
CERTIFIED SURVEY MAP NO. ____

Being all of Parcel 9 of Certified Survey Map No. 2273 in the Southwest 1/4 of the Northwest 1/4 of Section 27 and in the Southeast 1/4 of the Northeast 1/4 of Section 28, Township 1 North, Range 22 East, Village of Pleasant Prairie, Kenosha County, Wisconsin

VICINITY MAP

SCALE 1":1000'

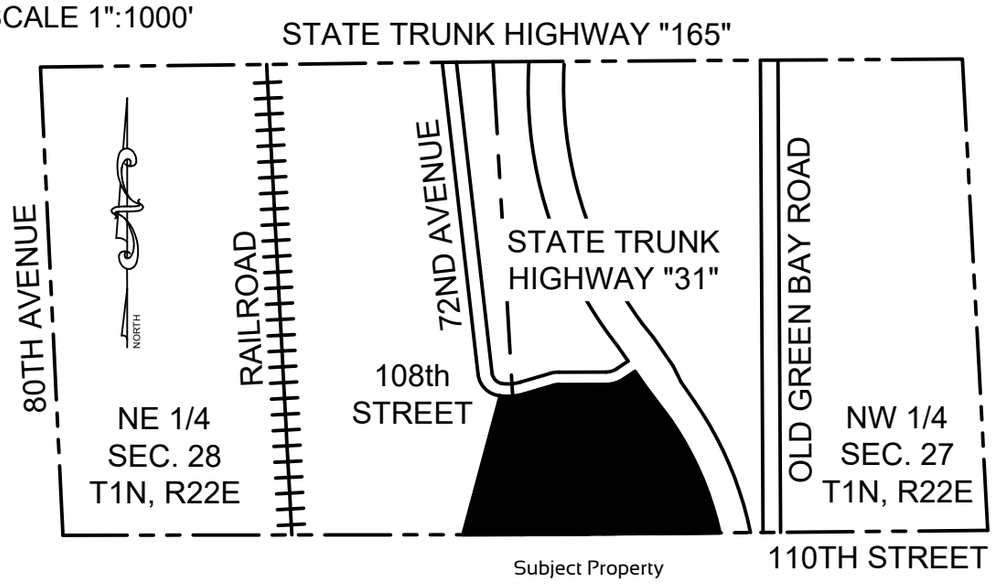

Subject Property
Zoning: M-2 & C-1
Tax Key Number:
92-4-122-272-0502

WISCONSIN
JESSE
LAND SURVEYOR

DRAFT

Jesse Zoltowski

SEPTEMBER 22, 2026

Prepared for:
TI INVESTORS OF LAKEVIEW
NITTO PARCEL LLC
710 N Plankinton Avenue
Milwaukee, WI 53203

NOTES:

1. All measurements have been made to the nearest one-hundredth of a foot.
2. All angular measurement have been made to the nearest one second.
3. Coordinates referenced to the Wisconsin State Plane Coordinate System, South Zone (N.A.D. 1927). Bearings referenced to the south line of the Northwest 1/4 of Section 27, Township 1 North, Range 22 East has a bearing of S89°28'52"W.
4. Floodplain Area based on Village of Pleasant Prairie Floodplain Boundary Adjustment; State of Wisconsin Department of Natural Resources Floodplain Analysis Review, Un-named Tributary No. 1 to the Des Plains River, Village of Pleasant Prairie, Kenosha County; and Federal Emergency Management Agency (FEMA) Conditional Letter of Map Revision (CLOMR) Case No. 20-05-3166R for the revision of Flood Insurance Rate Map Community Panel No. 55059C0194D with an effective date of JUNE 19, 2012.
5. Wetland Areas based on Wetlands delineated by LANDCO2 April, 2026 and Wetland Fill Permits by the Wisconsin Department of Natural Resources and Army Corps of Engineers.
6. Building Setbacks per Declaration of Development Standards and Protective Covenants recorded in Document No. 1204261 : Street = 60 Feet; Side/Rear = 45 feet.


PREPARED BY:
PINNACLE ENGINEERING GROUP
20725 WATERTOWN ROAD | SUITE 100 |
BROOKFIELD, WI 53186
OFFICE: (262)754-8888

This instrument was drafted by Jesse Zoltowski, PLS-License No. S-3094

DRAFTED BY: ST
JOB #644.00
SHEET 1 OF 17

CERTIFIED SURVEY MAP NO. ____

Being all of Parcel 9 of Certified Survey Map No. 2273 in the Southwest 1/4 of the Northwest 1/4 of Section 27 and in the Southeast 1/4 of the Northeast 1/4 of Section 28, Township 1 North, Range 22 East, Village of Pleasant Prairie, Kenosha County, Wisconsin

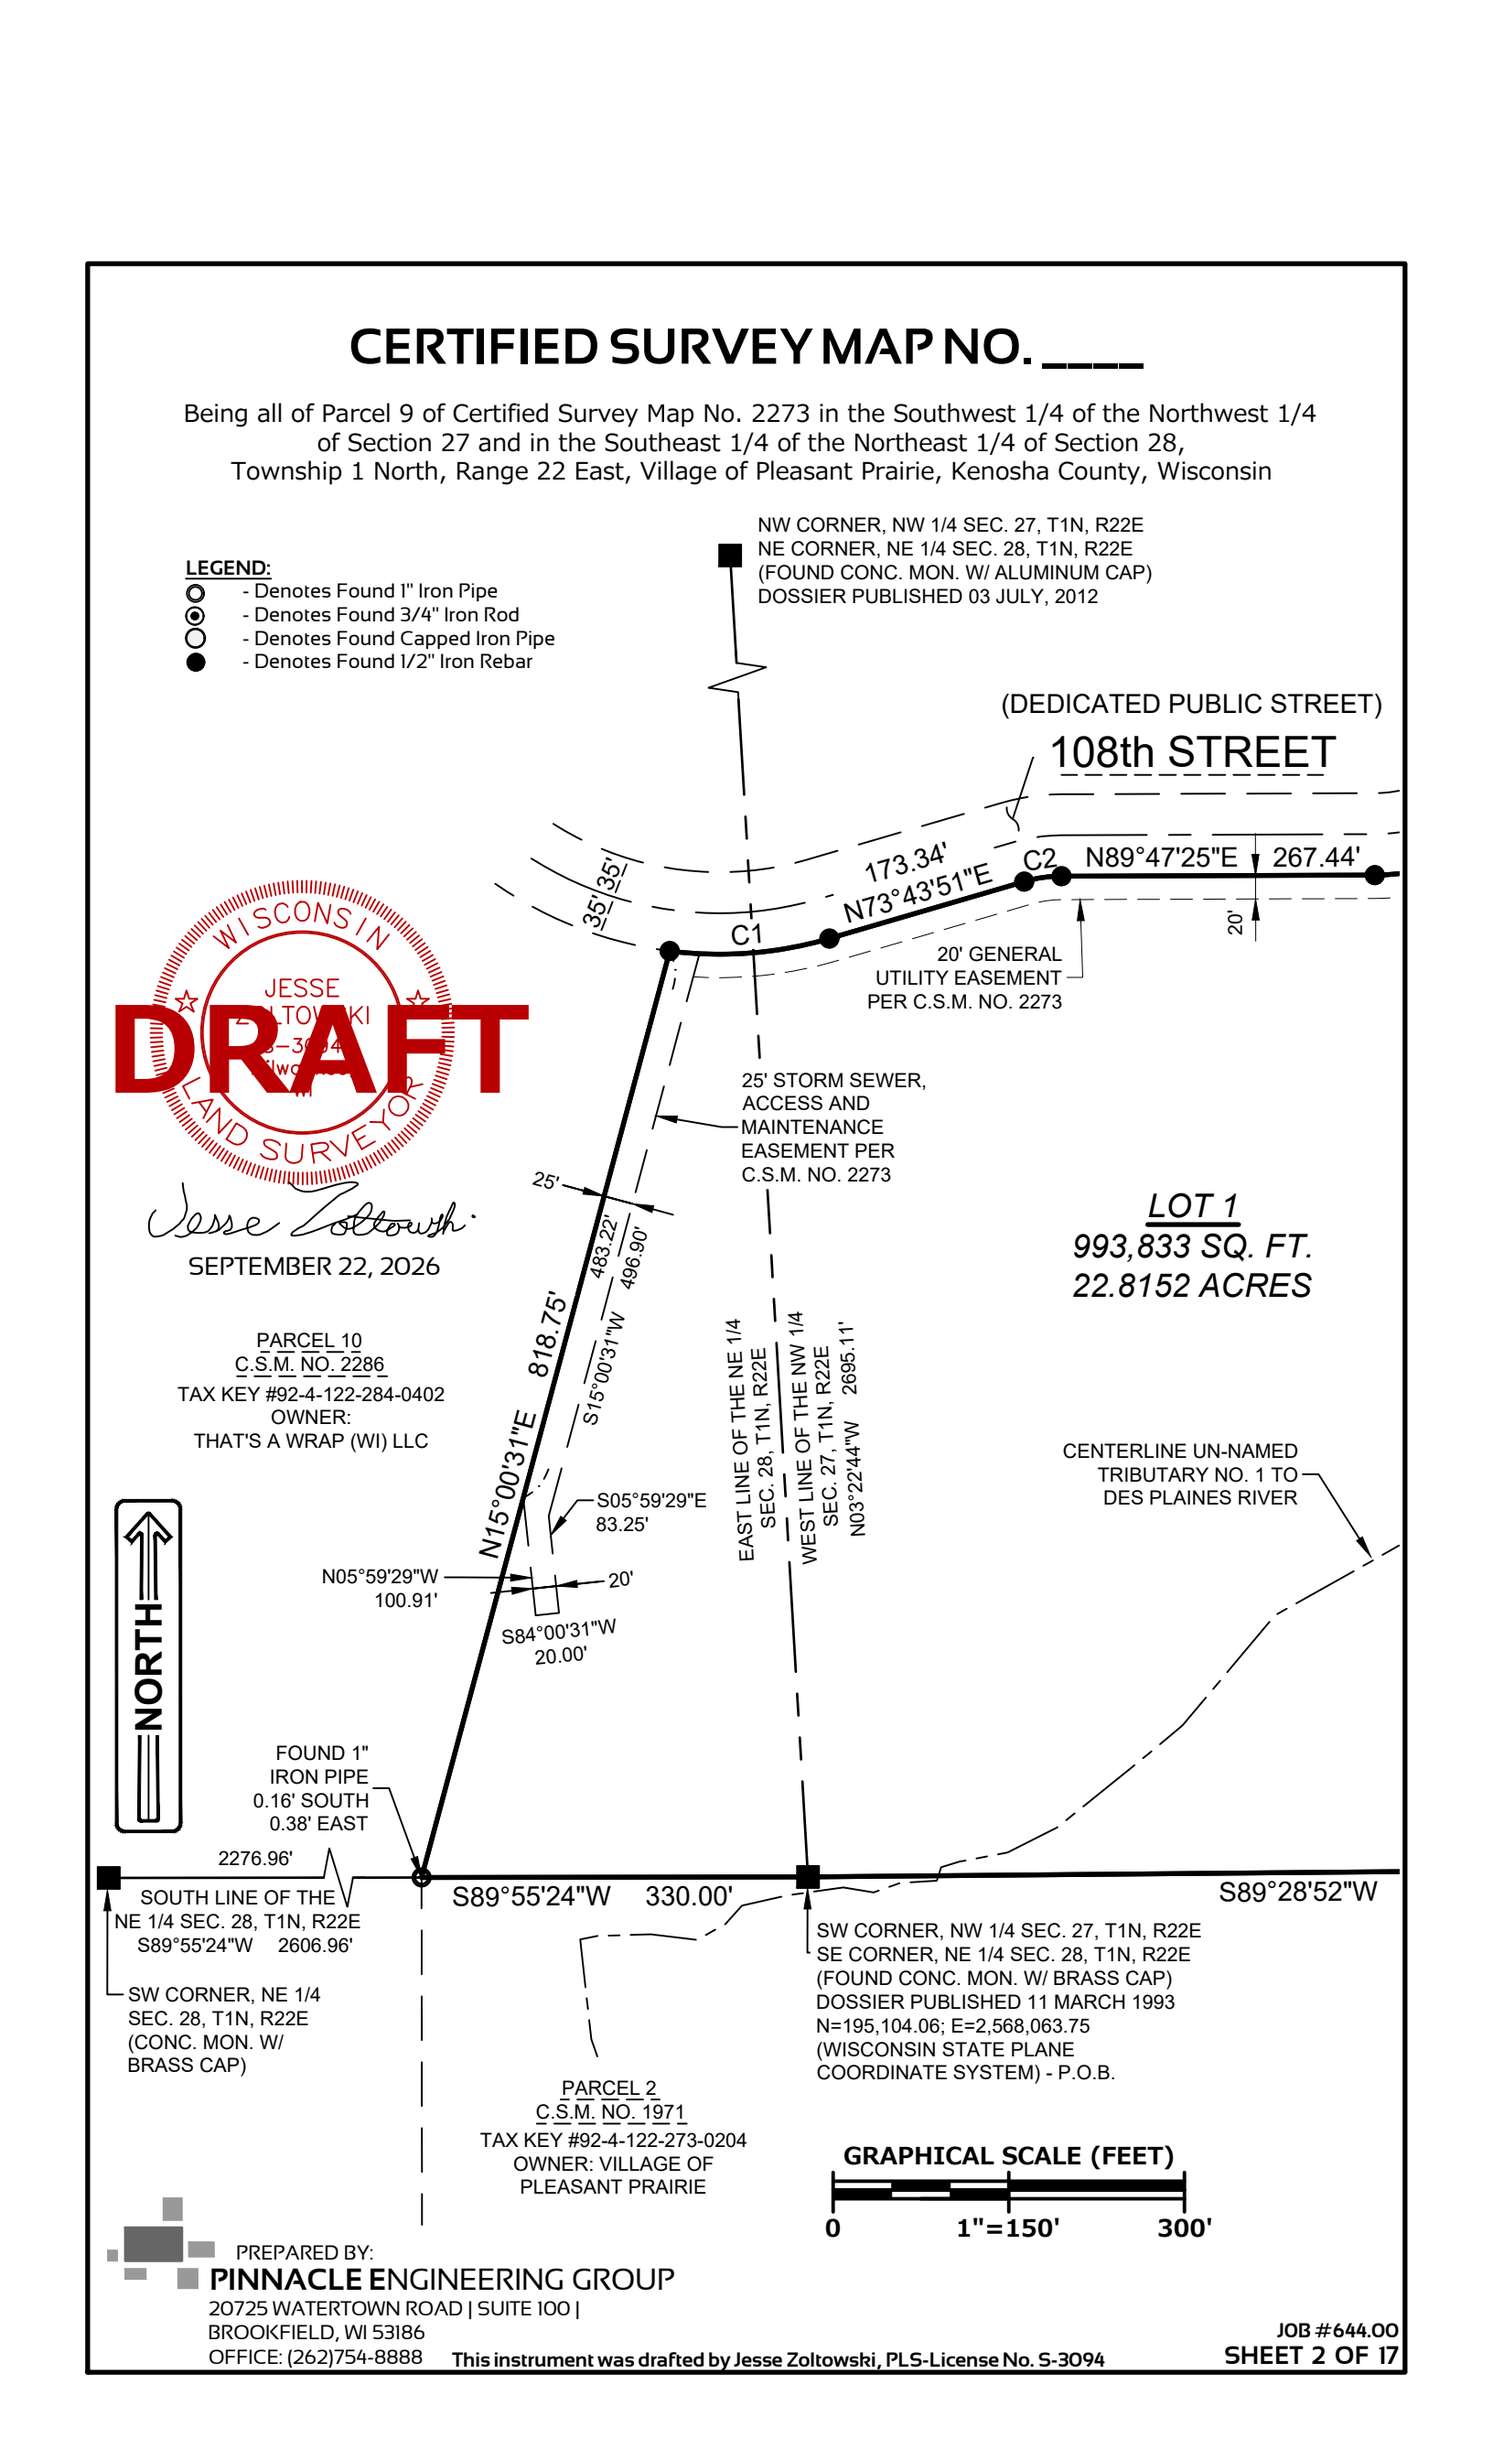


PREPARED BY:
PINNACLE ENGINEERING GROUP
20725 WATERTOWN ROAD | SUITE 100 |
BROOKFIELD, WI 53186
OFFICE: (262)754-8888

This instrument was drafted by Jesse Zoltowski, PLS-License No. S-3094

CERTIFIED SURVEY MAP NO. ____

Being all of Parcel 9 of Certified Survey Map No. 2273 in the Southwest 1/4 of the Northwest 1/4 of Section 27 and in the Southeast 1/4 of the Northeast 1/4 of Section 28, Township 1 North, Range 22 East, Village of Pleasant Prairie, Kenosha County, Wisconsin

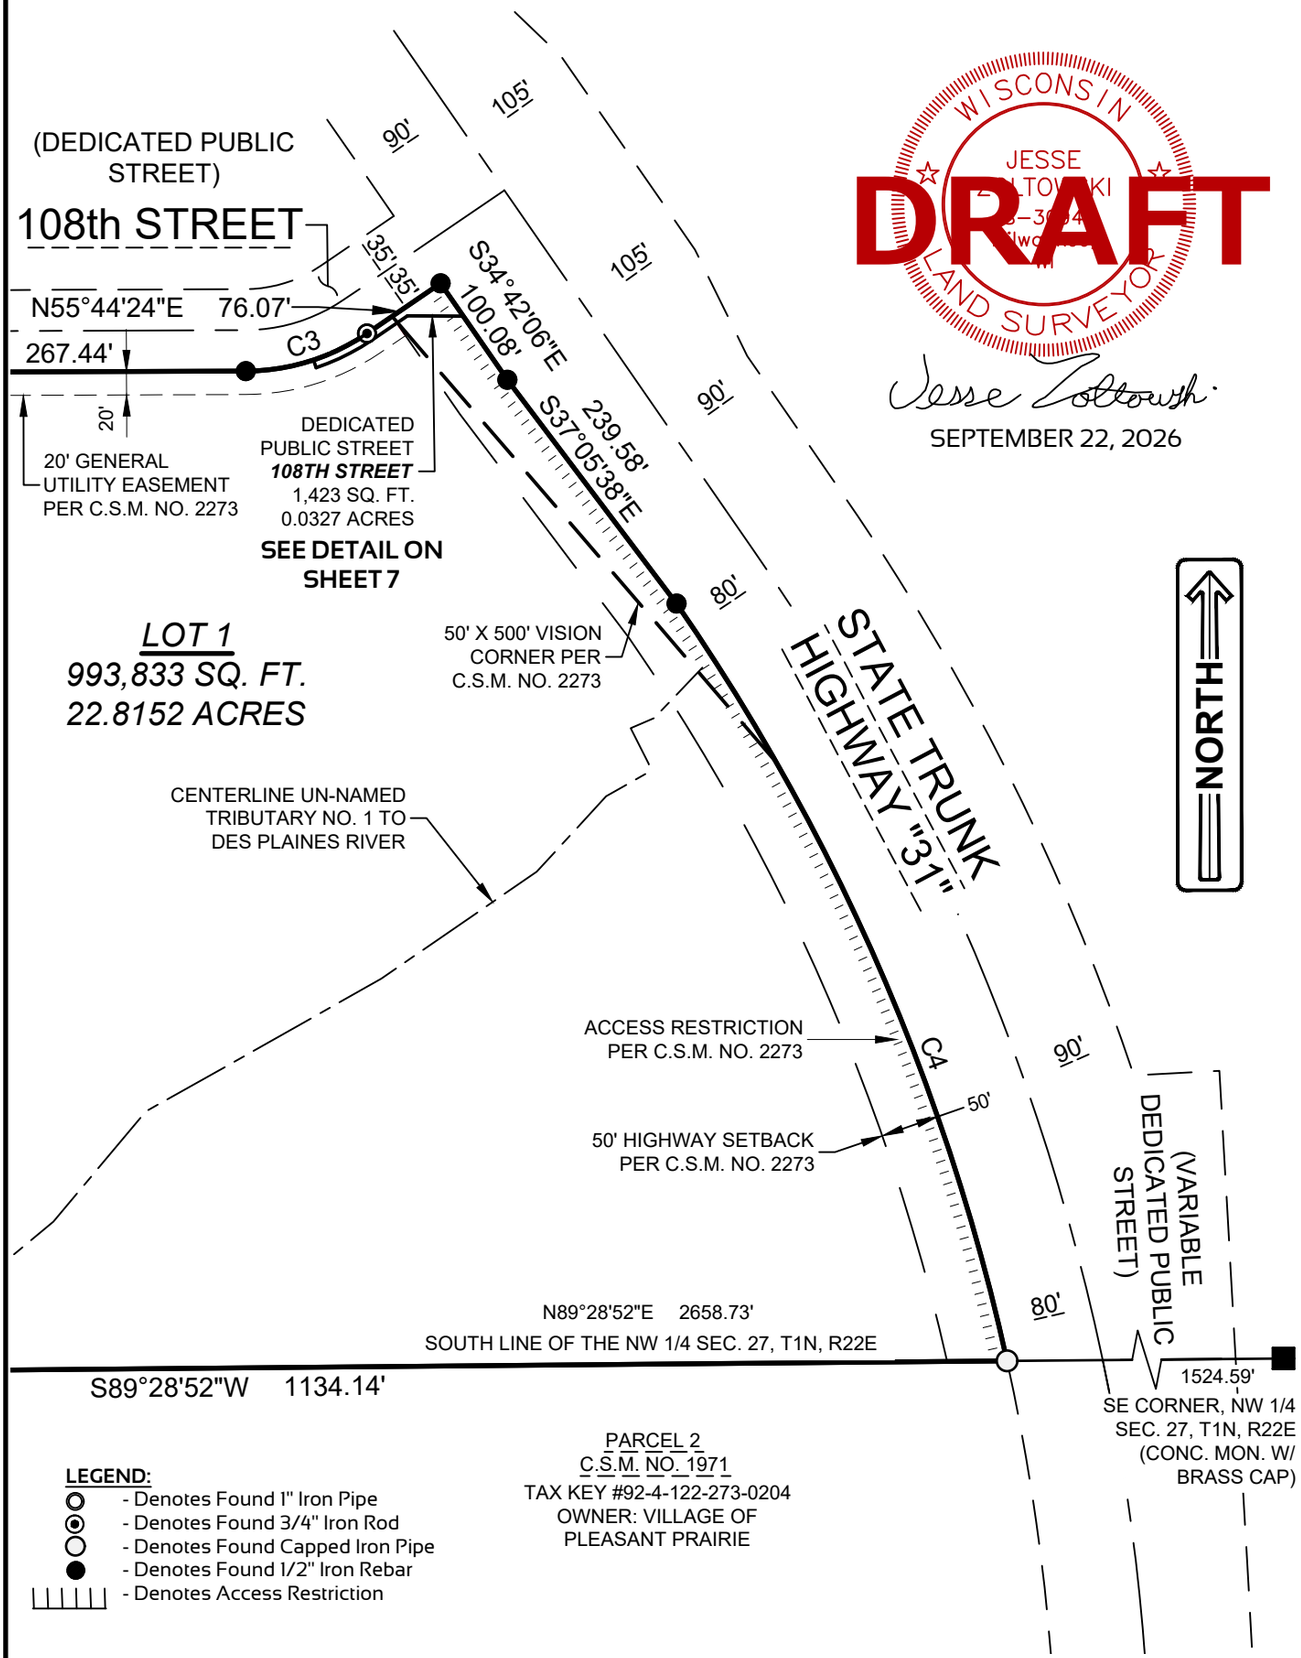

DRAFT

WISCONSIN JESSE ZOLTOWSKI S-3094 LAND SURVEYOR

Jesse Zoltowski

SEPTEMBER 22, 2026

LEGEND:

- ○ - Denotes Found 1" Iron Pipe
- ◉ - Denotes Found 3/4" Iron Rod
- ○ - Denotes Found Capped Iron Pipe
- ● - Denotes Found 1/2" Iron Rebar
- ||||| - Denotes Access Restriction

GRAPHICAL SCALE (FEET)


0 1"=150' 300'

PREPARED BY:
PINNACLE ENGINEERING GROUP
20725 WATERTOWN ROAD | SUITE 100 |
BROOKFIELD, WI 53186
OFFICE: (262)754-8888

This instrument was drafted by Jesse Zoltowski, PLS-License No. S-3094

CERTIFIED SURVEY MAP NO. ____

Being all of Parcel 9 of Certified Survey Map No. 2273 in the Southwest 1/4 of the Northwest 1/4 of Section 27 and in the Southeast 1/4 of the Northeast 1/4 of Section 28, Township 1 North, Range 22 East, Village of Pleasant Prairie, Kenosha County, Wisconsin

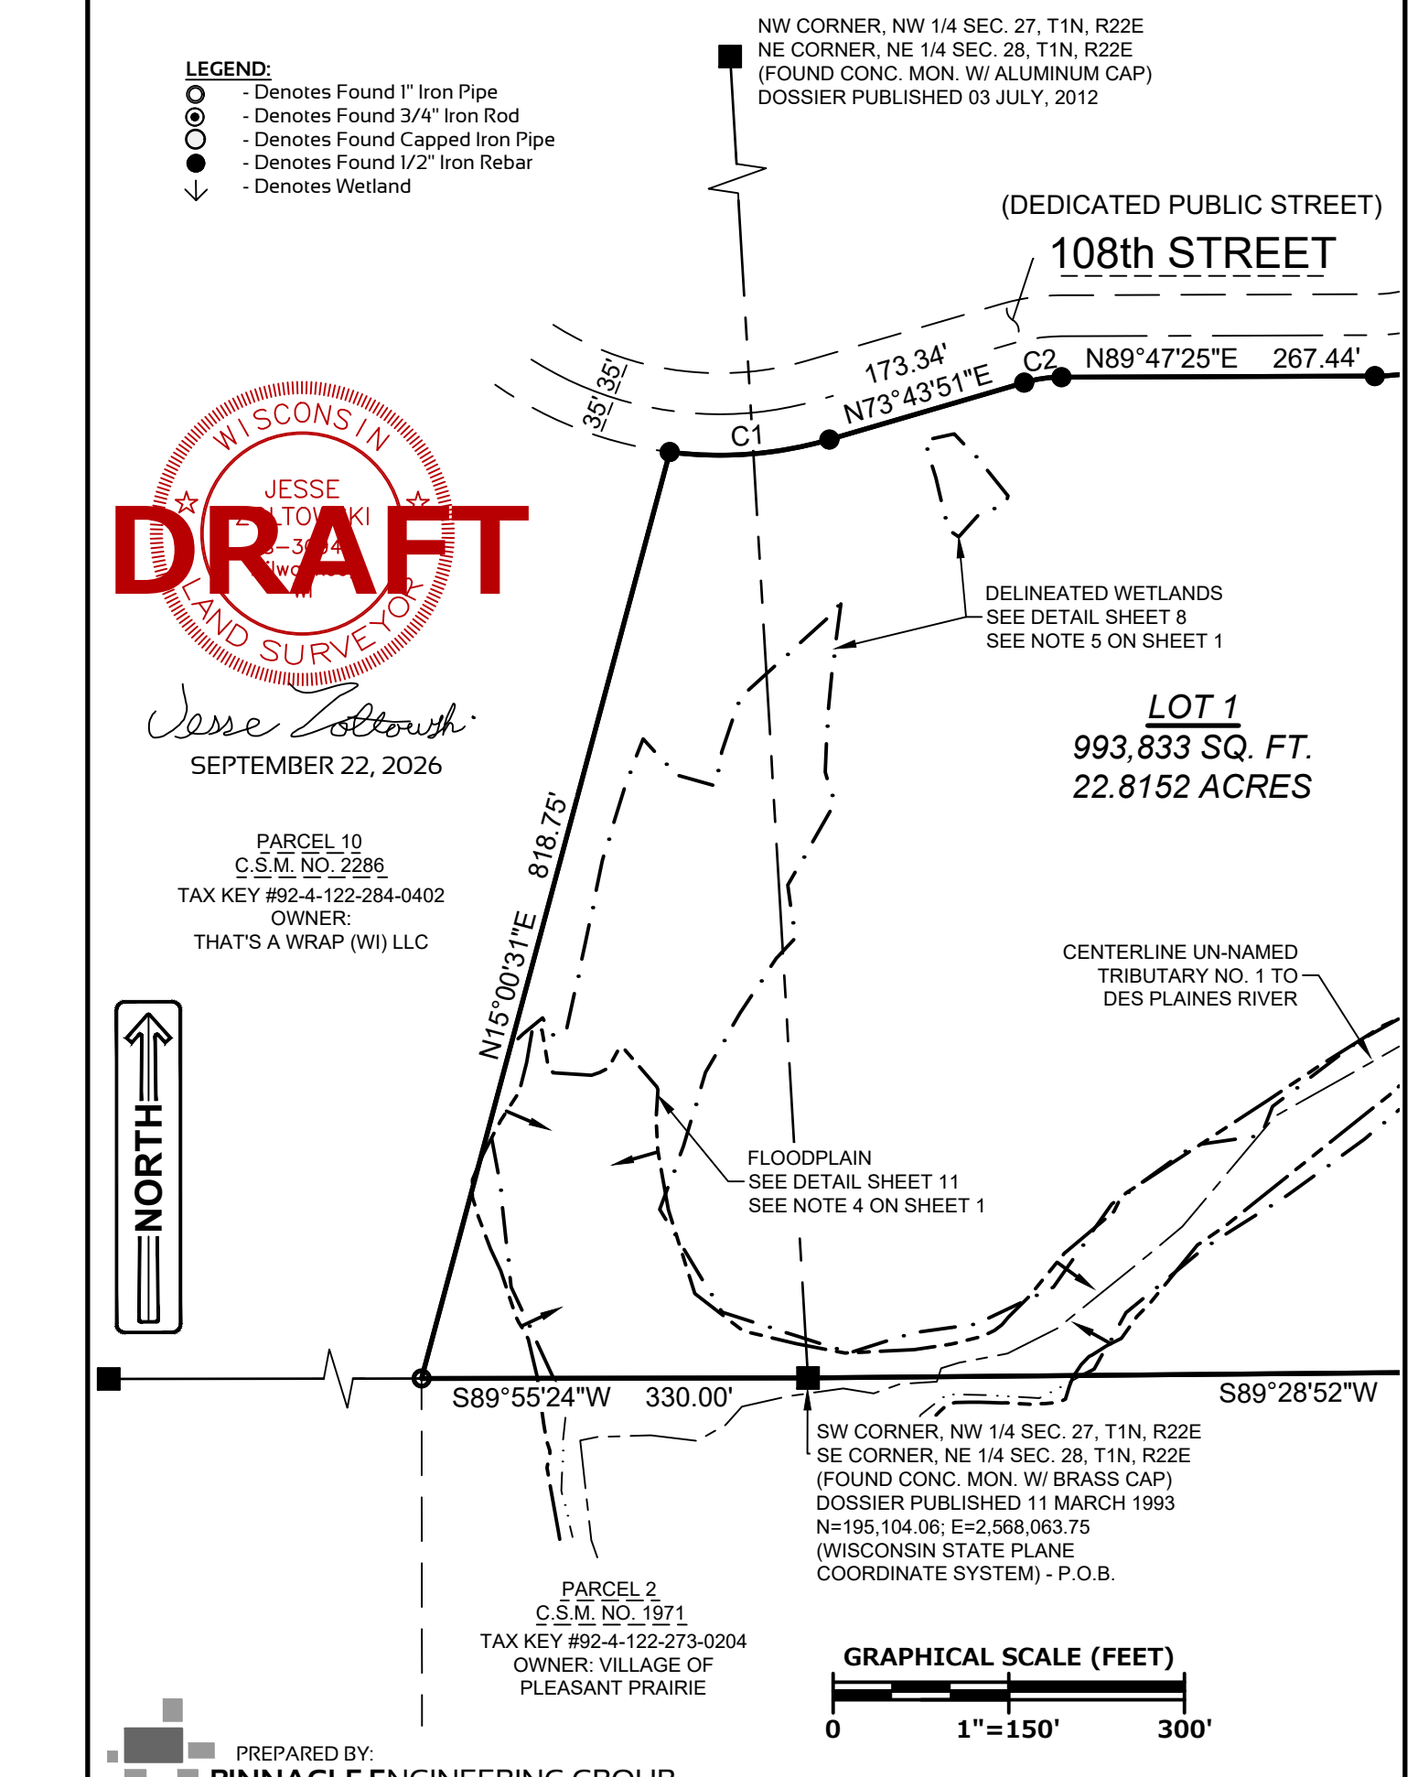


PREPARED BY:
PINNACLE ENGINEERING GROUP
20725 WATERTOWN ROAD | SUITE 100 |
BROOKFIELD, WI 53186
OFFICE: (262)754-8888

This instrument was drafted by Jesse Zoltowski, PLS-License No. S-3094

CERTIFIED SURVEY MAP NO. ____

Being all of Parcel 9 of Certified Survey Map No. 2273 in the Southwest 1/4 of the Northwest 1/4 of Section 27 and in the Southeast 1/4 of the Northeast 1/4 of Section 28, Township 1 North, Range 22 East, Village of Pleasant Prairie, Kenosha County, Wisconsin

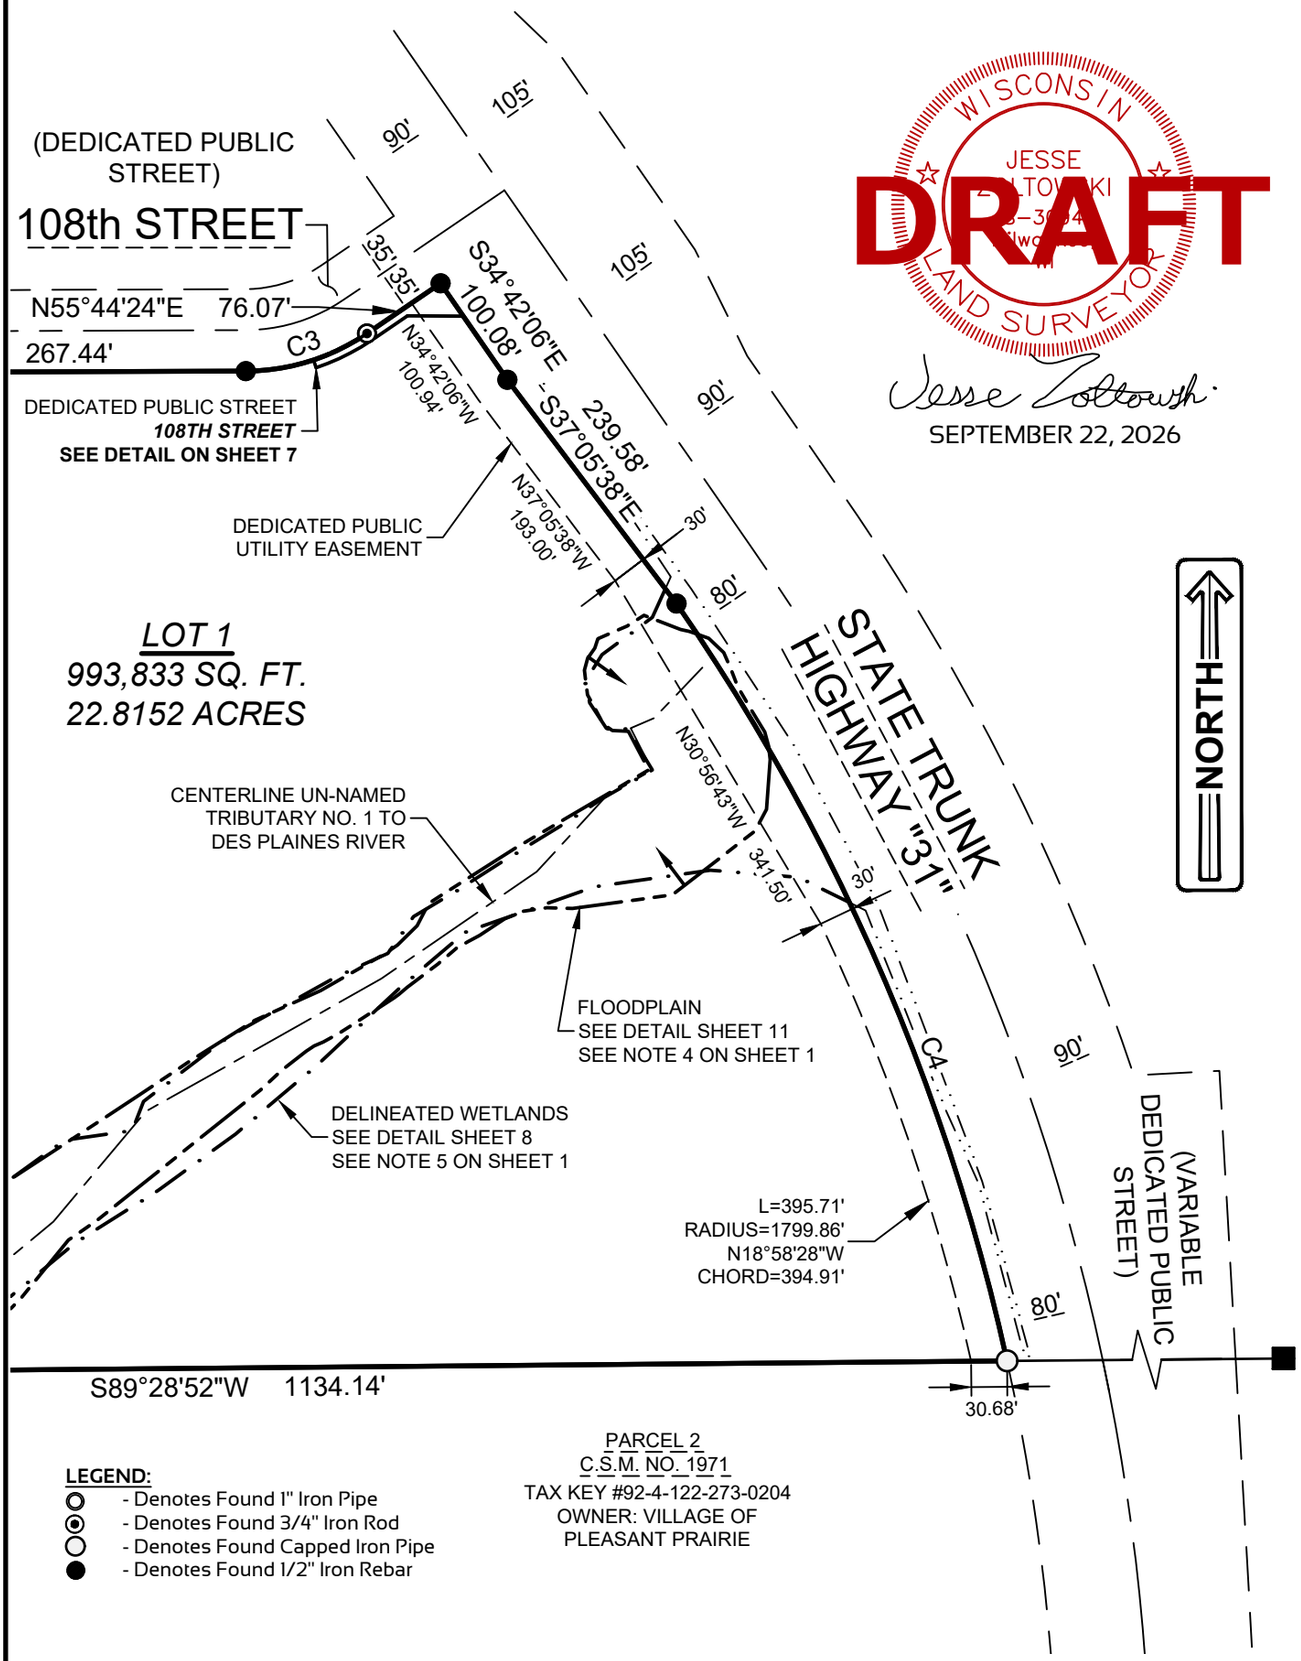

DRAFT

WISCONSIN JESSE ZOLTOWSKI S-3094 LAND SURVEYOR

Jesse Zoltowski

SEPTEMBER 22, 2026

PARCEL 2
C.S.M. NO. 1971
TAX KEY #92-4-122-273-0204
OWNER: VILLAGE OF PLEASANT PRAIRIE

LEGEND:

- ○ - Denotes Found 1" Iron Pipe
- ◉ - Denotes Found 3/4" Iron Rod
- ○ - Denotes Found Capped Iron Pipe
- ● - Denotes Found 1/2" Iron Rebar

GRAPHICAL SCALE (FEET)


0 1"=150' 300'

PREPARED BY:
PINNACLE ENGINEERING GROUP
20725 WATERTOWN ROAD | SUITE 100 |
BROOKFIELD, WI 53186
OFFICE: (262)754-8888

This instrument was drafted by Jesse Zoltowski, PLS-License No. S-3094

CERTIFIED SURVEY MAP NO. ____

Being all of Parcel 9 of Certified Survey Map No. 2273 in the Southwest 1/4 of the Northwest 1/4 of Section 27 and in the Southeast 1/4 of the Northeast 1/4 of Section 28, Township 1 North, Range 22 East, Village of Pleasant Prairie, Kenosha County, Wisconsin

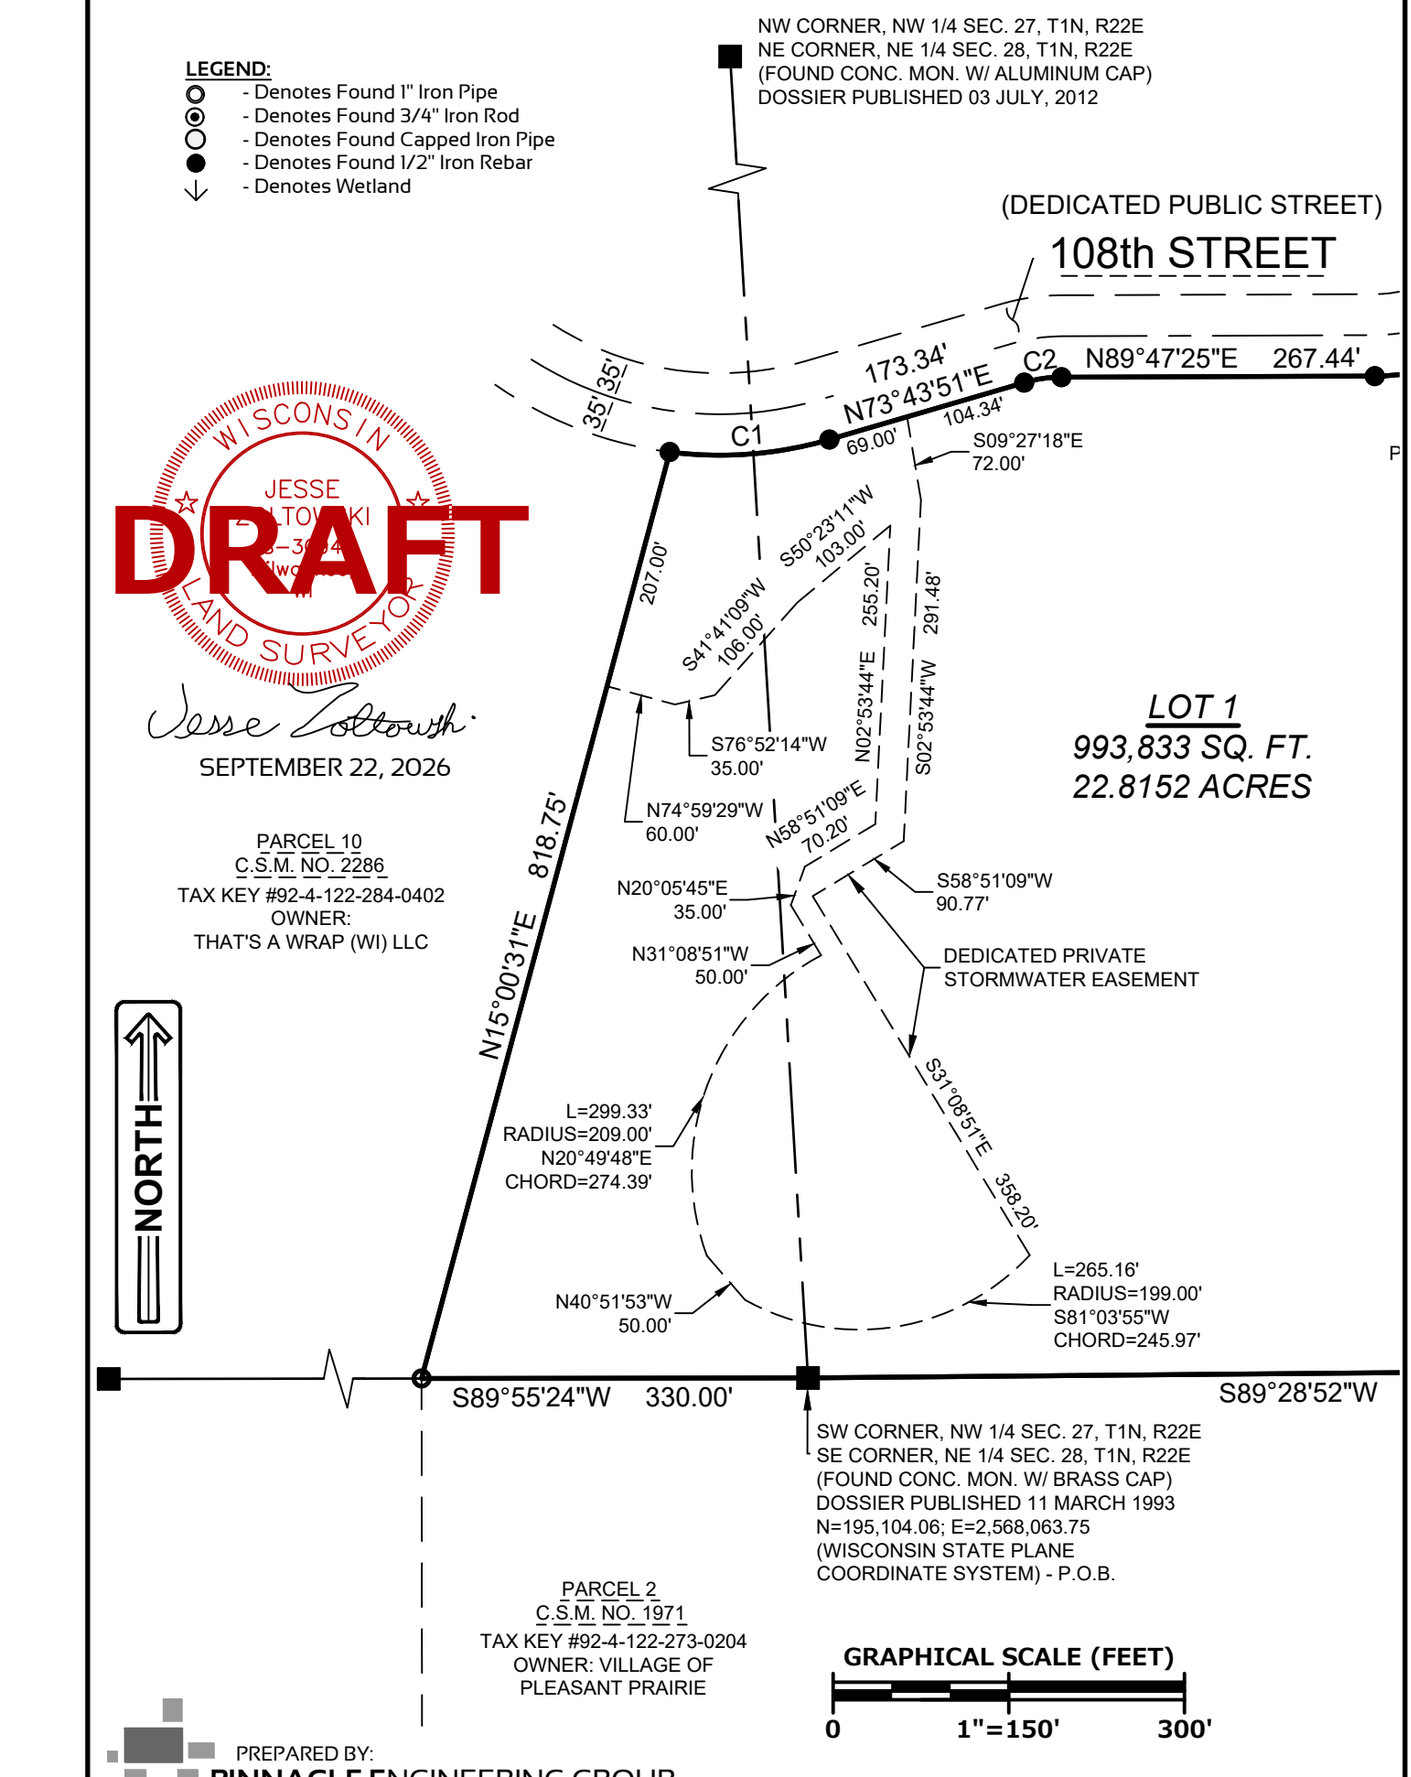


PREPARED BY:
PINNACLE ENGINEERING GROUP
20725 WATERTOWN ROAD | SUITE 100 |
BROOKFIELD, WI 53186
OFFICE: (262)754-8888

This instrument was drafted by Jesse Zoltowski, PLS-License No. S-3094

CERTIFIED SURVEY MAP NO. ____

Being all of Parcel 9 of Certified Survey Map No. 2273 in the Southwest 1/4 of the Northwest 1/4 of Section 27 and in the Southeast 1/4 of the Northeast 1/4 of Section 28, Township 1 North, Range 22 East, Village of Pleasant Prairie, Kenosha County, Wisconsin

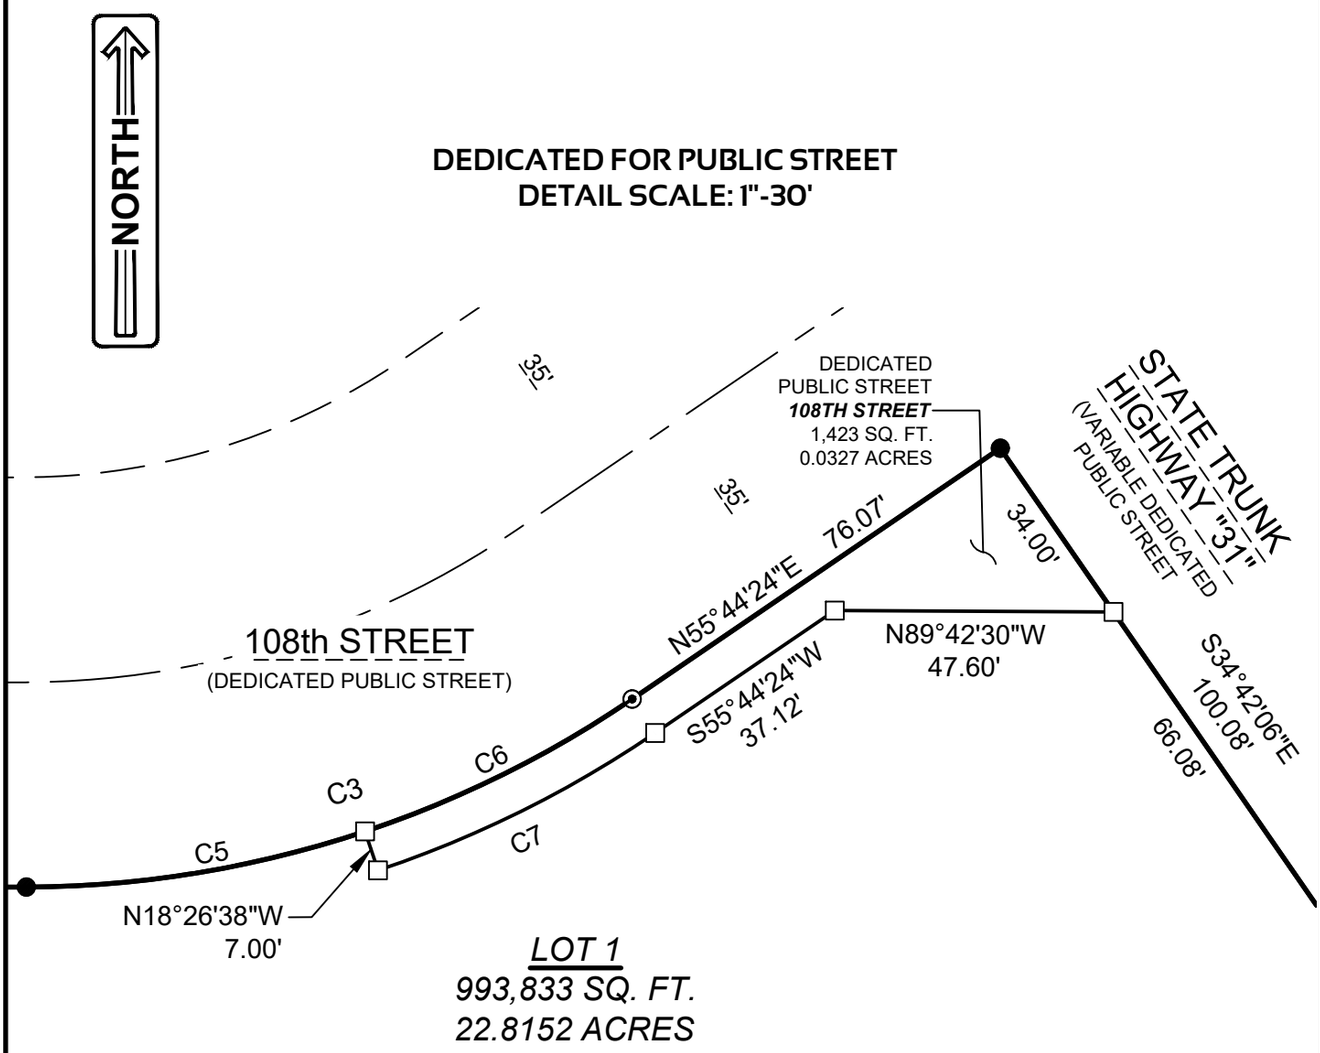

LEGEND:

- ◉ - Denotes Found 3/4" Iron Rod
- ● - Denotes Found Capped Iron Pipe
- □ - Denotes Set 1-1/4" X 18" Iron Rod, 4.30 LBS./FT.

WISCONSIN
JESSE
ZOLTOWSKI
S-3094
LAND SURVEYOR

DRAFT

Jesse Zoltowski

SEPTEMBER 22, 2026


PREPARED BY:
PINNACLE ENGINEERING GROUP
20725 WATERTOWN ROAD | SUITE 100 |
BROOKFIELD, WI 53186
OFFICE: (262)754-8888

This instrument was drafted by Jesse Zoltowski, PLS-License No. S-3094

CERTIFIED SURVEY MAP NO. ____

Being all of Parcel 9 of Certified Survey Map No. 2273 in the Southwest 1/4 of the Northwest 1/4 of Section 27 and in the Southeast 1/4 of the Northeast 1/4 of Section 28, Township 1 North, Range 22 East, Village of Pleasant Prairie, Kenosha County, Wisconsin

WETLAND DETAIL

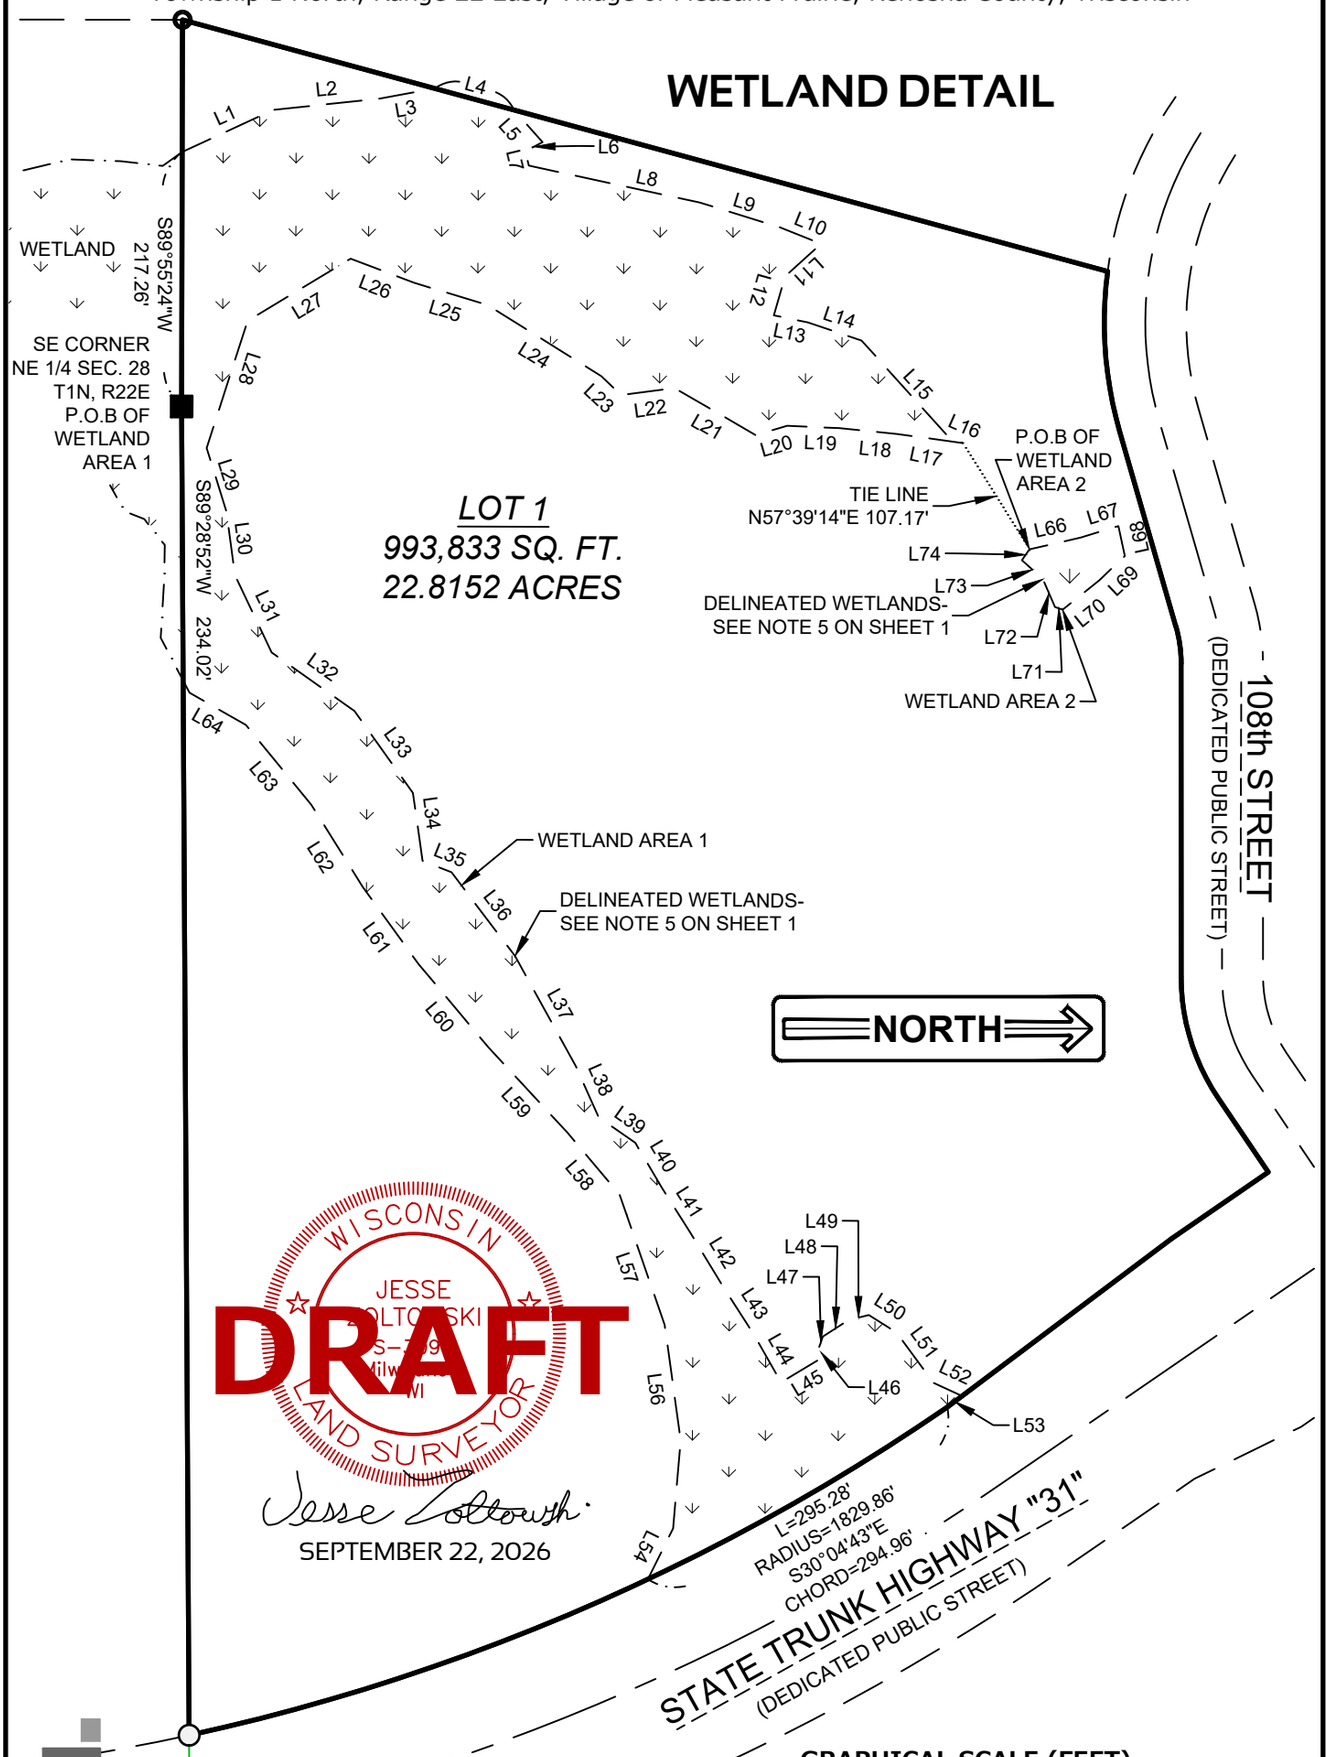

WISCONSIN
JESSE ZOLTOWSKI
S-3094
MILWAUKEE
WI
LAND SURVEYOR

DRAFT

Jesse Zoltowski
SEPTEMBER 22, 2026

GRAPHICAL SCALE (FEET)
0 1"=150' 300'

PREPARED BY:
PINNACLE ENGINEERING GROUP
20725 WATERTOWN ROAD | SUITE 100 |
BROOKFIELD, WI 53186
OFFICE: (262)754-8888

This instrument was drafted by Jesse Zoltowski, PLS-License No. S-3094

CERTIFIED SURVEY MAP NO. ____

Being all of Parcel 9 of Certified Survey Map No. 2273 in the Southwest 1/4 of the Northwest 1/4 of Section 27 and in the Southeast 1/4 of the Northeast 1/4 of Section 28, Township 1 North, Range 22 East, Village of Pleasant Prairie, Kenosha County, Wisconsin

WETLAND LINE TABLE

LINE TABLE		
LINE NO.	BEARING	DISTANCE
L1	N24°56'25"W	85.91'
L2	N06°13'02"W	91.03'
L3	N10°31'14"W	48.11'
L4	N15°00'31"E	69.89'
L5	N48°06'52"E	36.70'
L6	S28°21'02"E	16.62'
L7	N76°15'19"E	12.58'
L8	N11°58'24"E	149.07'
L9	N16°57'36"E	71.92'
L10	N21°38'10"E	37.86'
L11	S42°09'54"E	41.37'
L12	S74°15'59"E	34.72'
L13	N11°34'32"E	29.62'
L14	N18°25'48"E	48.36'
L15	N47°43'09"E	110.81'
L16	N23°32'31"E	13.14'
L17	S07°42'23"W	56.76'
L18	S05°34'57"W	49.21'
L19	S02°19'08"W	44.67'
L20	S16°20'32"E	28.13'
L21	S29°54'04"W	80.01'
L22	S07°45'10"E	45.92'
L23	S43°19'22"W	23.48'
L24	S31°49'42"W	114.47'
L25	S16°37'44"W	65.97'

LINE TABLE		
LINE NO.	BEARING	DISTANCE
L26	S20°37'17"W	57.52'
L27	S31°16'55"E	102.71'
L28	S72°17'54"E	114.06'
L29	N72°26'21"E	56.32'
L30	N82°03'00"E	55.42'
L31	N64°25'36"E	72.83'
L32	N35°03'37"E	86.62'
L33	N54°15'30"E	85.94'
L34	N81°45'53"E	58.54'
L35	N21°20'04"E	26.61'
L36	N52°37'49"E	89.75'
L37	N60°53'40"E	107.37'
L38	N65°38'46"E	47.77'
L39	N34°46'46"E	38.20'
L40	N59°09'51"E	44.25'
L41	N57°26'50"E	43.69'
L42	N58°25'29"E	61.33'
L43	N56°55'17"E	43.01'
L44	N60°14'36"E	47.07'
L45	N31°11'30"W	41.83'
L46	S67°21'03"W	9.01'
L47	N70°40'50"W	9.84'
L48	N33°00'25"W	25.94'
L49	N13°55'40"W	17.91'
L50	N31°47'09"E	27.93'

LINE TABLE		
LINE NO.	BEARING	DISTANCE
L51	N53°31'53"E	53.48'
L52	N24°31'16"E	26.80'
L53	S37°05'38" E	15.78'
L54	N63°44'04"W	48.61'
L55	N85°20'44"W	75.63'
L56	S81°52'51"W	99.22'
L57	S70°43'07"W	117.70'
L58	S49°40'14"W	69.17'
L59	S46°58'41"W	98.61'
L60	S49°45'31"W	93.14'
L61	S53°55'23"W	81.57'
L62	S57°44'21"W	82.86'
L63	S50°26'04"W	87.94'
L64	S29°32'39"W	55.46'
L65	S62°03'33"W	11.63'
L66	N13°09'45"W	45.20'
L67	N17°10'48"W	33.38'
L68	N77°34'50"E	26.08'
L69	S43°49'21"E	30.04'
L70	S38°55'15"E	40.15'
L71	S18°31'56"W	6.87'
L72	S66°12'04"W	25.87'
L73	S42°04'30"W	24.18'
L74	N55°49'39"W	11.22'



Jesse Zoltowski

SEPTEMBER 22, 2026

PREPARED BY:
PINNACLE ENGINEERING GROUP
20725 WATERTOWN ROAD | SUITE 100 |
BROOKFIELD, WI 53186
OFFICE: (262)754-8888

This instrument was drafted by Jesse Zoltowski, PLS-License No. S-3094

CERTIFIED SURVEY MAP NO. ____

Being all of Parcel 9 of Certified Survey Map No. 2273 in the Southwest 1/4 of the Northwest 1/4 of Section 27 and in the Southeast 1/4 of the Northeast 1/4 of Section 28, Township 1 North, Range 22 East, Village of Pleasant Prairie, Kenosha County, Wisconsin

LEGAL DESCRIPTION OF WETLAND AREA 1:

Being a part of Parcel 9 of CERTIFIED SURVEY MAP NO. 2273, as recorded in the Office of the Register of Deeds for Kenosha County as Document No. 1239083, in the Southwest 1/4 of the Northwest 1/4 of Section 27 and in the Southeast 1/4 of the Northeast 1/4 of Section 28, Township 1 North, Range 22 East, Village of Pleasant Prairie, Kenosha County, Wisconsin, described as follows:

Beginning at the southeast corner of the Northeast 1/4 of said Section 28; thence South 89°55'24" West along the south line of said Northeast 1/4, 217.26 feet; thence North 24°56'25" West, 85.91 feet; thence North 06°13'02" West, 91.03 feet; thence North 10°31'14" West, 48.11 feet; thence North 15°00'31" East, 69.89 feet; thence North 48°06'52" East, 36.70 feet; thence South 28°21'02" East, 16.62 feet; thence North 76°15'19" East, 12.58 feet; thence North 11°58'24" East, 149.07 feet; thence North 16°57'36" East, 71.92 feet; thence North 21°38'10" East, 37.86 feet; thence South 42°09'54" East, 41.37 feet; thence South 74°15'59" East, 34.72 feet; thence North 11°34'32" East, 29.62 feet; thence North 18°25'48" East, 48.36 feet; thence North 47°43'09" East, 110.81 feet; thence North 23°32'31" East, 13.14 feet to a "Tie Line"; thence South 07°42'23" West, 56.76 feet; thence South 05°34'57" West, 49.21 feet; thence South 02°19'08" West, 44.67 feet; thence South 16°20'32" East, 28.13 feet; thence South 29°54'04" West, 80.01 feet; thence South 07°45'10" East, 45.92 feet; thence South 43°19'22" West, 23.48 feet; thence South 31°49'42" West, 114.47 feet; thence South 16°37'44" West, 65.97 feet; thence South 20°37'17" West, 57.52 feet; thence South 31°16'55" East, 102.71 feet; thence South 72°17'54" East, 114.06 feet; thence North 72°26'21" East, 56.32 feet; thence North 82°03'00" East, 55.42 feet; thence North 64°25'36" East, 72.83 feet; thence North 35°03'37" East, 86.62 feet; thence North 54°15'30" East, 85.94 feet; thence North 81°45'53" East, 58.54 feet; thence North 21°20'04" East, 26.61 feet; thence North 52°37'49" East, 89.75 feet; thence North 60°53'40" East, 107.37 feet; thence North 65°38'46" East, 47.77 feet; thence North 34°46'46" East, 38.20 feet; thence North 59°09'51" East, 44.25 feet; thence North 57°26'50" East, 43.69 feet; thence North 58°25'29" East, 61.33 feet thence North 56°55'17" East, 43.01 feet; thence North 60°14'36" East, 47.07 feet; thence North 31°11'30" West, 41.83 feet; thence South 67°21'03" West, 9.01 feet; thence North 70°40'50" West, 9.84 feet; thence North 33°00'25" West, 25.94 feet; thence North 13°55'40" West, 17.91 feet; thence North 31°47'09" East, 27.93 feet; thence North 53°31'53" East, 53.48 feet; thence North 24°31'16" East, 26.80 feet to the east line of said Parcel 9; thence South 37°05'38" East along said east line of Parcel 9, 15.78 feet to a point on a curve; thence southeasterly 295.28 feet along the arc of said curve to the right, whose radius is 1829.86 feet and whose chord bears South 30°04'43" East, 294.96 feet; thence North 63°44'04" West, 48.61 feet; thence North 85°20'44" West, 75.63 feet; thence South 81°52'51" West, 99.22 feet; thence South 70°43'07" West, 117.70 feet; thence South 49°40'14" West, 69.17 feet; thence South 46°58'41" West, 98.61 feet; thence South 49°45'31" West, 93.14 feet; thence South 53°55'23" West, 81.57 feet; thence South 57°44'21" West, 82.86 feet; thence South 50°26'04" West, 87.94 feet; thence South 29°32'39" West, 55.46 feet; thence South 62°03'33" West, 11.63 feet to the south line of the Northwest 1/4 of said Section 27; thence South 89°28'52" West along said south line, 234.02 feet to the Point of Beginning.

LEGAL DESCRIPTION OF WETLAND AREA 2:

Being a part of Parcel 9 of CERTIFIED SURVEY MAP NO. 2273, as recorded in the Office of the Register of Deeds for Kenosha County as Document No. 1239083, in the Southwest 1/4 of the Northwest 1/4 of Section 27 and in the Southeast 1/4 of the Northeast 1/4 of Section 28, Township 1 North, Range 22 East, Village of Pleasant Prairie, Kenosha County, Wisconsin, described as follows:

Commencing at the southeast corner of the Northeast 1/4 of said Section 28; thence South 89°55'24" West along the south line of said Northeast 1/4, 217.26 feet; thence North 24°56'25" West, 85.91 feet; thence North 06°13'02" West, 91.03 feet; thence North 10°31'14" West, 48.11 feet; thence North 15°00'31" East, 69.89 feet; thence North 48°06'52" East, 36.70 feet; thence South 28°21'02" East, 16.62 feet; thence North 76°15'19" East, 12.58 feet; thence North 11°58'24" East, 149.07 feet; thence North 16°57'36" East, 71.92 feet; thence North 21°38'10" East, 37.86 feet; thence South 42°09'54" East, 41.37 feet; thence South 74°15'59" East, 34.72 feet; thence North 11°34'32" East, 29.62 feet; thence North 18°25'48" East, 48.36 feet; thence North 47°43'09" East, 110.81 feet; thence North 23°32'31" East, 13.14 feet to a "Tie Line"; thence North 57°39'14" East, along said "Tie Line", 107.17 feet to the Point of Beginning of Wetland Area 2;

Thence North 13°09'45" West, 45.20 feet; thence North 17°10'48" West, 33.38 feet; thence North 77°34'50" East, 26.08 feet; thence South 43°49'21" East, 30.04 feet; thence South 38°55'15" East, 40.15 feet; thence South 18°31'56" West, 6.87 feet; thence South 66°12'04" West, 25.87 feet; thence South 42°04'30" West, 24.18 feet; thence North 55°49'39" West, 1 1.22 to the aforesaid "Tie Line" and the Point of Beginning of Wetland Area 2.

WISCONSIN
JESSE
LTOWSKI
3-3094
LAND SURVEYOR

DRAFT

Jesse Zoltowski

SEPTEMBER 22, 2026

PREPARED BY:
PINNACLE ENGINEERING GROUP
20725 WATERTOWN ROAD | SUITE 100 |
BROOKFIELD, WI 53186
OFFICE: (262)754-8888

This instrument was drafted by Jesse Zoltowski, PLS-License No. S-3094

CERTIFIED SURVEY MAP NO. ____

Being all of Parcel 9 of Certified Survey Map No. 2273 in the Southwest 1/4 of the Northwest 1/4 of Section 27 and in the Southeast 1/4 of the Northeast 1/4 of Section 28, Township 1 North, Range 22 East, Village of Pleasant Prairie, Kenosha County, Wisconsin

FLOODPLAIN DETAIL



WISCONSIN JESSE ZOLTOWSKI S-3094 LAND SURVEYOR

DRAFT

Jesse Zoltowski

SEPTEMBER 22, 2026

LOT 1
993,833 SQ. FT.
22.8152 ACRES

GRAPHICAL SCALE (FEET)
0 1"=150' 300'

PREPARED BY:
PINNACLE ENGINEERING GROUP
20725 WATERTOWN ROAD | SUITE 100 |
BROOKFIELD, WI 53186
OFFICE: (262)754-8888

This instrument was drafted by Jesse Zoltowski, PLS-License No. S-3094

JOB #644.00

CERTIFIED SURVEY MAP NO. ____

Being all of Parcel 9 of Certified Survey Map No. 2273 in the Southwest 1/4 of the Northwest 1/4 of Section 27 and in the Southeast 1/4 of the Northeast 1/4 of Section 28, Township 1 North, Range 22 East, Village of Pleasant Prairie, Kenosha County, Wisconsin

FLOODPLAIN LINE TABLE

LINE TABLE		
LINE NO.	BEARING	DISTANCE
L1	N07°51'47"W	1.32'
L2	N13°21'43"W	33.01'
L3	N24°41'24"W	5.43'
L4	N31°22'22"W	11.30'
L5	N27°01'22"W	5.29'
L6	N18°10'54"W	41.24'
L7	N25°10'14"W	20.62'
L8	N20°41'44"W	29.63'
L9	N16°49'52"W	17.34'
L10	N00°27'27"E	14.75'
L11	N22°44'22"E	23.00'
L12	N27°24'14"E	32.98'
L13	N32°56'12"E	29.20'
L14	N14°05'52"E	25.69'
L15	N09°45'08"E	27.90'
L16	N88°06'07"E	8.22'
L17	S76°13'37"E	0.19'
L18	S09°47'06"E	27.93'
L19	S27°54'46"E	10.06'
L20	S86°18'48"E	32.88'
L21	N71°32'29"E	7.35'
L22	N62°42'32"E	6.78'
L23	N36°34'00"E	6.97'
L24	N28°09'45"E	8.93'
L25	N29°56'02"E	3.90'
L26	N49°59'02"E	3.18'
L27	S45°44'42"E	4.54'
L28	S40°48'01"E	41.16'
L29	S19°27'49"E	2.55'
L30	S03°38'26"W	25.05'
L31	S03°17'33"E	27.67'
L32	S10°09'05"E	50.46'
L33	S17°30'55"E	75.17'
L34	S52°18'06"E	52.16'
L35	S76°30'44"E	46.54'

LINE TABLE		
LINE NO.	BEARING	DISTANCE
L36	S79°09'44"E	42.43'
L37	N87°16'56"E	59.08'
L38	N81°28'08"E	32.10'
L39	N76°06'09"E	27.02'
L40	N63°58'44"E	11.88'
L41	N53°00'07"E	8.01'
L42	N40°37'43"E	8.89'
L43	N45°10'21"E	23.89'
L44	N39°13'31"E	47.93'
L45	N49°51'04"E	55.72'
L46	N25°39'25"E	10.86'
L47	N42°57'02"E	8.26'
L48	N56°50'57"E	144.92'
L49	N56°05'38"E	52.78'
L50	N57°54'03"E	64.94'
L51	N65°43'36"E	61.75'
L52	N60°16'22"E	15.81'
L53	N60°10'41"E	46.39'
L54	N55°40'46"E	14.07'
L55	N45°32'56"E	23.47'
L56	N27°26'01"E	21.69'
L57	N57°29'53"E	86.34'
L58	N59°30'07"E	53.05'
L59	N59°38'18"E	80.21'
L60	N27°48'03"W	37.18'
L61	N87°08'47"W	13.73'
L62	N54°06'50"W	9.49'
L63	N28°30'03"W	28.36'
L64	N07°15'11"W	21.19'
L65	N15°25'58"E	10.53'
L66	N35°00'41"E	10.68'
L67	N18°04'05"E	8.33'
L68	N66°25'24"E	27.40'
L69	N57°39'08"E	16.90'
L70	S68°54'33"E	33.48'

LINE TABLE		
LINE NO.	BEARING	DISTANCE
L71	S77°16'49"E	7.64'
L72	S70°36'24"E	7.28'
L73	S06°26'47"E	8.60'
L74	S04°10'41"W	42.61'
L75	S28°15'56"W	21.11'
L76	S52°19'23"W	89.12'
L77	S82°13'50"W	85.83'
L78	N88°22'15"W	21.92'
L79	S81°30'05"W	20.47'
L80	S67°58'41"W	17.14'
L81	S56°26'46"W	25.66'
L82	S61°46'47"W	11.60'
L83	S61°28'44"W	10.01'
L84	S49°37'53"W	21.65'
L85	S52°44'56"W	32.98'
L86	S50°07'21"W	9.41'
L87	S52°47'59"W	4.88'
L88	S57°16'52"W	55.15'
L89	S61°00'14"W	16.25'
L90	S66°58'48"W	8.52'
L91	S56°33'56"W	8.17'
L92	S52°05'56"W	26.53'
L93	S46°51'26"W	23.89'
L94	S51°31'43"W	14.71'
L95	S51°24'48"W	165.74'
L96	S55°36'17"W	28.45'
L97	S39°16'17"W	64.49'
L98	S44°28'30"W	15.78'
L99	S35°13'38"W	22.71'
L100	S63°44'23"W	13.77'
L101	S57°36'26"W	14.96'
L102	S63°50'49"W	2.82'
L103	S44°16'59"W	9.90'
L104	S33°22'30"W	11.09'

WISCONSIN JESSE ZOLTOWSKI S-3094 LAND SURVEYOR

DRAFT

PREPARED BY:
PINNACLE ENGINEERING GROUP
20725 WATERTOWN ROAD | SUITE 100 |
BROOKFIELD, WI 53186
OFFICE: (262)754-8888

Jesse Zoltowski
SEPTEMBER 22, 2026

This instrument was drafted by Jesse Zoltowski, PLS-License No. S-3094

CERTIFIED SURVEY MAP NO. ____

Being all of Parcel 9 of Certified Survey Map No. 2273 in the Southwest 1/4 of the Northwest 1/4 of Section 27 and in the Southeast 1/4 of the Northeast 1/4 of Section 28, Township 1 North, Range 22 East, Village of Pleasant Prairie, Kenosha County, Wisconsin

LEGAL DESCRIPTION OF FLOODPLAIN

Being a part of Parcel 9 of CERTIFIED SURVEY MAP NO. 2273, as recorded in the Office of the Register of Deeds for Kenosha County as Document No. 1239083, in the Southwest 1/4 of the Northwest 1/4 of Section 27 and in the Southeast 1/4 of the Northeast 1/4 of Section 28, Township 1 North, Range 22 East, Village of Pleasant Prairie, Kenosha County, Wisconsin, described as follows:

Beginning at the southeast corner of the Northeast 1/4 of said Section 28; thence South 89°55'24" West along the south line of said Northeast 1/4, 231.13 feet; thence North 7°51'47" West, 1.32 feet; thence North 13°21'43" West, 33.01 feet; thence North 24°41'24" West, 5.43 feet; thence North 31°22'22" West, 11.30 feet; thence North 27°01'22" West, 5.29 feet; thence North 18°10'54" West, 41.24 feet; thence North 25°10'14" West, 20.62 feet; thence North 20°41'44" West, 29.63 feet; thence North 16°49'52" West, 17.34 feet; thence North 0°27'27" East, 14.75 feet; thence North 22°44'22" East, 23.00 feet; thence North 27°24'14" East, 32.98 feet; thence North 32°56'12" East, 29.20 feet; thence North 14°05'52" East, 25.69 feet; thence North 9°45'08" East, 27.90 feet; thence North 88°06'07" East, 8.22 feet; thence South 76°13'37" East, 0.19 feet; thence South 9°47'06" East, 27.93 feet; thence South 27°54'46" East, 10.06 feet; thence South 86°18'48" East, 32.88 feet; thence North 71°32'29" East, 7.35 feet; thence North 62°42'32" East, 6.78 feet; thence North 36°34'00" East, 6.97 feet; thence North 28°09'45" East, 8.93 feet; thence North 29°56'02" East, 3.90 feet; thence North 49°59'02" East, 3.18 feet; thence South 45°44'42" East, 4.54 feet; thence South 40°48'01" East, 41.16 feet; thence South 19°27'49" East, 2.55 feet; thence South 3°38'26" West, 25.05 feet; thence South 3°17'33" East, 27.67 feet; thence South 10°09'05" East, 50.46 feet; thence South 17°30'55" East, 75.17 feet; thence South 52°18'06" East, 52.16 feet; thence South 76°30'44" East, 46.54 feet; thence South 79°09'44" East, 42.43 feet; thence North 87°16'56" East, 59.08 feet; thence North 81°28'08" East, 32.10 feet; thence North 76°06'09" East, 27.02 feet; thence North 63°58'44" East, 11.88 feet; thence North 53°00'07" East, 8.01 feet; thence North 40°37'43" East, 8.89 feet; thence North 45°10'21" East, 23.89 feet; thence North 39°13'31" East, 47.93 feet; thence North 49°51'04" East, 55.72 feet; thence North 25°39'25" East, 10.86 feet; thence North 42°57'02" East, 8.26 feet; thence North 56°50'57" East, 144.92 feet; thence North 56°05'38" East, 52.78 feet; thence North 57°54'03" East, 64.94 feet; thence North 65°43'36" East, 61.75 feet; thence North 60°16'22" East, 15.81 feet; thence North 60°10'41" East, 46.39 feet; thence North 55°40'46" East, 14.07 feet; thence North 45°32'56" East, 23.47 feet; thence North 27°26'01" East, 21.69 feet; thence North 57°29'53" East, 86.34 feet; thence North 59°30'07" East, 53.05 feet; thence North 59°38'18" East, 80.21 feet; thence North 27°48'03" West, 37.18 feet; thence North 87°08'47" West, 13.73 feet; thence North 54°06'50" West, 9.49 feet; thence North 28°30'03" West, 28.36 feet; thence North 7°15'11" West, 21.19 feet; thence North 15°25'58" East, 10.53 feet; thence North 35°00'41" East, 10.68 feet; thence North 18°04'05" East, 8.33 feet; thence North 66°25'24" East, 27.40 feet; thence North 57°39'08" East, 16.90 feet; thence South 68°54'33" East, 33.48 feet; thence South 77°16'49" East, 7.64 feet; thence South 70°36'24" East, 7.28 feet to a point on a curve, also being the southwest right of way line of State Trunk Highway "31"; thence southeasterly 115.90 feet along the arc of said curve to the right, whose radius is 1829.86 feet, whose chord bears South 31°53'45" East, 115.89 feet; thence South 6°26'47" East, 8.60 feet; thence South 4°10'41" West, 42.61 feet; thence South 28°15'56" West, 21.11 feet; thence South 52°19'23" West, 89.12 feet; thence South 82°13'50" West, 85.83 feet; thence North 88°22'15" West, 21.92 feet; thence South 81°30'05" West, 20.47 feet; thence South 67°58'41" West, 17.14 feet; thence South 56°26'46" West, 25.66 feet; thence South 61°46'47" West, 11.60 feet; thence South 61°28'44" West, 10.01 feet; thence South 49°37'53" West, 21.65 feet; thence South 52°44'56" West, 32.98 feet; thence South 50°07'21" West, 9.41 feet; thence South 52°47'59" West, 4.88 feet; thence South 57°16'52" West, 55.15 feet; thence South 61°00'14" West, 16.25 feet; thence South 66°58'48" West, 8.52 feet; thence South 56°33'56" West, 8.17 feet; thence South 52°05'56" West, 26.53 feet; thence South 46°51'26" West, 23.89 feet; thence South 51°31'43" West, 14.71 feet; thence South 51°24'48" West, 165.74 feet; thence South 55°36'17" West, 28.45 feet; thence South 39°16'17" West, 64.49 feet; thence South 44°28'30" West, 15.78 feet; thence South 35°13'38" West, 22.71 feet; thence South 63°44'23" West, 13.77 feet; thence South 57°36'26" West, 14.96 feet; thence South 63°50'49" West, 2.82 feet; thence South 44°16'59" West, 9.90 feet; thence South 33°22'30" West, 11.09 feet to the south line of the Northwest 1/4 of said Section 27; thence South 89°28'52" West along said south line, 227.13 feet to the Point of Beginning.



SEPTEMBER 22, 2026

PREPARED BY:
PINNACLE ENGINEERING GROUP
20725 WATERTOWN ROAD | SUITE 100 |
BROOKFIELD, WI 53186
OFFICE: (262)754-8888

This instrument was drafted by Jesse Zoltowski, PLS-License No. S-3094

CERTIFIED SURVEY MAP NO. ____

Being all of Parcel 9 of Certified Survey Map No. 2273 in the Southwest 1/4 of the Northwest 1/4 of Section 27 and in the Southeast 1/4 of the Northeast 1/4 of Section 28, Township 1 North, Range 22 East, Village of Pleasant Prairie, Kenosha County, Wisconsin

SURVEYOR'S CERTIFICATE

STATE OF WISCONSIN)
WAUKESHA COUNTY) SS

I, Jesse Zoltowski, Professional Land Surveyor, do hereby certify:

That I have surveyed and mapped Parcel Nine (9) of CERTIFIED SURVEY MAP NO. 2273, located in the Southwest One-quarter (1/4) of the Northwest One-quarter (1/4) of Section Twenty-seven (27) and in the Southeast One-quarter (1/4) of the Northeast One-quarter (1/4) of Section Twenty-eight (28), Township One (1) North, Range Twenty-two (22) East, Village of Pleasant Prairie, Kenosha County, Wisconsin, recorded in the Office of the Register of Deeds for Kenosha County on October 18, 2001 as Document No. 1239083.

Dedicating that portion of the subject property as graphically shown for public right of way purposes.

Containing 995,256 Square Feet (22.8479 Acres) Gross and 993,833 Square Feet (22.8152 Acres) of land Net, more or less.

That I have made such survey, land division and map by the direction of TI INVESTORS OF LAKEVIEW NITTO PARCEL LLC, owner of said land.

That such map is a correct representation of all the exterior boundaries of the land surveyed and the land division thereof made.

That I have fully complied with the requirements of Chapter 236 of the Wisconsin State Statutes and the Village of Pleasant Prairie Land Division and Development Control Ordinance in surveying, mapping and dividing the land within the certified survey map.

Date: SEPTEMBER 22, 2026



Jesse Zoltowski
Professional Land Surveyor S-3094

CURVE TABLE							
CURVE NO.	LENGTH	RADIUS	DELTA	CHORD BEARING	CHORD LENGTH	TANGENT	TANGENT
C1	137.73'	335.00'	023°33'21"	N85°30'32"E	136.76'	S82°42'48"E	N73° 43' 51"E
C2	32.23'	115.00'	016°03'34"	S81°45'38"W	32.13'	S89°47'25"W	S73° 43' 51"W
C3	109.94'	185.00'	034°03'01"	N72°45'54"E	108.33'	N89°47'25"E	N55° 44' 24"E
C4	709.89'	1829.86'	022°13'40"	N23°35'15"W	705.45'	N12°28'26"W	N34° 42' 05"W
C5	58.87'	185.00'	018°14'03"	N80°40'23"E	58.63'	N89°47'25"E	N71° 33' 22"E
C6	51.07'	185.00'	015°48'58"	N63°38'53"E	50.91'	N71°33'22"E	N55° 44' 24"E
C7	53.00'	192.00'	015°48'58"	S63°38'53"W	52.83'	S71°33'22"W	S55° 44' 24"W

PREPARED BY:
PINNACLE ENGINEERING GROUP
20725 WATERTOWN ROAD | SUITE 100 |
BROOKFIELD, WI 53186
OFFICE: (262)754-8888

This instrument was drafted by Jesse Zoltowski, PLS-License No. S-3094

CERTIFIED SURVEY MAP NO. ____

Being all of Parcel 9 of Certified Survey Map No. 2273 in the Southwest 1/4 of the Northwest 1/4 of Section 27 and in the Southeast 1/4 of the Northeast 1/4 of Section 28, Township 1 North, Range 22 East, Village of Pleasant Prairie, Kenosha County, Wisconsin

OWNER'S CERTIFICATE OF DEDICATION

TI INVESTORS OF LAKEVIEW NITTO PARCEL LLC, a Limited Liability Company duly organized and existing under and by virtue of the laws of the State of Wisconsin, as owner, does hereby certify that said limited liability company caused the land described on this certified survey map to be surveyed, mapped and dedicated as represented on this certified survey map.

TI INVESTORS OF LAKEVIEW NITTO PARCEL LLC, as owner, does further certify that this certified survey map is required by Chapter 236 of the Wisconsin State Statutes to be submitted to the following for approval:

1. Village of Pleasant Prairie

IN WITNESS WHEREOF, the said _____ has caused these presents to be signed by (name - print) _____, (title) _____, at (city)_____, _____ County, Wisconsin, on this _____ day of _____ , 2026.

In the presence of: TI INVESTORS OF LAKEVIEW NITTO PARCEL LLC

_____
Name (signature) - Title

STATE OF WISCONSIN)
_____ COUNTY) SS

Personally came before me this _____ day of _____ , 2026, (name) _____, (title) _____, of the above named limited liability company, to me known to be the person who executed the foregoing instrument, and to me known to be such _____title) of said limited liability company, and acknowledged that they executed the foregoing instrument as such officer as the deed of said limited liability, by its authority.

_____
Notary Public
Name:_____
State of Wisconsin
My Commission Expires: _____

CONSENT OF CORPORATE MORTGAGEE

_____ , a corporation duly organized and existing under and by virtue of the laws of the State of Wisconsin, mortgagee of the above described land, does hereby consent to the surveying, mapping and dedication of the land described in the forgoing affidavit of Jesse Zoltowski, surveyor, and does hereby consent to the above certification of owners.

IN WITNESS WHEREOF, the said _____ , has caused these presents to be signed by _____ , its _____, and its corporate seal to be hereunto affixed this _____ day of _____ , 2026.

_____ _____
Date Name - Title

STATE OF WISCONSIN)
_____ COUNTY) SS

Personally came before me this _____ day of _____ , 2026, _____ , to me known to be the person who executed the foregoing instrument and to me known to be such officer of said corporation and acknowledged the same.

_____
Notary Public
Name:_____
State of Wisconsin
My Commission Expires: _____

WISCONSIN
JESSE
ZOLTOWSKI
S-3094
LAND SURVEYOR
DRAFT

Jesse Zoltowski
SEPTEMBER 22, 2026

PREPARED BY:
PINNACLE ENGINEERING GROUP
20725 WATERTOWN ROAD | SUITE 100 |
BROOKFIELD, WI 53186
OFFICE: (262)754-8888

This instrument was drafted by Jesse Zoltowski, PLS-License No. S-3094

CERTIFIED SURVEY MAP NO. ____

Being all of Parcel 9 of Certified Survey Map No. 2273 in the Southwest 1/4 of the Northwest 1/4 of Section 27 and in the Southeast 1/4 of the Northeast 1/4 of Section 28, Township 1 North, Range 22 East, Village of Pleasant Prairie, Kenosha County, Wisconsin

PLAN COMMISSION APPROVAL

Approved by the Plan Commission of the Village of Pleasant Prairie on this _____ day of _____ , 2026.

_____
Michael R. Pollocoff, Chairman

VILLAGE BOARD APPROVAL

Approved by the Village Board of the Village of Pleasant Prairie, Wisconsin, on this _____ day of _____ , 2026.

_____
David J. Klimisch, Village President

_____
Jane C. Snell, Village Clerk



SEPTEMBER 22, 2026

PREPARED BY:
PINNACLE ENGINEERING GROUP
20725 WATERTOWN ROAD | SUITE 100 |
BROOKFIELD, WI 53186
OFFICE: (262)754-8888

This instrument was drafted by Jesse Zoltowski, PLS-License No. S-3094

CERTIFIED SURVEY MAP NO. ____

Being all of Parcel 9 of Certified Survey Map No. 2273 in the Southwest 1/4 of the Northwest 1/4 of Section 27 and in the Southeast 1/4 of the Northeast 1/4 of Section 28, Township 1 North, Range 22 East, Village of Pleasant Prairie, Kenosha County, Wisconsin

The following "Dedication of Easement Provisions" and "Restrictive Covenants" were drafted by the Village of Pleasant Prairie and is shown here on as a condition of map approval. Inclusion thereof on this document is not to be considered practicing law in the State of Wisconsin by the above signed Land Surveyor, the Land Surveyor is not responsible for rights granted, perceived or otherwise stated herein.

TI Investors of Lakeveiw Nitto Parcel LLC (hereinafter referred to as the "Owner"), hereby dedicates to the Village of Pleasant Prairie (the "Village") and other parties as identified herein, the following fee simple interests and easements, in the locations shown on this Certified Survey Map and provides for certain restrictive covenants benefiting the Village and other parties as provided herein.

The term "Lot Owner" means the Owner while holding ownership of applicable property and, after sale by the Owner, the owner or owners of individual lots within the property included in the CSM (including any Outlots, if applicable), their successors, assigns and successors-in-title in their capacity as Lot Owners. All restrictive covenants and dedication and easement conditions and requirements herein shall run with the land, shall be binding upon all Lot Owners, and shall benefit and be enforceable by the Village and other parties as provided herein. As used in herein, the term "Village" includes the Village and its successors and assigns.

1. The fee ownership interest in the areas shown on the CSM as Dedicated Public Street are hereby dedicated, given, granted and conveyed by the Owner to the public for street purposes and related public purposes and for other purposes in the sole discretion of the Village.
2. A perpetual easement interest in each area shown on the CSM as Dedicated Private Stormwater Easement is hereby dedicated, given, granted, reserved and conveyed by the Owner to the Village for stormwater management purposes. The Owner shall record a Stormwater Maintenance Agreement pursuant to Section 289-9 of the Village Code of Ordinances for all Dedicated Private Stormwater Easement Areas.
3. A perpetual easement interest in each area shown on the CSM as Dedicated Public Utility Easement is hereby dedicated, given, granted, reserved and conveyed by the Owner to the Village for public and private utility, stormwater management, and telecommunications purposes and for all related construction, installation, repair, alteration, replacement, landscaping, maintenance, and ingress and egress.
4. The Owner hereby covenants that the Owner and Lot Owners shall not dedicate or convey an easement to any party in any part of the area of an easement dedicated to the Village pursuant to this CSM without approval by the Village.
5. The Owner hereby covenants that use by a Lot Owner of an easement area dedicated to the Village pursuant to this CSM shall not interfere with the Village's rights under the easement dedicated to the Village, that a Lot Owner may not alter the grade elevation of any part of an easement area dedicated to the Village, and that no structure, fence, landscaping, trees or other obstruction to the free and full access of each easement area by the Village shall be installed, constructed, or maintained by a Lot Owner unless approved in writing by the Village. If the Village approves of any structure, fence, landscaping, or other obstruction in an easement area the Village shall not be responsible for any damage to or replacement of same.
6. The Owner hereby covenants that each Lot Owner shall have the obligation, at the Lot Owner's cost, of maintaining each easement area dedicated to the Village pursuant to the CSM in a functional, neat, and nuisance-free condition, including mowing and the removal of trash, debris, leaves, and brush.
7. The Owner hereby covenants that, to the extent applicable to a particular easement area dedicated to the Village pursuant to the CSM, each Lot Owner, at the Lot Owner's cost, shall maintaining erosion control methods to protect any present drainageways, shall perform ditching, dredging, or cleaning to re-establish stormwater management design capacities, shall clean, repair and replace any private inlets, private outlets, private piping, private manholes and private catch basin structures, and shall perform any other maintenance required to prevent nuisance conditions.
8. The Owner hereby covenants for the Owner and the Lot Owners that areas within the property described in the CSM that are wetlands subject to Village, state and/or federal wetlands requirements and areas that are subject to floodplain zoning regulations under federal, state, or Village laws and ordinances, will be managed consistent with these wetland and floodplain requirements and be preserved, protected, and maintained in functional, neat, and nuisance-free condition.
9. The Village shall have the right, but not the obligation, to perform any obligations of a Lot Owner under the dedications and covenants herein, if the Lot Owner fails to comply with these obligations, and the Lot Owner shall be liable for any costs which may be incurred by the Village. The Village may recover such costs from such Lot Owner as special assessments or special charges under Section 66.0627 (or successors or similar provisions) of the Wisconsin Statutes or otherwise according to law.



SEPTEMBER 22, 2026

PREPARED BY:
PINNACLE ENGINEERING GROUP
20725 WATERTOWN ROAD | SUITE 100 |
BROOKFIELD, WI 53186
OFFICE: (262)754-8888

This instrument was drafted by Jesse Zoltowski, PLS-License No. S-3094