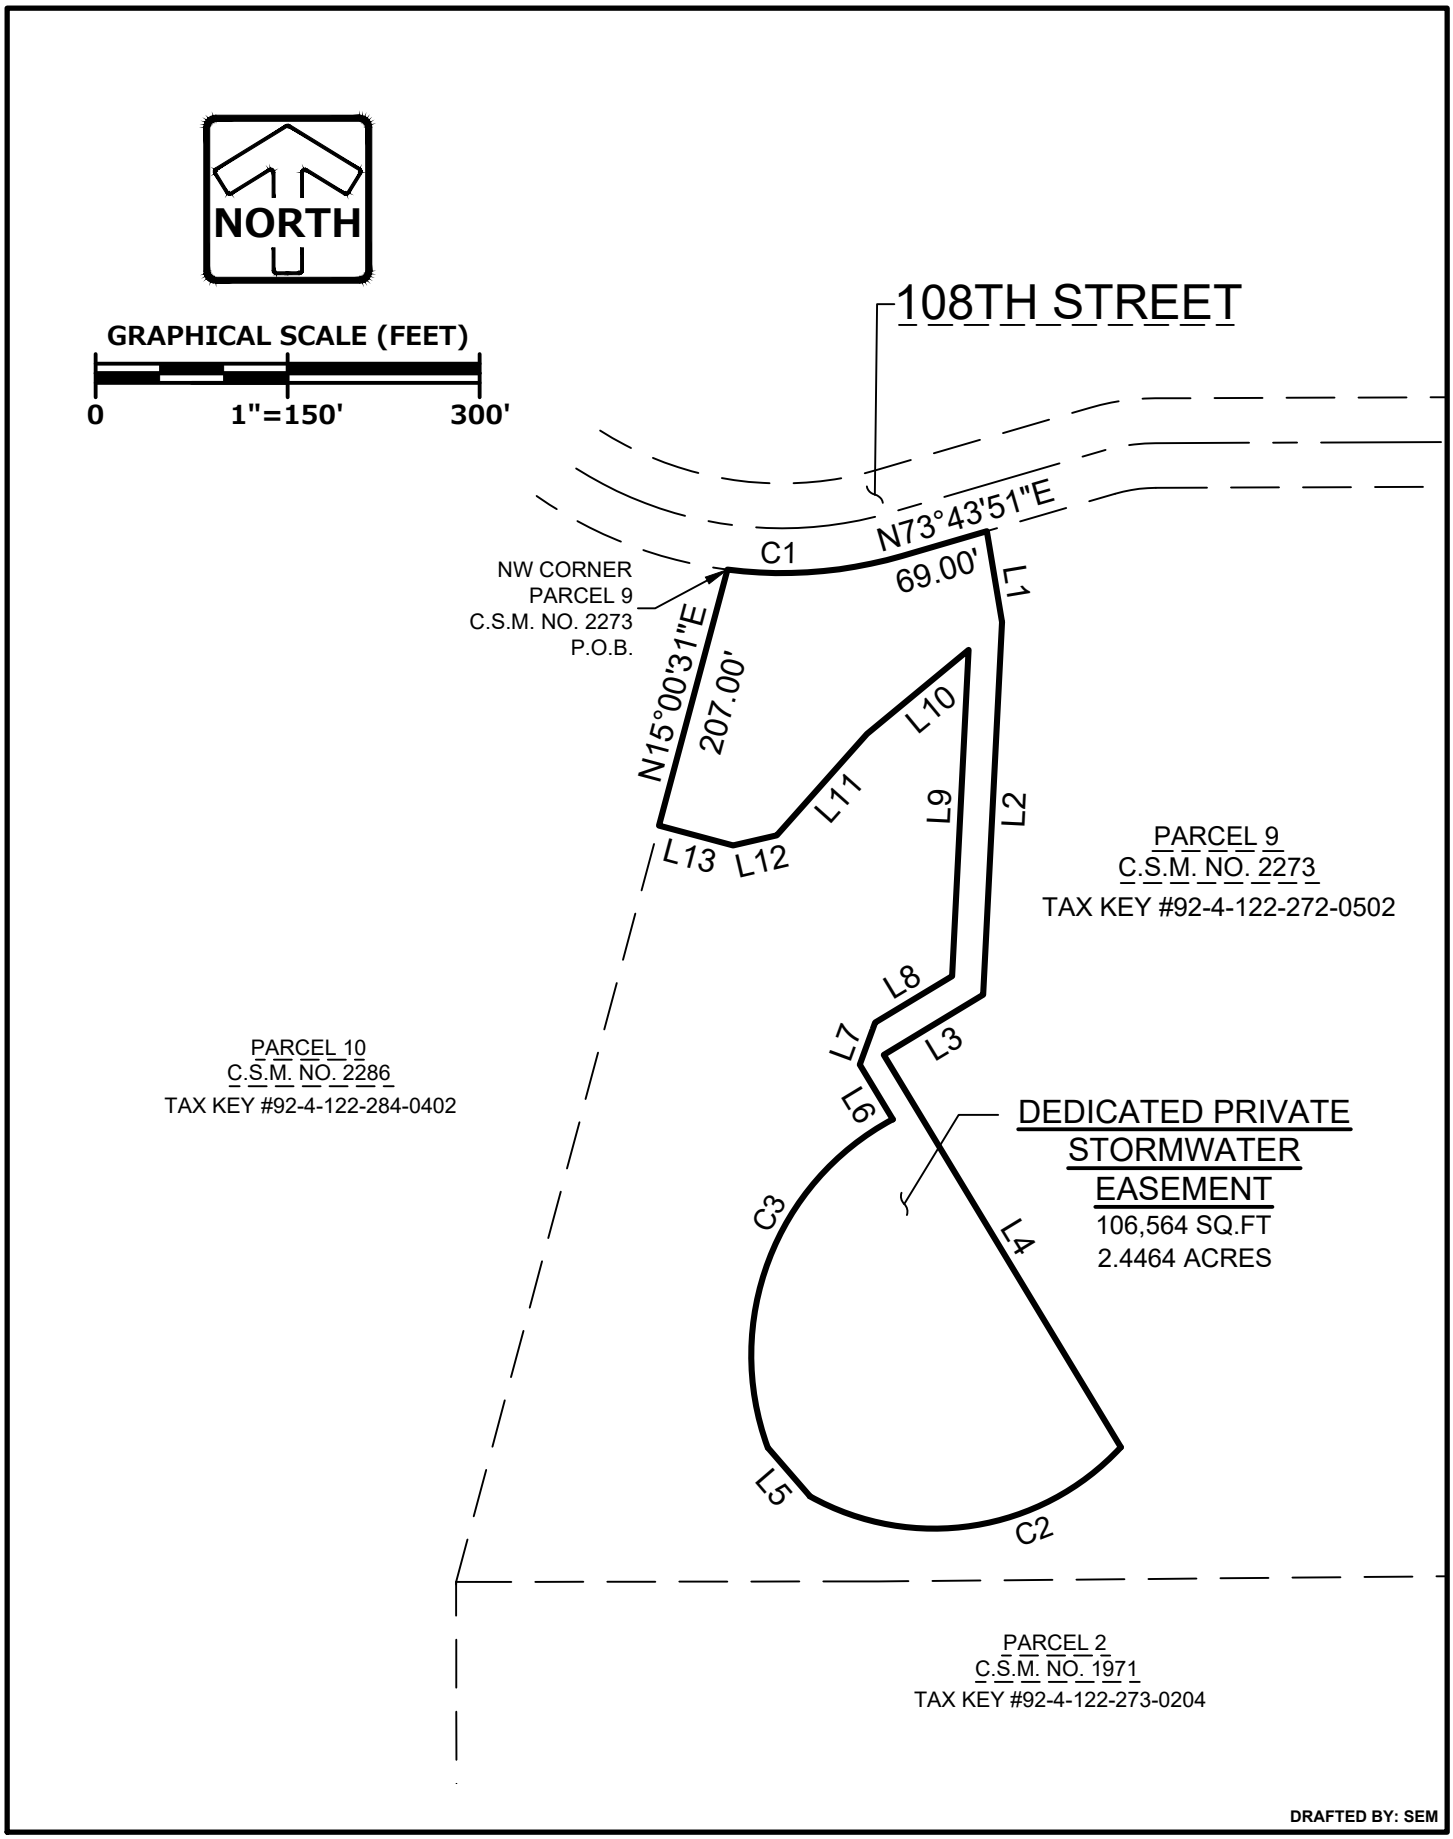


Z:\PROJECTS\2016\644.00-WI\SURVEY\CAD\644.00 EXHIBIT STORM.DWG

DRAFTED BY: SEM

EXHIBIT

SHEET 1 OF 2

10/7/2026

PINNACLE ENGINEERING GROUP PLAN | DESIGN | DELIVER
20725 WATERTOWN ROAD | SUITE 100 | BROOKFIELD, WI 53186 WWW.PINNACLE-ENGR.COM

PEG JOB#644.00

LEGAL DESCRIPTION:

Being a part of Parcel 9 of Certified Survey Map No. 2273, recorded in the Office of the Register of Deeds for Kenosha County on October 18, 2001 as Document No. 1239083, located in the Southwest 1/4 of the Northwest 1/4 of Section 27 and in the Southeast 1/4 of the Northeast 1/4 of Section 28, all in Township 1 North, Range 22 East, Village of Pleasant Prairie, Kenosha County, Wisconsin, described as:

Beginning at the northwest corner of said Parcel 9, and a point on a curve; thence northeasterly 137.73 feet along the arc of said curve to the left and the south right-of-way line of 108th Street, whose radius is 335.00 feet and whose chord bears North 85°30'32" East 136.76 feet; thence North 73°43'51" East along said south right-of-way line, 69.00 feet; thence South 09°27'18" East, 72.00 feet; thence South 02°53'44" West, 291.48 feet; thence South 58°51'09" West, 90.77 feet; thence South 31°08'51" East, 358.20 feet to a point on a curve; thence southwesterly 265.16 feet along the arc of said curve to the right, whose radius is 199.00 feet and whose chord bears South 81°03'55" West, 245.97 feet; thence North 40°51'53" West, 50.00 feet to a point on a curve; thence northeasterly 299.33 feet along the arc of said curve to the right, whose radius is 209.00 feet and whose chord bears North 20°49'48" East, 274.39 feet; thence North 31°08'51" West, 50.00 feet; thence North 20°05'45" East, 35.00 feet; thence North 58°51'09" East, 70.20 feet; thence North 02°53'44" East, 255.20 feet; thence South 50°23'11" West, 103.00 feet; thence South 41°41'09" West, 106.00 feet; thence South 76°52'14" West, 35.00 feet; thence North 74°59'29" West, 60.00 feet to the west line of said Parcel 9 of Certified Survey Map No. 2273; thence North 15°00'31" East along said west line 207.00 feet to the Point of Beginning.

Said easement contains 106,564 square feet (2.4464 Acres), more or less.

LINE TABLE		
LINE NO.	BEARING	DISTANCE
L1	S09°27'18"E	72.00'
L2	S02°53'44"W	291.48'
L3	S58°51'09"W	90.77'
L4	S31°08'51"E	358.20'
L5	N40°51'53"W	50.00'
L6	N31°08'51"W	50.00'
L7	N20°05'45"E	35.00'
L8	N58°51'09"E	70.20'
L9	N02°53'44"E	255.20'
L10	S50°23'11"W	103.00'
L11	S41°41'09"W	106.00'
L12	S76°52'14"W	35.00'
L13	N74°59'29"W	60.00'

CURVE TABLE				
CURVE NO.	LENGTH	RADIUS	CHORD BEARING	CHORD LENGTH
C1	137.73'	335.00'	N85°30'32"E	136.76'
C2	265.16'	199.00'	S81°03'55"W	245.97'
C3	299.33'	209.00'	N20°49'48"E	274.39'

Z:\PROJECTS\2016\644.00-WI\SURVEY\CAD\644.00 EXHIBIT STORM.DWG

DRAFTED BY: SEM

PINNACLE ENGINEERING GROUP PLAN | DESIGN | DELIVER
20725 WATERTOWN ROAD | SUITE 100 | BROOKFIELD, WI 53186 WWW.PINNACLE-ENGR.COM PEG JOB#644.00