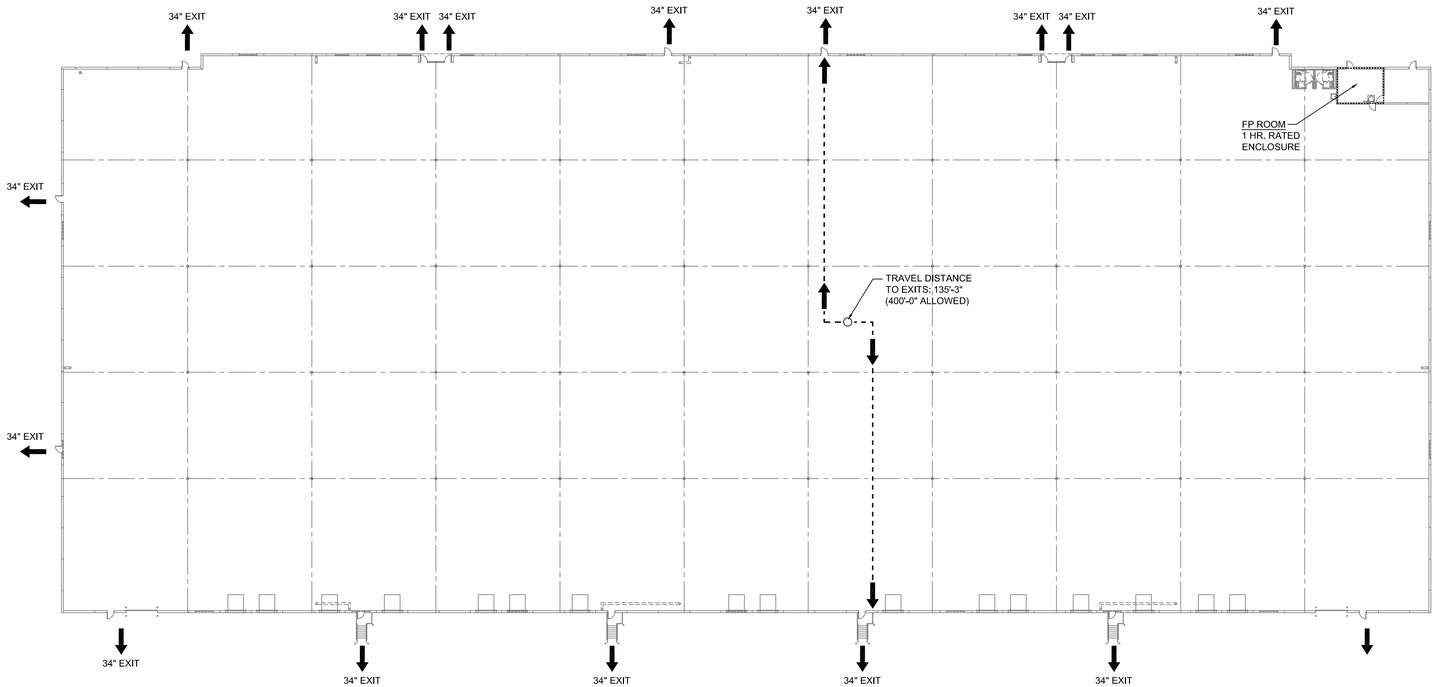


1 / A0.1 FIRST FLOOR PLAN
1/32" = 1'-0"

TRUE NORTH

PLAN NORTH

APPLICABLE CODES:

BUILDING CODE: INTERNATIONAL BUILDING CODE - 2021 AS MODIFIED BY THE WISCONSIN ENROLLED COMMERCIAL BUILDING CODE IN CHAPTER SPS 362.

CHAPTER 3 - USE AND OCCUPANCY CLASSIFICATION

THIS BUILDING WILL BE CLASSIFIED AS A FULLY SPRINKLERED, NON-SEPARATED 'S-1', 'F-1' & 'B' USE. DEPENDING ON USE WHEN FUTURE OCCUPANCY IS DETERMINED, IT WILL INCORPORATE NON-SEPARATED USES PER SECTION 508.3.1 INCLUDING BUSINESS OFFICES WHICH ARE CLASSIFIED AS BUSINESS 'B' USE GROUP. THE BUILDING WILL BE CURRENTLY CLASSIFIED AS 'F-1' - THE MOST RESTRICTIVE OCCUPANCY.

CHAPTER 5 - GENERAL BUILDING HEIGHTS AND AREAS

THE BUILDING IS CONSTRUCTED WITH UNPROTECTED STEEL COLUMNS, JOISTS, BEAMS, AND ROOF DECK, THEREFORE THE CONSTRUCTION CLASSIFICATION FOR THE BUILDING IS TYPE II-B. THE BUILDING IS FULLY SPRINKLERED.

TABLE 504.3 'ALLOWABLE BUILDING HEIGHT IN FEET ABOVE GRADE PLANE'
OCCUPANCY GROUPS S-1, F-1, B FOR CONSTRUCTION TYPE IIB: 75'-0"

TABLE 506 'ALLOWABLE AREA FACTOR IN SQUARE FEET'

OCCUPANCY GROUP S-1: 70,000 SF MAXIMUM FOR SINGLE STORY SPRINKLERED BUILDING.
OCCUPANCY GROUP F-1: 62,000 SF MAXIMUM FOR SINGLE STORY SPRINKLERED BUILDING.
OCCUPANCY GROUP B: 92,000 SF MAXIMUM FOR SINGLE STORY SPRINKLERED BUILDING.

ACTUAL BUILDING: 39'-2" HIGH
SINGLE STORY
152,334 SF

SECTION 507.4 'SPRINKLERED, ONE-STORY BUILDINGS'

THE AREA OF A GROUP A-4 BUILDING NO MORE THAN ONE STORY ABOVE GRADE PLANE OF OTHER THAN TYPE V CONSTRUCTION, OR THE AREA OF A GROUP B, F, M OR S BUILDING NOT MORE THAN ONE STORY ABOVE GRADE PLANE OF ANY CONSTRUCTION TYPE, SHALL NOT BE LIMITED WHERE THE BUILDING IS PROVIDED WITH AN AUTOMATIC SPRINKLER SYSTEM THROUGHOUT IN ACCORDANCE WITH SECTION 903.3.1.1 AND IS SURROUNDED AND ADJOINED BY PUBLIC WAYS OR YARDS NOT LESS THAN 60 FEET IN WIDTH.

THIS BUILDING QUALIFIES AS AN UNLIMITED AREA BUILDING.

CHAPTER 6 - TYPES OF CONSTRUCTION

SECTION 602.2 'TYPES I AND II'
TYPES I AND II CONSTRUCTION ARE THOSE TYPES OF CONSTRUCTION IN WHICH THE BUILDING ELEMENTS SPECIFIED IN TABLE 601 ARE OF NONCOMBUSTIBLE MATERIALS, EXCEPT AS PERMITTED IN SECTION 603 AND ELSEWHERE IN THIS CODE.

TABLE 601 'FIRE-RESISTANCE RATING REQUIREMENTS FOR BUILDING ELEMENTS (HOURS)'

BUILDING ELEMENTS		
PRIMARY STRUCTURAL FRAME	INCLUDING COLUMNS, GIRDERS, TRUSSES	0 HOURS / NONCOMBUSTIBLE
BEARING WALLS	EXTERIOR (>30')	0 HOURS / NONCOMBUSTIBLE
	INTERIOR	0 HOURS / NONCOMBUSTIBLE
NONBEARING WALLS AND PARTITIONS	EXTERIOR (>30')	0 HOURS / NONCOMBUSTIBLE
	INTERIOR	0 HOURS / NONCOMBUSTIBLE
FLOOR CONSTRUCTION AND ASSOCIATED SECONDARY STRUCTURAL MEMBERS	INCLUDING SUPPORTING BEAMS AND JOIST	0 HOURS / NONCOMBUSTIBLE
ROOF CONSTRUCTION AND ASSOCIATED SECONDARY STRUCTURAL MEMBERS	INCLUDING SUPPORTING BEAMS AND JOIST	0 HOURS / NONCOMBUSTIBLE

THIS BUILDING IS CLASSIFIED AS TYPE II-B.

CHAPTER 7 - FIRE AND SMOKE PROTECTION FEATURES

TABLE 716.2 "OPENING FIRE PROTECTION ASSEMBLIES, RATINGS AND MARKINGS"
OTHER FIRE BARRIERS REQUIRE A 45 MINUTE DOOR RATING.

A 45 MINUTE RATED DOOR IS PROVIDED AT THE FIRE PROTECTION ROOM.

CHAPTER 8 - INTERIOR FINISHES

SECTION 803.1.1 'INTERIOR WALL AND CEILING FINISH MATERIALS TESTED IN ACCORDANCE WITH NFPA 286'
INTERIOR WALL AND CEILING FINISHES SHALL BE CLASSIFIED IN ACCORDANCE WITH NFPA 286 AND COMPLY WITH SECTION 803.1.1.1. MATERIALS COMPLYING WITH SECTION 803.1.1.1 SHALL BE CONSIDERED TO ALSO COMPLY WITH THE REQUIREMENTS OF CLASS A.

SECTION 803.1.1.1 'ACCEPTANCE CRITERIA FOR NFPA 286'
THE INTERIOR FINISH SHALL COMPLY WITH THE FOLLOWING:
1. DURING THE 40KW EXPOSURE, FLAMES SHALL NOT SPREAD TO THE CEILING.
2. THE FLAME SHALL NOT SPREAD TO THE OUTER EXTREMITY OF THE SAMPLE ON ANY WALL OR CEILING.
3. FLASHOVER, AS DEFINED IN NFPA 286, SHALL NOT OCCUR.
4. THE PEAK HEAT RELEASE RATE THROUGHOUT THE TEST SHALL NOT EXCEED 800 KW.
5. THE TOTAL SMOKE RELEASED THROUGHOUT THE TEST SHALL NOT EXCEED 1,000 SM.

CLASS A: FLAME SPREAD 0 - 25, SMOKED DEVELOPED 0 - 450
CLASS B: FLAME SPREAD 26 - 75, SMOKED DEVELOPED 0 - 450
CLASS C: FLAME SPREAD 76 - 200, SMOKED DEVELOPED 0 - 450

SECTION 803.13' INTERIOR FINISH REQUIREMENTS BASED ON OCCUPANCY'
INTERIOR WALL AND CEILING FINISH SHALL HAVE A FLAME SPREAD RATING NOT GREATER THAN THAT SPECIFIED IN TABLE 803.13 FOR THE GROUP AND LOCATION DESIGNATED. INTERIOR WALL AND CEILING FINISH MATERIALS TESTED IN ACCORDANCE WITH NFPA 286 AND MEETING THE ACCEPTANCE CRITERIA OF SECTION 803.1.1.1, SHALL BE PERMITTED TO BE USED WHERE A CLASS A CLASSIFICATION IN ACCORDANCE WITH ASTM E 84 OR UL 723 IS REQUIRED.

TABLE 803.13 REQUIRES THE FOLLOWING IN A SPRINKLERED BUILDING.
INTERIOR EXIT STAIRWAYS AND RAMPS AND EXIT PASSAGEWAYS - B
CORRIDORS AND ENCLOSURE FOR EXIT ACCESS STAIRWAYS AND RAMPS - B
ROOMS AND ENCLOSED SPACES - C

SECTION 803.14 'STABILITY'
INTERIOR FINISH MATERIALS REGULATED BY THIS CHAPTER SHALL BE APPLIED OR FASTENED IN SUCH A MANNER THAT THE MATERIALS WILL NOT READILY BECOME DETACHED WHERE SUBJECTED TO ROOM TEMPERATURES OF 200 DEGREES FAHRENHEIT FOR NOT LESS THAN 30 MINUTES.

SECTION 803.15.4 'MATERIALS'
AN INTERIOR WALL OR CEILING FINISH THAT ARE IS MORE THAN 0.25 INCH THICK SHALL BE APPLIED DIRECTLY TO ONTO THE WALL, CEILING OR STRUCTURAL ELEMENT WITHOUT THE USE OF FURRING STRIPS AND SHALL NOT BE SUSPENDED AWAY FROM THE BUILDING ELEMENT TO WHICH THAT FINISH MATERIAL IT IS APPLIED.

SECTION 803.1.2 'INTERIOR WALL AND CEILING FINISH MATERIALS TESTED IN ACCORDANCE WITH ASTM E-84 OR UL 723'
INTERIOR WALL AND CEILING FINISHES SHALL BE CLASSIFIED IN ACCORDANCE WITH ASTM E-84 OR UL 723. SUCH INTERIOR FINISH MATERIALS SHALL BE GROUPED IN THE FOLLOWING CLASSES IN ACCORDANCE WITH THEIR FLAME SPREAD AND SMOKE-DEVELOPED INDICES.

SECTION 804.4.2 - MINIMUM CRITICAL RADIANT FLUX.
EXCEPTION: WHERE A BUILDING IS EQUIPPED THROUGHOUT WITH AN AUTOMATIC SPRINKLER SYSTEM IN ACCORDANCE WITH SECTION 903.1.1 OR 903.3.1.2, CLASS II MATERIALS ARE PERMITTED IN ANY AREA WHERE CLASS I MATERIALS ARE REQUIRED, AND MATERIALS COMPLYING WITH DOC FF-1 "PILL TEST" (CPSC 16 CFR PART 1630) OR WITH ASTM D2859 ARE PERMITTED IN ANY AREA WHERE CLASS II MATERIALS ARE REQUIRED.

CHAPTER 9 - FIRE PROTECTION SYSTEMS

THIS BUILDING IS FULLY SPRINKLERED IN ACCORDANCE WITH SECTION 903.

CHAPTER 10 - MEANS OF EGRESS

SECTION 1004: 'OCCUPANT LOAD'
TABLE 1004.5 'MAXIMUM FLOOR AREA ALLOWANCES PER OCCUPANT'
WAREHOUSE AREA = 500 GROSS
152,334 GROSS SF (1 OCCUPANT / 500 GROSS) = 305 OCCUPANTS

SECTION 1005: 'MEANS OF EGRESS SIZING'
TABLE 1005.3.2 'OTHER EGRESS COMPONENTS'
THE CAPACITY, IN INCHES, OF MEANS OF EGRESS COMPONENTS OTHER THAN STAIRWAYS SHALL BE CALCULATED BY MULTIPLYING THE OCCUPANT LOAD SERVED BY SUCH COMPONENT BY A MEANS OF EGRESS CAPACITY FACTOR OF 0.2 INCH PER OCCUPANT.
EXCEPTION 1: FOR OTHER THAN GROUP H AND I-2 OCCUPANCIES, THE CAPACITY, IN INCHES, OF MEANS OF EGRESS COMPONENTS OTHER THAN STAIRWAYS SHALL BE CALCULATED BY MULTIPLYING THE OCCUPANT LOAD SERVED BY SUCH COMPONENT BY A MEANS OF EGRESS CAPACITY FACTOR OF 0.15 INCH PER OCCUPANT IN BUILDINGS EQUIPPED THROUGHOUT WITH AN AUTOMATIC SPRINKLER SYSTEM INSTALLED IN ACCORDANCE WITH SECTION 903.3.1.1 OR 903.3.1.2 AND AN EMERGENCY VOICE/ALARM COMMUNICATIONS SYSTEM IN ACCORDANCE WITH SECTION 907.5.2.2.

CALCULATION WITH SPRINKLER SYSTEM = 0.2 INCHES PER OCCUPANT
305 OCCUPANTS (0.15" / OCCUPANT) = 45.75" OF EGRESS WIDTH (544" PROVIDED)

EGRESS WIDTHS COMPLY WITH SECTION 1004.

SECTION 1006 'NUMBER OF EXITS AND EXIT ACCESS DOORWAYS'
TABLE 1006.2.1 'SPACES WITH ONE EXIT OR EXIT ACCESS DOORWAY'
IN OCCUPANCIES 'F-1', 'S-1', 'B' THE COMMON PATH OF EGRESS TRAVEL SHALL NOT EXCEED 100 FEET WITH A SPRINKLER SYSTEM

SECTION 1009.7 'EXTERIOR AREA FOR ASSISTED RESCUE'
EXTERIOR AREAS FOR ASSISTED RESCUE SHALL BE ACCESSED BY AN ACCESSIBLE ROUTE FROM THE AREA SERVED. WHERE THE EXIT DISCHARGE DOES NOT INCLUDE AN ACCESSIBLE ROUTE FROM AN EXIT LOCATED ON THE LEVEL OF EXIT DISCHARGE TO A PUBLIC WAY, AN EXTERIOR AREA OF ASSISTED RESCUE SHALL BE PROVIDED ON THE EXTERIOR LANDING IN ACCORDANCE WITH SECTIONS 1009.7.1 THROUGH 1009.7.4.

SECTION 1009.7.2 'SEPARATION'
EXTERIOR WALLS SEPARATING THE EXTERIOR AREA OF ASSISTED RESCUE FROM THE INTERIOR OF THE BUILDING SHALL HAVE A MINIMUM FIRE-RESISTANCE RATING OF 1 HOUR, RATED FOR EXPOSURE TO FIRE FROM THE INSIDE. THE FIRE-RESISTANCE-RATED EXTERIOR WALL CONSTRUCTION SHALL EXTEND HORIZONTALLY 10 FEET BEYOND THE LANDING ON EITHER SIDE OF THE LANDING OR EQUIVALENT FIRE-RESISTANCE-RATED CONSTRUCTION IS PERMITTED TO EXTEND OUT PERPENDICULAR TO THE EXTERIOR WALL 4 FEET MINIMUM ON THE SIDE OF THE LANDING. THE FIRE-RESISTANCE-RATED CONSTRUCTION SHALL EXTEND VERTICALLY FROM THE GROUND TO A POINT 10 FEET ABOVE THE FLOOR LEVEL OF THE AREA FOR ASSISTED RESCUE OR TO THE ROOF LINE, WHICHEVER IS LOWER. OPENINGS WITHIN SUCH FIRE-RESISTANCE-RATED EXTERIOR WALLS SHALL BE PROTECTED IN ACCORDANCE WITH SECTION 716.
EXCEPTION: THE FIRE-RESISTANCE RATING AND OPENING PROTECTIVES ARE NOT REQUIRED IN THE EXTERIOR WALL WHERE THE BUILDING IS EQUIPPED THROUGHOUT WITH AN AUTOMATIC SPRINKLER SYSTEM INSTALLED IN ACCORDANCE WITH SECTION 903.1.1 OR 903.1.2.

SECTION 1017 'EXIT ACCESS TRAVEL DISTANCE'
TABLE 1017.2 'EXIT ACCESS TRAVEL DISTANCE'
IN OCCUPANCIES 'F-1', 'S-1', 'B' THE EXIT ACCESS TRAVEL DISTANCE SHALL BE 250 FEET WITH A SPRINKLER SYSTEM.

SECTION 1017.2.2 'GROUPS F-1 AND S-1 INCREASE'
THE MAXIMUM EXIT ACCESS TRAVEL DISTANCE SHALL BE 400 FEET IN GROUP F-1 OR S-1 OCCUPANCIES WHERE ALL OF THE FOLLOWING CONDITIONS ARE MET:
1. THE PORTION OF THE BUILDING CLASSIFIED AS GROUP F-1 OR S-1 IS LIMITED TO ONE STORY IN HEIGHT
2. THE MINIMUM HEIGHT FROM THE FINISHED FLOOR TO THE BOTTOM OF THE CEILING OR ROOF SLAB OR DECK IS 24 FEET.
3. THE BUILDING IS EQUIPPED THROUGHOUT WITH AN AUTOMATIC SPRINKLER SYSTEM IN ACCORDANCE WITH SECTION 903.3.1.1

SECTION 1017.3 'MEASUREMENT'
EXIT ACCESS TRAVEL DISTANCE SHALL BE MEASURED FROM THE MOST REMOTE POINT OF EACH ROOM, AREA OR SPACE ALONG THE NATURAL AND UNOBSTRUCTED PATH OF HORIZONTAL AND VERTICAL EGRESS TRAVEL TO THE ENTRANCE OF AN EXIT. WHERE MORE THAN ONE EXIT IS REQUIRED, EXIT ACCESS TRAVEL DISTANCE SHALL BE MEASURED TO THE NEAREST EXIT.

TRAVEL DISTANCES COMPLY WITH SECTION 1017.

CHAPTER 29 - PLUMBING SYSTEMS

TABLE 2902.1 ' MINIMUM NUMBER OF PLUMBING FACILITIES'
TOTAL PROVIDED:
WATER CLOSETS: 2 PROVIDED
LAVATORIES: 2 PROVIDED
SERVICE SINK: 1 PROVIDED

TABLE 2902.1 WILL ACCOMMODATE AN OCCUPANCY OF 40

A PORTION OF THE SHELL BUILDING WILL ACCOMODATE AN INITIAL OCCUPANCY OF 40 OCCUPANTS INCLUDING BOTH EMPLOYEES AND CUSTOMERS WITH A MAXIMUM TRAVEL DISTANCE OF 500' FROM THE TOILET ROOM. THE REQUIRED PLUMBING FIXTURES WILL BE VERIFIED UNDER A FUTURE TENANT OCCUPANCY

© 2026 Partners in Design Architects, Inc.


REVISIONS
1 05.12.26 SITE 1 OPERATIONAL RESUBMITTAL
2 05.15.26 SITE 1 OPERATIONAL COMMENTS
3 07.24.26 SUBMITTAL #4
09.22.26 SITE 1 OPERATIONAL CONDITIONAL APPROVAL SET

ZILBER INDUSTRIAL 3
108th St, Lakeview Corporate Park, Pleasant Prairie, WI
CODE SUMMARY

2610 Lake Cook Road
Suite 280
Riverwoods, IL 60015
Ph.: (847) 940-0300
www.pdarchitects.com

Partners in Design ARCHITECTS

PROJECT NO.: 522.22.031
DRAWN BY: CTS
CHECKED BY: WHB
DATE: 08.12.22
SHEET NO.: A0.1

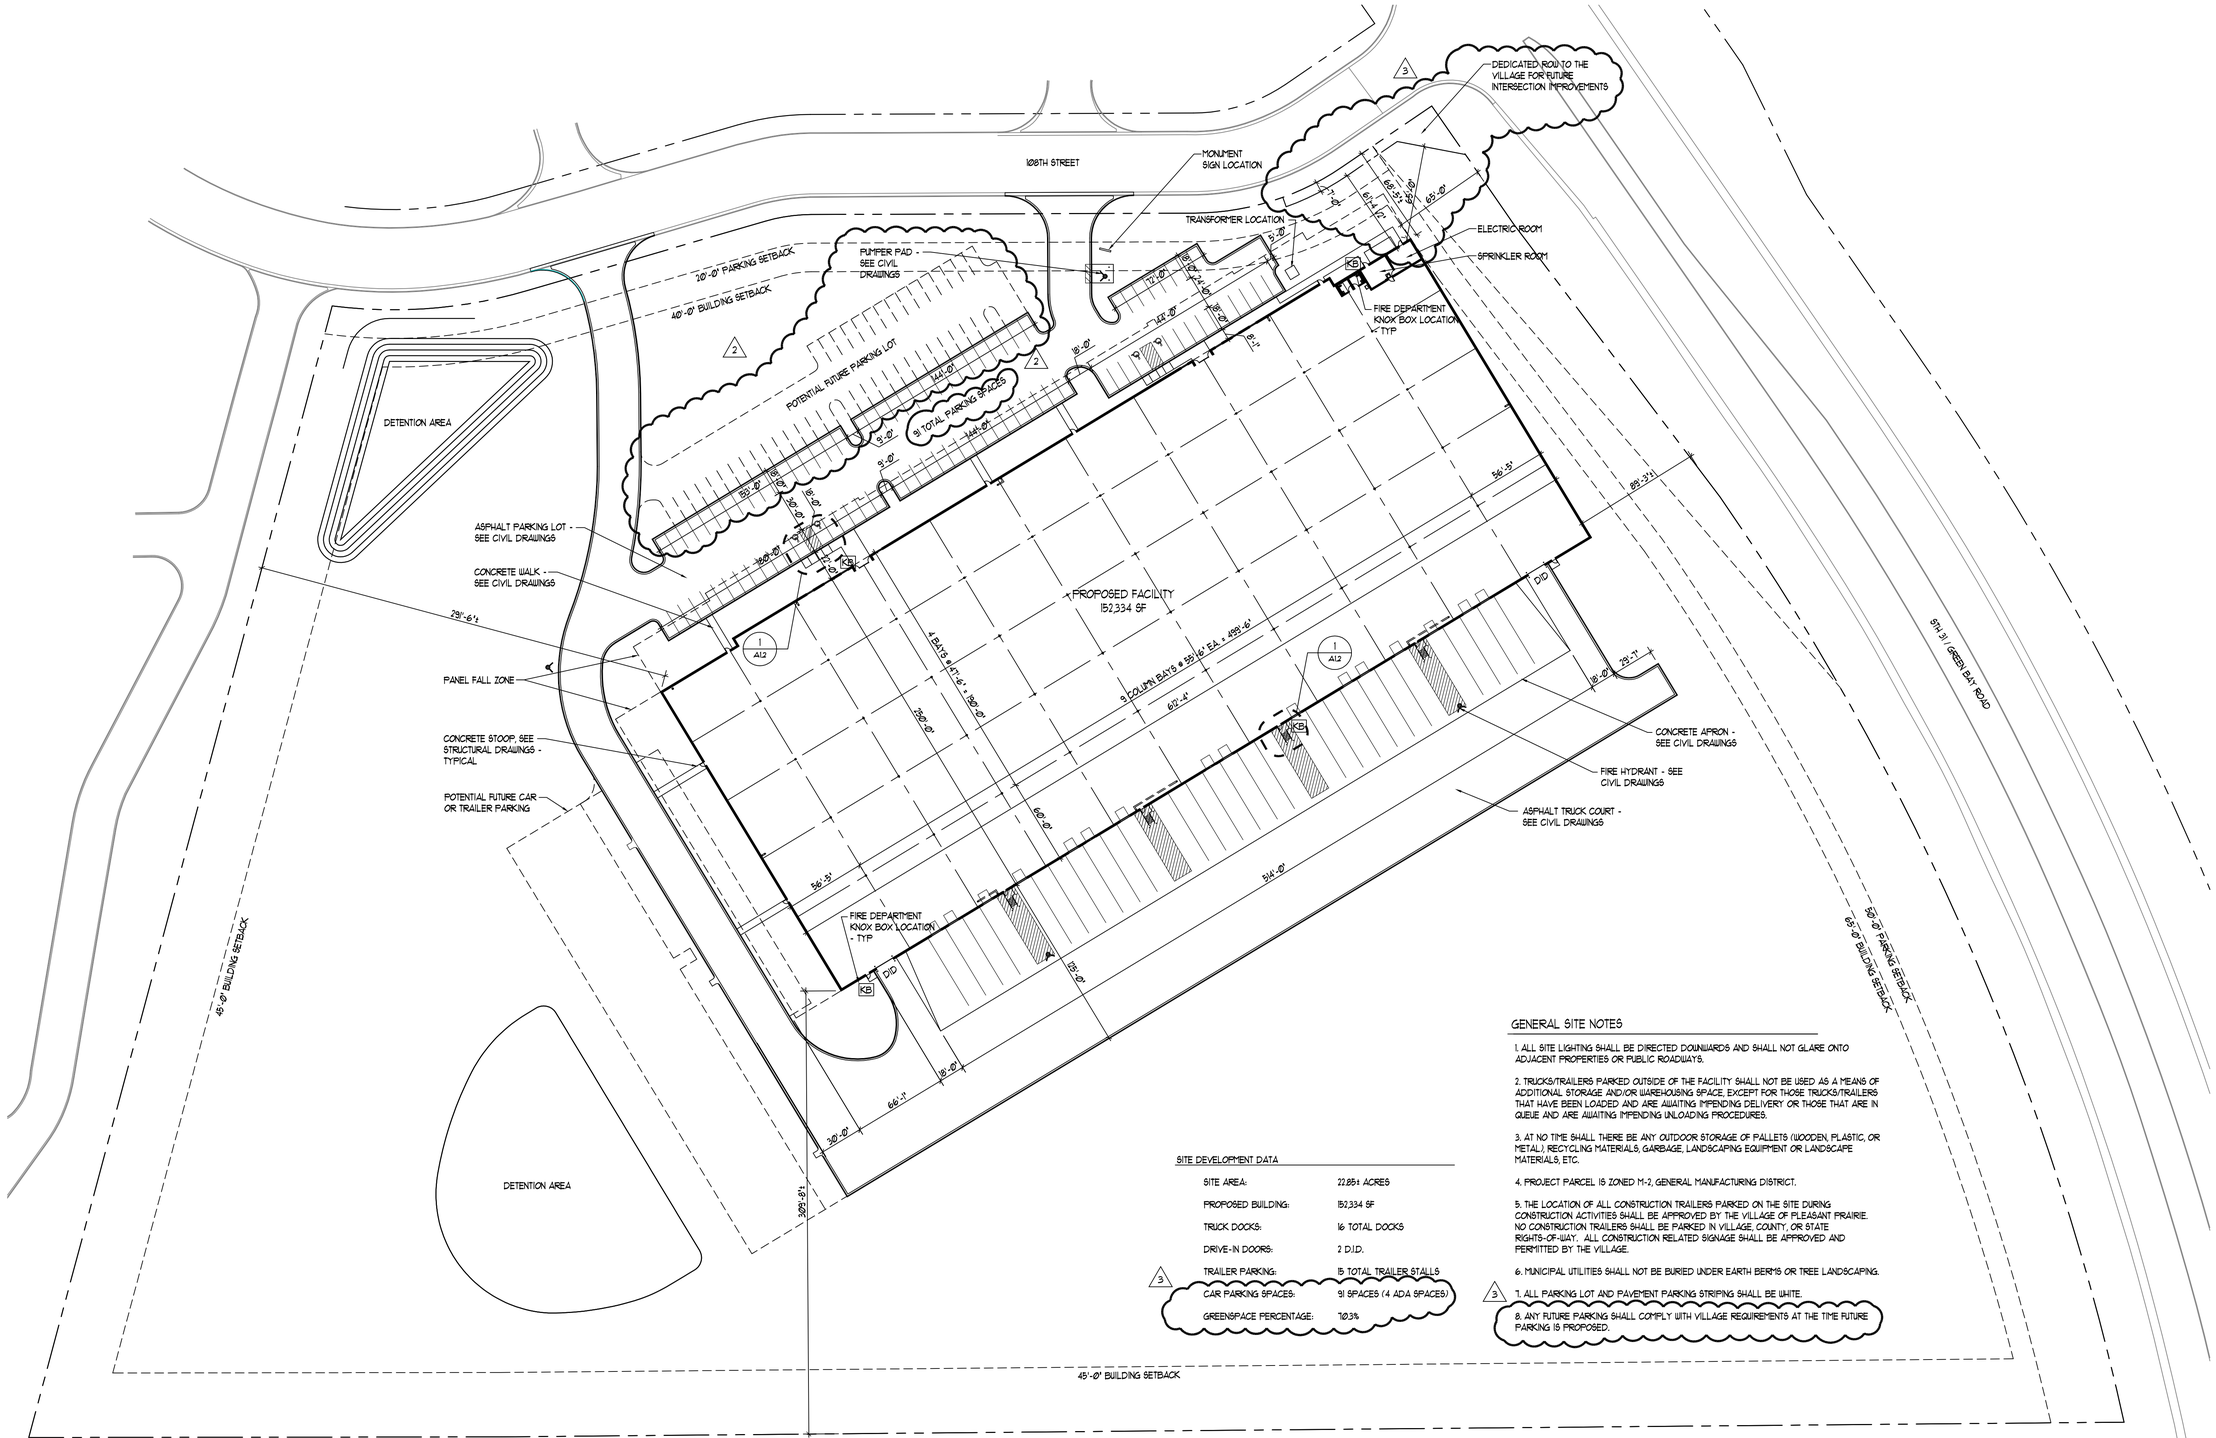

1 A1.1 SITE PLAN
1" - 50'-0"

SITE DEVELOPMENT DATA

SITE AREA:	22.85± ACRES
PROPOSED BUILDING:	152,334 SF
TRUCK DOCKS:	16 TOTAL DOCKS
DRIVE-IN DOORS:	2 D.I.D.
TRAILER PARKING:	15 TOTAL TRAILER STALLS
CAR PARKING SPACES:	91 SPACES (4 ADA SPACES)
GREENSPACE PERCENTAGE:	10.3%

GENERAL SITE NOTES

1. ALL SITE LIGHTING SHALL BE DIRECTED DOWNWARDS AND SHALL NOT GLARE ONTO ADJACENT PROPERTIES OR PUBLIC ROADWAYS.

2. TRUCKS/TRAILERS PARKED OUTSIDE OF THE FACILITY SHALL NOT BE USED AS A MEANS OF ADDITIONAL STORAGE AND/OR WAREHOUSING SPACE, EXCEPT FOR THOSE TRUCKS/TRAILERS THAT HAVE BEEN LOADED AND ARE AWAITING IMPENDING DELIVERY OR THOSE THAT ARE IN QUEUE AND ARE AWAITING IMPENDING UNLOADING PROCEDURES.

3. AT NO TIME SHALL THERE BE ANY OUTDOOR STORAGE OF PALLETS (WOODEN, PLASTIC, OR METAL), RECYCLING MATERIALS, GARBAGE, LANDSCAPING EQUIPMENT OR LANDSCAPE MATERIALS, ETC.

4. PROJECT PARCEL IS ZONED M-2, GENERAL MANUFACTURING DISTRICT.

5. THE LOCATION OF ALL CONSTRUCTION TRAILERS PARKED ON THE SITE DURING CONSTRUCTION ACTIVITIES SHALL BE APPROVED BY THE VILLAGE OF PLEASANT PRAIRIE. NO CONSTRUCTION TRAILERS SHALL BE PARKED IN VILLAGE, COUNTY, OR STATE RIGHTS-OF-WAY. ALL CONSTRUCTION RELATED SIGNAGE SHALL BE APPROVED AND PERMITTED BY THE VILLAGE.

6. MUNICIPAL UTILITIES SHALL NOT BE BURIED UNDER EARTH BERMS OR TREE LANDSCAPING.

7. ALL PARKING LOT AND PAVEMENT PARKING STRIPING SHALL BE WHITE.

8. ANY FUTURE PARKING SHALL COMPLY WITH VILLAGE REQUIREMENTS AT THE TIME FUTURE PARKING IS PROPOSED.

© 2026 Partners in Design Architects, Inc.


REVISIONS
3 05.20.26 SITE 1 OPERATIONAL RESUBMITTAL
2 05.1.26 SITE 1 OPERATIONAL COMMENTS
1 07.24.26 SUBMITTAL #4
09.02.26 SITE 1 OPERATIONAL CONDITIONAL APPROVAL SET

ZILBER INDUSTRIAL 3
108th St, Lakeview Corporate Park, Pleasant Prairie, WI
SITE PLAN

2610 Lake Cook Road
Suite 280
Riverwoods, IL 60015
Ph.: (847) 940-0300
www.pidarchitects.com

Partners in Design ARCHITECTS


PROJECT NO.: 522.22.031
DRAWN BY: JJH
CHECKED BY: WHB
DATE: 08.12.22
SHEET NO.: A1.1

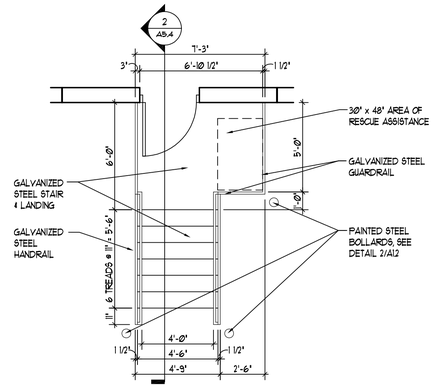

1 A1.2 EGRESS STAIR PLAN
1/4" = 1'-0"

TRUE NORTH

PLAN NORTH

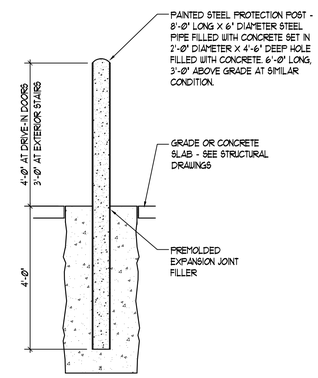

2 A1.2 BOLLARD SECTION
1/2" = 1'-0"

© 2026 Partners in Design Architects, Inc.

ZILBER INDUSTRIAL 3
108th St, Lakeview Corporate Park, Pleasant Prairie, WI


SITE DETAILS

REVISIONS
1 05.10.26 SITE 1 OPERATIONAL RESUBMITTAL
2 05.13.26 SITE 1 OPERATIONAL COMMENTS
3 07.24.26 SUBMITTAL #4
4 09.22.26 SITE 1 OPERATIONAL CONDITIONAL APPROVAL SET

2610 Lake Cook Road
Suite 280
Riverwoods, IL 60015
Ph.: (847) 940-0300
www.pidarchitects.com


PartnersinDesign ARCHITECTS

PROJECT NO.: 522.22.031
DRAWN BY: CTS
CHECKED BY: WHB
DATE: 08.12.22
SHEET NO.: A1.2

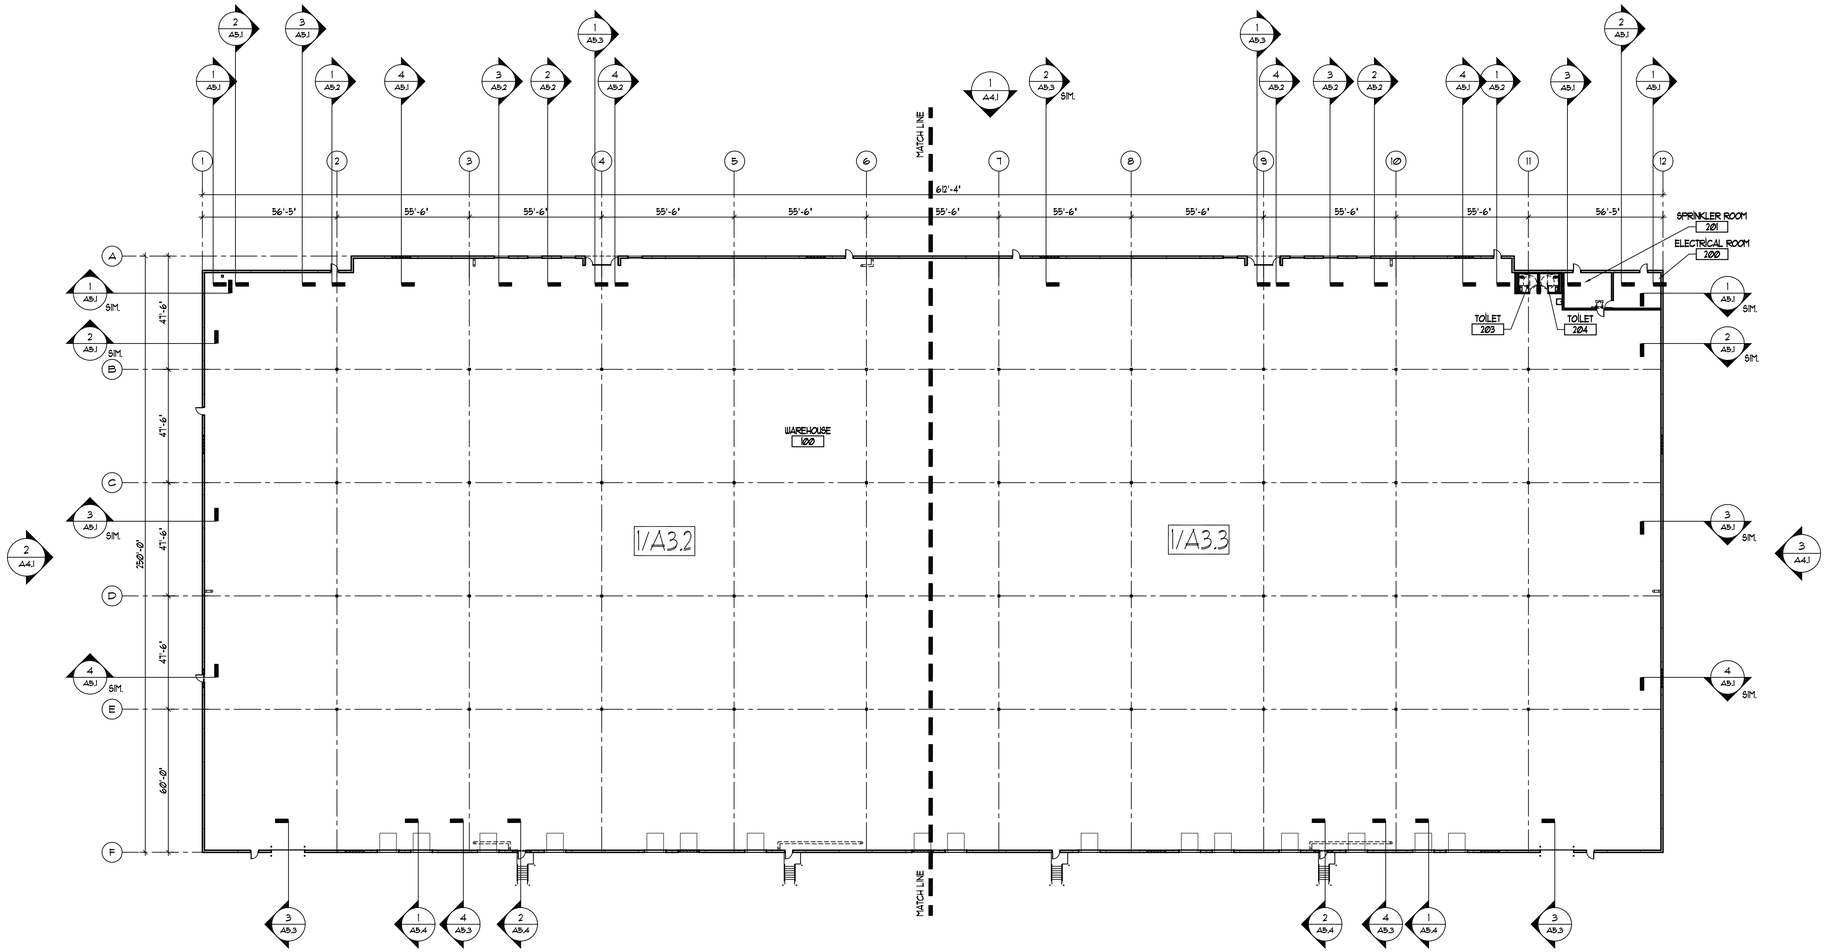

1 A3.1 OVERALL BUILDING PLAN
1" = 30'-0"

4 A4.1

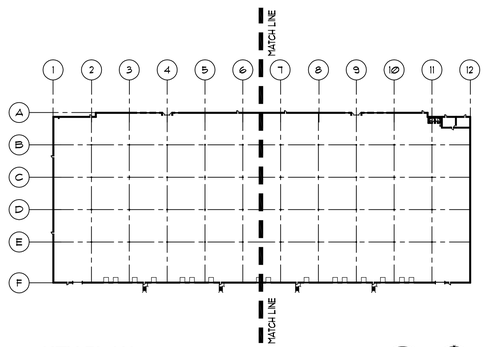

KEY PLAN
NOT TO SCALE

© 2026 Partners in Design Architects, Inc.

REVISIONS
1 05.20.26 SITE 1 OPERATIONAL RESUBMITTAL
2 06.11.26 SITE 1 OPERATIONAL COMMENTS
3 07.24.26 SUBMITTAL #4
4 09.02.26 SITE 1 OPERATIONAL CONDITIONAL APPROVAL SET


ZILBER INDUSTRIAL 3
108th St, Lakeview Corporate Park, Pleasant Prairie, WI

OVERALL BUILDING PLAN

2610 Lake Cook Road
Suite 280
Riverwoods, IL 60015
Ph.: (847) 940-0300
www.pidarchitects.com

PartnersinDesign ARCHITECTS

PROJECT NO.: 522.22.031
DRAWN BY: JJH
CHECKED BY: WHB
DATE: 08.12.22
SHEET NO.: A3.1

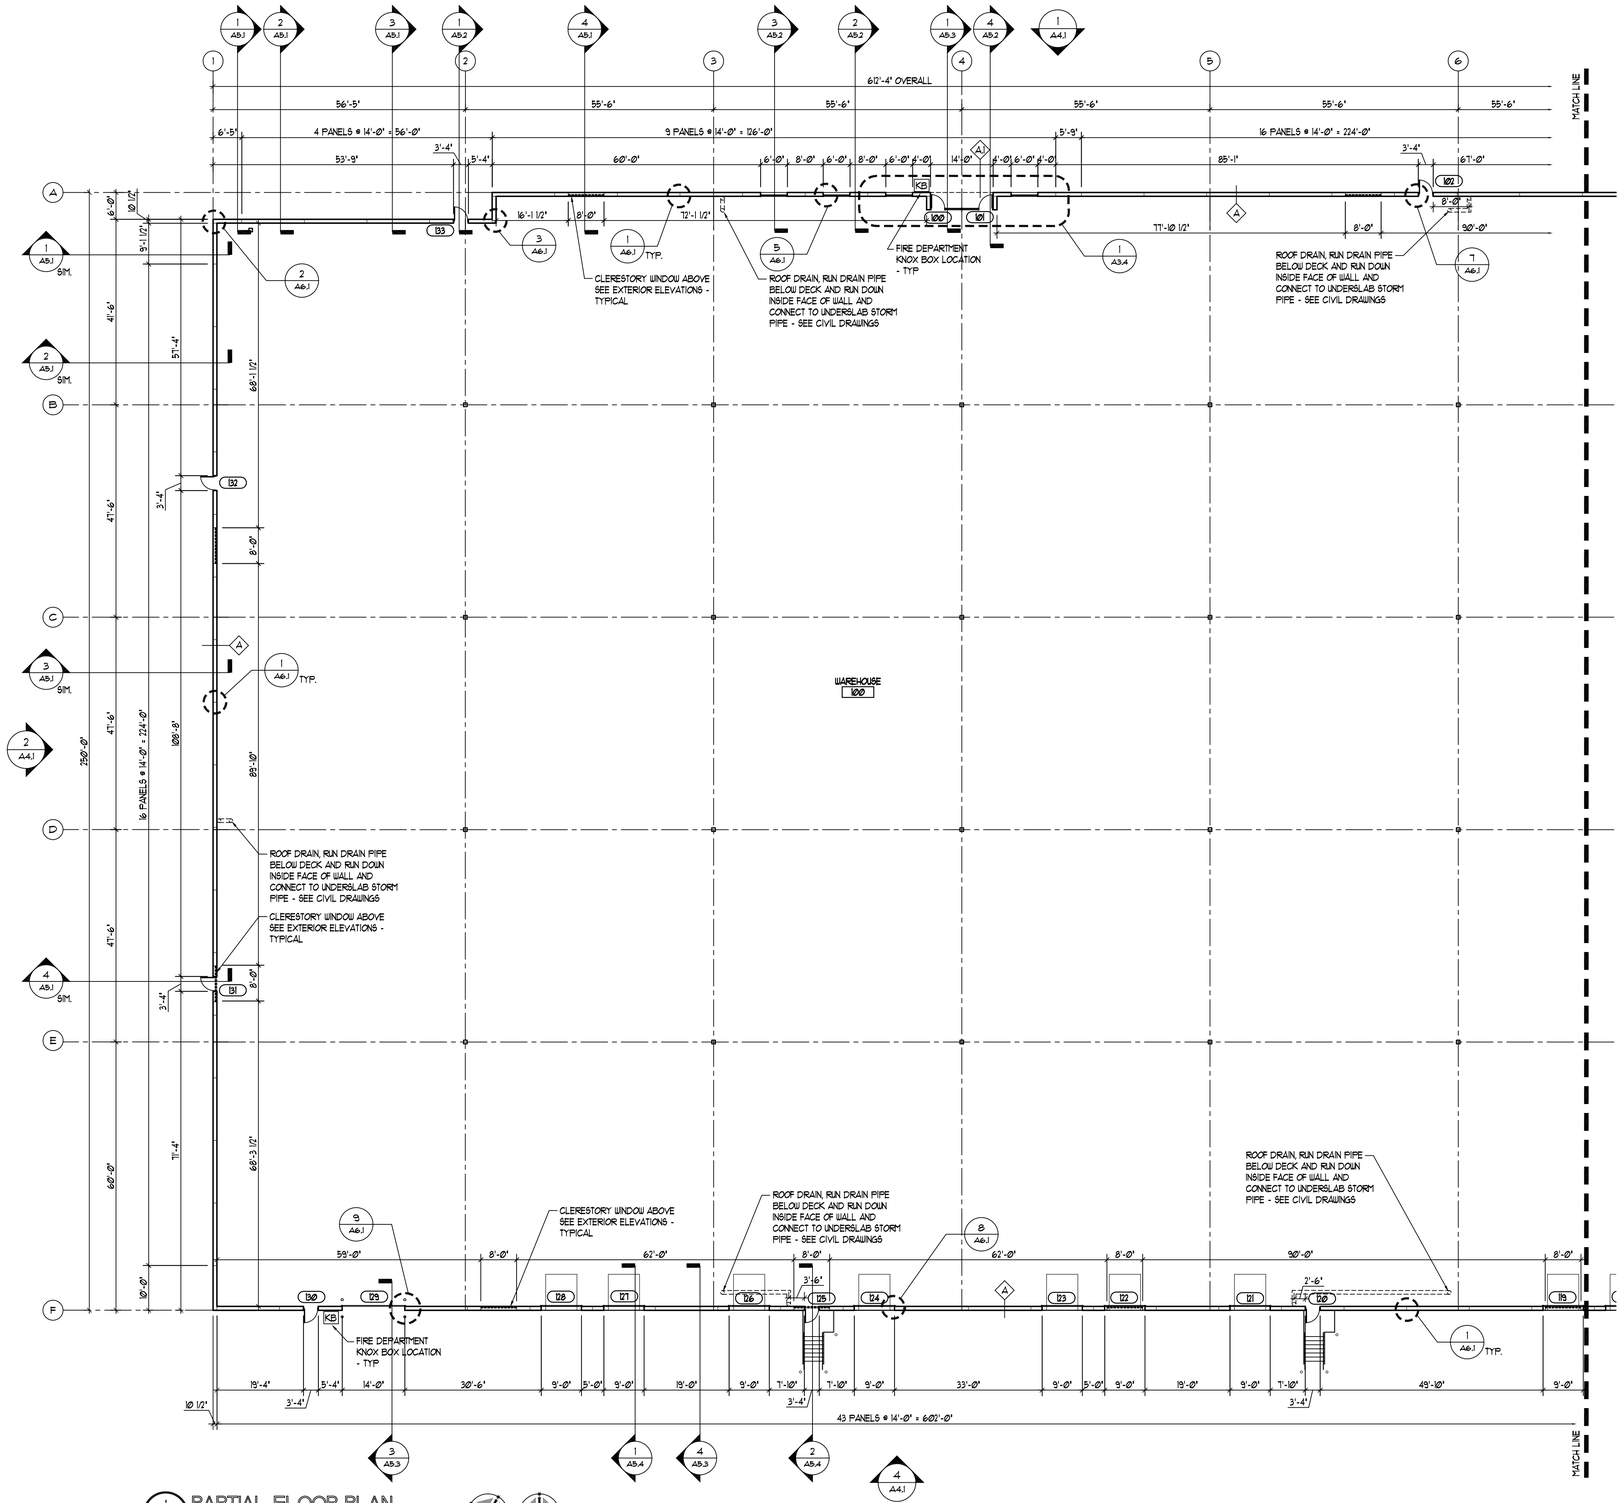

PARTIAL FLOOR PLAN


A3.2 1/16" = 1'-0"

TRUE NORTH

PLAN NORTH


WALL TYPES

1. ALL INTERIOR WALLS TO BE TYPE 'B' UNLESS NOTED OTHERWISE.
2. ALL EXTERIOR WALLS TO BE TYPE 'A' UNLESS NOTED OTHERWISE.
3. ALL GYPSUM BOARD TO BE 5/8" TYPE 'X' UNLESS NOTED OTHERWISE.
4. CONFIRM THE REQUIRED STUD THICKNESS PER SELECTED MANUFACTURER'S LOAD TABLES FOR THE WALL HEIGHTS INDICATED ON THE PLANS.
5. PROVIDE GYPSUM BOARD EXPANSION JOINTS AS REQUIRED PER MANUFACTURER'S RECOMMENDATIONS.

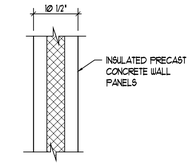


A
1. SEE EXTERIOR ELEVATIONS FOR HEIGHT

A1
1. 12" THICK

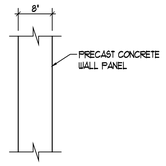


B
1. UL #U905 - 1 HOUR RATED
2. EXTEND WALLS TO DECK


B1
1. UN-RATED
2. EXTEND WALLS TO DECK

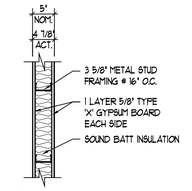


C
1. EXTEND WALLS TO 11'-4" AFF.

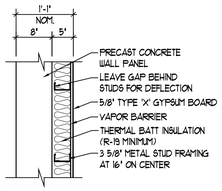

D
1. EXTEND PRECAST WALL TO DECK
2. EXTEND INTERIOR GYPSUM BOARD WALL TO 11'-4" AFF.

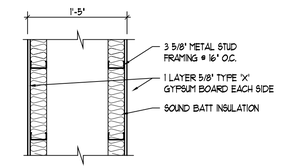

E
1. EXTEND WAREHOUSE WALL TO 11'-4" AFF.
2. EXTEND TOILET ROOM WALL 6" ABOVE CEILING

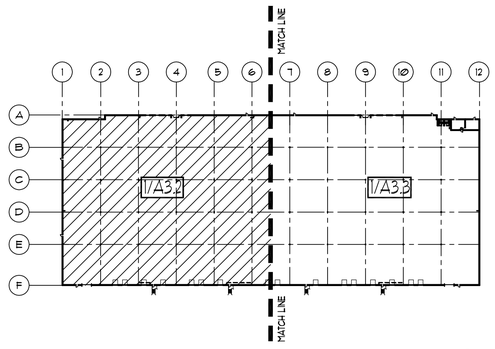

KEY PLAN

NOT TO SCALE

TRUE NORTH

PLAN NORTH

REVISIONS
1. 03.20.26 SITE 1 OPERATIONAL RESUBMITTAL
2. 05.1.26 SITE 1 OPERATIONAL COMMENTS
3. 07.24.26 SUBMITTAL #4
4. 09.22.26 SITE 1 OPERATIONAL CONDITIONAL APPROVAL SET

ZILBER INDUSTRIAL 3

108th St, Lakeview Corporate Park, Pleasant Prairie, WI

PARTIAL FLOOR PLAN

2610 Lake Cook Road
Suite 280
Riverwoods, IL 60015
Ph.: (847) 940-0300
www.pidarchitects.com

Partners in Design ARCHITECTS

PROJECT NO.: 522.22.031


DRAWN BY: JJH

CHECKED BY: WHB

DATE: 08.12.22

SHEET NO.: A3.2

© 2026 Partners in Design Architects, Inc.

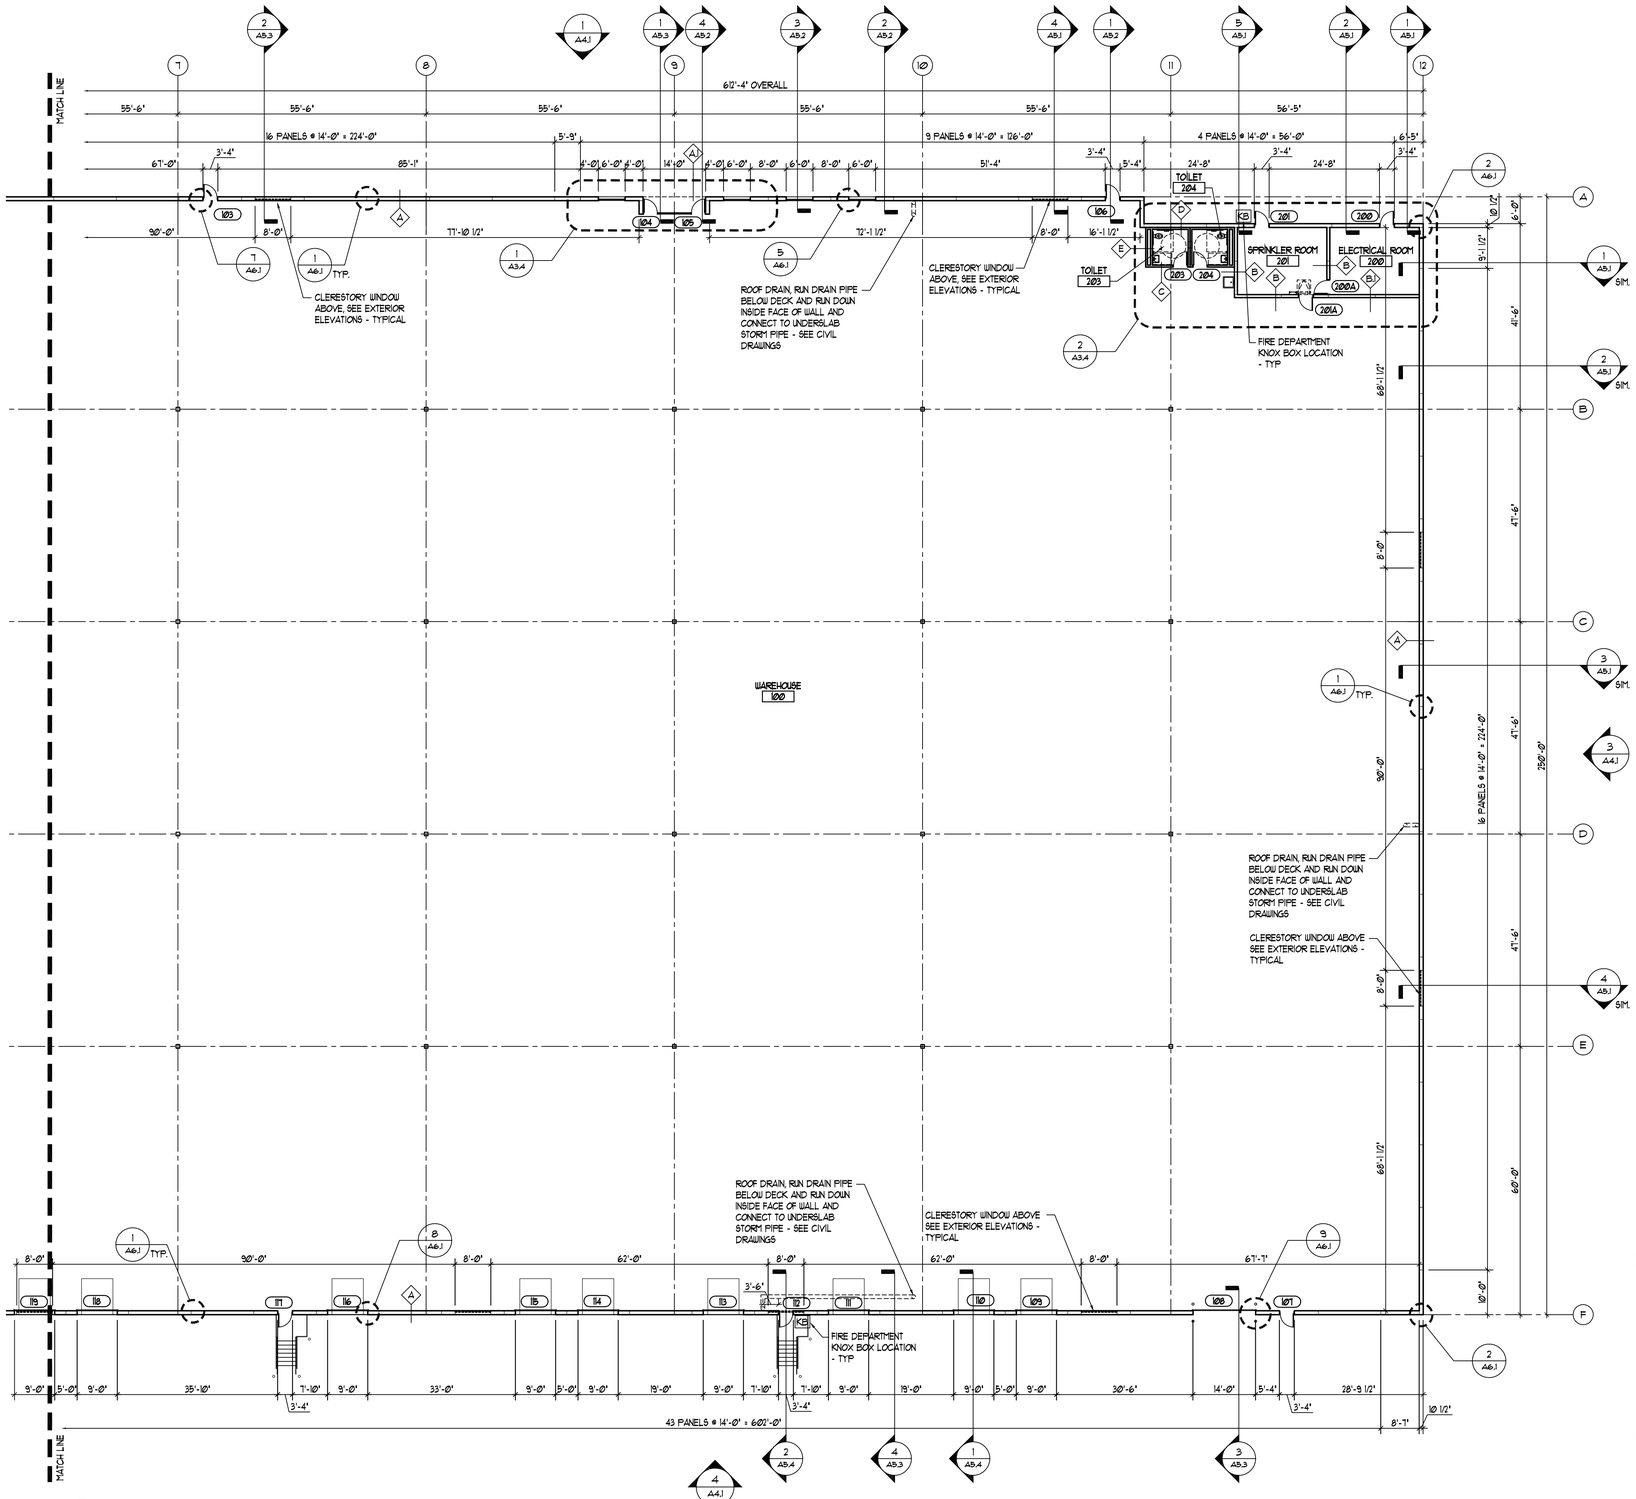


1 PARTIAL FLOOR PLAN
A3.3 1/16" = 1'-0"

TRUE NORTH


PLAN NORTH

WALL TYPES


1. ALL INTERIOR WALLS TO BE TYPE 'B' UNLESS NOTED OTHERWISE.
2. ALL EXTERIOR WALLS TO BE TYPE 'A' UNLESS NOTED OTHERWISE.
3. ALL GYPSUM BOARD TO BE 5/8" TYPE 'X' UNLESS NOTED OTHERWISE.
4. CONFIRM THE REQUIRED STUD THICKNESS PER SELECTED MANUFACTURER'S LOAD TABLES FOR THE WALL HEIGHTS INDICATED ON THE PLANS.
5. PROVIDE GYPSUM BOARD EXPANSION JOINTS AS REQUIRED PER MANUFACTURER'S RECOMMENDATIONS.

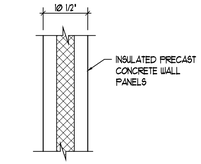


A
1. SEE EXTERIOR ELEVATIONS FOR HEIGHT
A1
1. 12" THICK

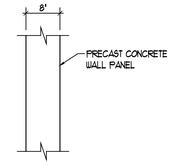


B
1. UL #U905 - 1 HOUR RATED
2. EXTEND WALLS TO DECK
B1
1. UN-RATED
2. EXTEND WALLS TO DECK

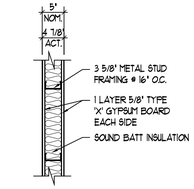


C
1. EXTEND WALLS TO 11'-4" A.F.F.

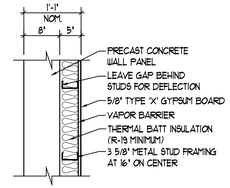

D
1. EXTEND PRECAST WALL TO DECK
2. EXTEND INTERIOR GYPSUM BOARD WALL TO 11'-4" A.F.F.

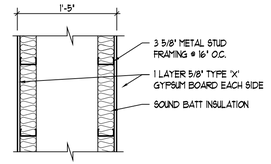

E
1. EXTEND WAREHOUSE WALL TO 11'-4" A.F.F.
2. EXTEND TOILET ROOM WALL 6" ABOVE CEILING

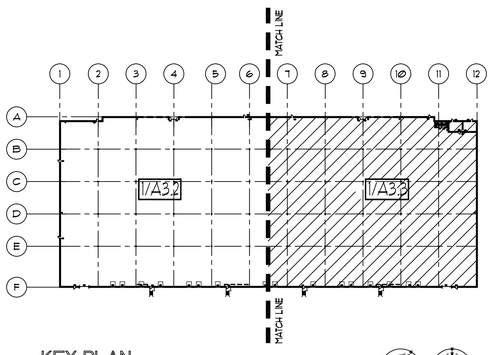

KEY PLAN
NOT TO SCALE

TRUE NORTH

PLAN NORTH

© 2026 Partners in Design Architects, Inc.

REVISIONS
1 05.20.26 SITE 1 OPERATIONAL RESUBMITTAL
2 05.11.26 SITE 1 OPERATIONAL COMMENTS
3 07.24.26 SUBMITTAL #4
09.02.26 SITE 1 OPERATIONAL CONDITIONAL APPROVAL SET


ZILBER INDUSTRIAL 3
108th St, Lakeview Corporate Park, Pleasant Prairie, WI

PARTIAL FLOOR PLAN

2610 Lake Cook Road
Suite 280
Riverwoods, IL 60015
Ph.: (847) 940-0300
www.pdarchitects.com


Partners in Design ARCHITECTS

PROJECT NO.: 522.22.031
DRAWN BY: JJH
CHECKED BY: WHB
DATE: 08.12.22
SHEET NO.: A3.3

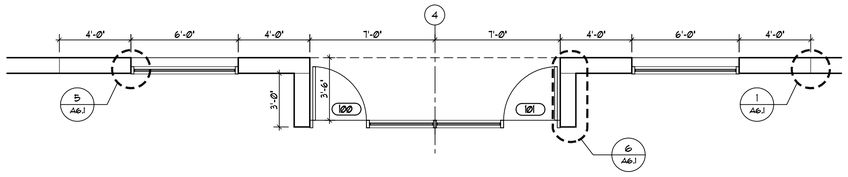


1 A3.4 ENLARGED FLOOR PLAN
1/4"=1'-0"

TRUE NORTH | PLAN NORTH

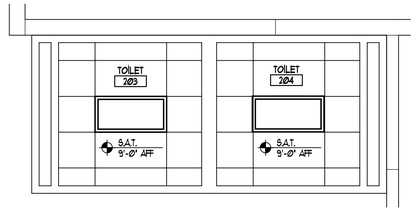


3 A3.4 TOILET REFLECTED CEILING PLAN
1/4"=1'-0"

TRUE NORTH | PLAN NORTH

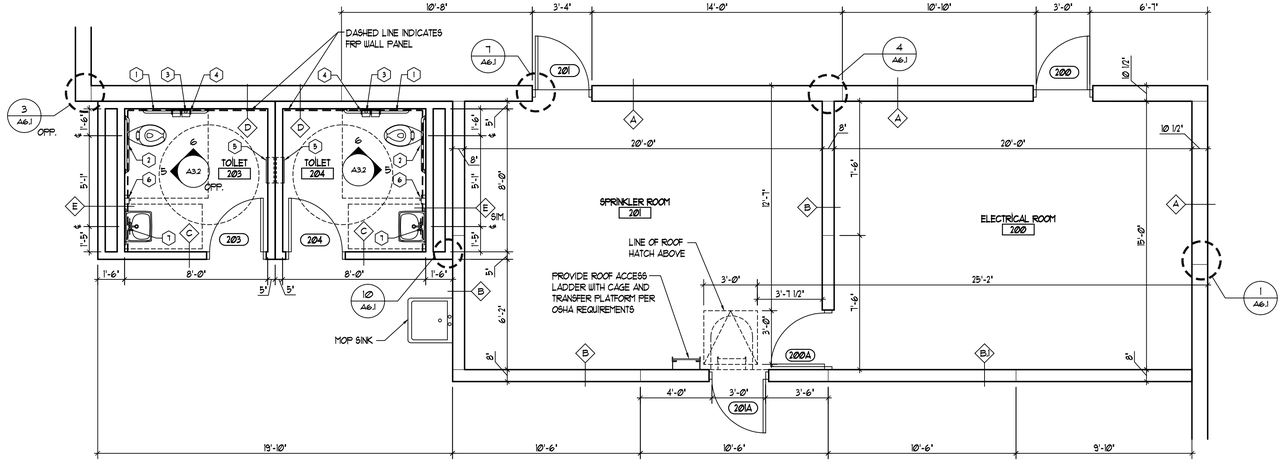

2 A3.4 ENLARGED FLOOR PLAN
1/4"=1'-0"


TRUE NORTH | PLAN NORTH

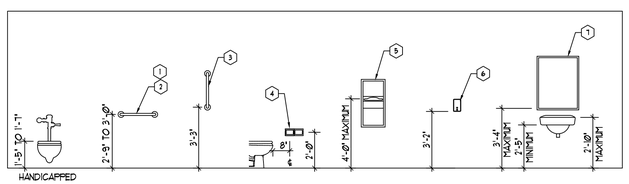

TOILET ACCESSORIES MOUNTING HEIGHTS
N.T.S.

GENERAL NOTES:

1. ACCESS TO ALL DISPENSING AND OPERABLE CONTROLS SHOULD BE 15" TO 48" ABOVE FINISHED FLOOR.
2. REFER TO MANUFACTURERS' GUIDELINES FOR INSTALLATION.
3. T.O.O. INDICATES TOP OF OPENING.
4. EXPOSED UNDER LAVATORY PIPING TO BE WRAPPED TO PROTECT AGAINST CONTACT.
5. PROVIDE SOLID BLOCKING AT ALL GRAB BAR LOCATIONS AND IN WALLS AS REQUIRED.

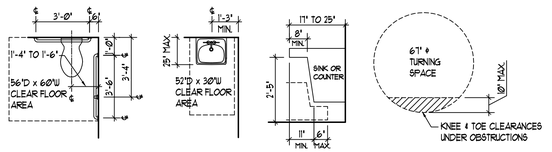

FIXTURE CLEARANCES
N.T.S.


GENERAL NOTES:

1. ALL FIXTURES TO MEET ADAAG CLEARANCE AND HEIGHT REQUIREMENTS.
2. ALL TOILET FLUSH CONTROLS SHALL BE ON THE WIDE SIDE OF STALL.


TOILET ACCESSORIES LEGEND

TAG	DESCRIPTION	MANUFACTURER	MODEL#	NOTE
1	42" GRAB BAR	BOBRICK	B-6806 (42)	
2	36" GRAB BAR	BOBRICK	B-6806 (36)	
3	18" GRAB BAR	BOBRICK	B-6806 (18)	
4	TOILET PAPER DISPENSER	BOBRICK	B-2888	
5	RECESSED PAPER TOWEL DISPENSER/WASTE (SMALL)	BOBRICK	B-369	
6	WALL MOUNTED SOAP DISPENSER	BOBRICK	B-4112	
7	SURFACE MOUNTED MIRROR (STANDARD SIZE)	BOBRICK	B-165 (24 x 36)	

APPROVED ALTERNATE MANUFACTURERS: ASI, BRADLEY

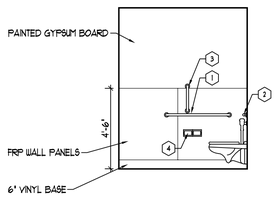

4 A3.4 TOILET ROOM ELEVATION
1/4"=1'-0"

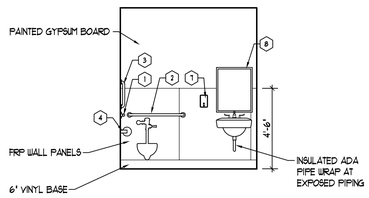

5 A3.4 TOILET ROOM ELEVATION
1/4"=1'-0"

© 2026 Partners in Design Architects, Inc.

REVISIONS
- 05.01.26 SITE 1 OPERATIONAL RESUBMITTAL
- 05.11.26 SITE 1 OPERATIONAL COMMENTS
- 07.24.26 SUBMITTAL #4
- 09.02.26 SITE 1 OPERATIONAL CONDITIONAL APPROVAL SET

ZILBER INDUSTRIAL 3
108th St, Lakeview Corporate Park, Pleasant Prairie, WI

ENLARGED PLANS & NOTES

2610 Lake Cook Road
Suite 280
Rivenwoods, IL 60015
Ph.: (847) 940-0300
www.pidarchitects.com

Partners in Design ARCHITECTS

PROJECT NO.: 522.22.031
DRAWN BY: JJH | CHECKED BY: WHB
DATE: 08.12.22
SHEET NO.: A3.4

ROOM FINISH SCHEDULE

ROOM NAME	NO.	FLOOR	BASE	WALLS				CEILING		PAINT		REMARKS
				NORTH	EAST	SOUTH	WEST	MAT'L	HT.	WALLS	CLG	
WAREHOUSE	100	S. CONC.	--	CONC. / GYP. BD.	CONC.	CONC.	CONC.	MTL. DECK	VARIES	YES	NO	NOTES 1, 2, 3
ELECTRICAL ROOM	200	S. CONC.	--	CONC.	CONC.	CONC.	CONC.	MTL. DECK	VARIES	YES	NO	NOTE 5
SPRINKLER ROOM	201	S. CONC.	--	CONC.	CONC.	CONC.	CONC.	MTL. DECK	VARIES	YES	NO	NOTE 5
TOILET	203	S. CONC.	VINYL	FRP / GYP. BD.	GYP. BD.	GYP. BD.	FRP / GYP. BD.	S.A.T.	9'-0"	YES	NO	NOTE 4
TOILET	204	S. CONC.	VINYL	FRP / GYP. BD.	FRP / GYP. BD.	GYP. BD.	GYP. BD.	S.A.T.	9'-0"	YES	NO	NOTE 4


ROOM FINISH SCHEDULE NOTES:
1. PROVIDE 4" VINYL BASE ON GYSUM BOARD WALLS ONLY.
2. PROVIDE 4'-0" x 4'-0" FIBER REINFORCED PLASTIC WALL PANEL BEHIND SERVICE SINK.
3. INTERIOR SIDE OF HOLLOW METAL DOORS AND FRAMES TO BE HALLMAN LINDSEY JET GRAY, OR APPROVED EQUAL.
4. PROVIDE 6" VINYL BASE WITH CONTINUOUS WATERPROOF ADHESIVE TO WALL AND FLOOR.
5. WALLS TO BE PAINTED WITH PRIMER PAINT ONLY

DOOR SCHEDULE


NO.	SIZE	MATERIAL		TYPE		HDW SET	REMARKS
		DOOR	FRAME	DOOR	FRAME		
100	3'-0" x 7'-0" x 1 3/4"	ALUM	ALUM	A	5/A4.1	SET 1	
101	3'-0" x 7'-0" x 1 3/4"	ALUM	ALUM	A	5/A4.1	SET 1	
102	3'-0" x 7'-0" x 1 3/4"	HM	HM	B	A	SET 2	
103	3'-0" x 7'-0" x 1 3/4"	HM	HM	B	A	SET 2	
104	3'-0" x 7'-0" x 1 3/4"	ALUM	ALUM	A	5/A4.1	SET 1	
105	3'-0" x 7'-0" x 1 3/4"	ALUM	ALUM	A	5/A4.1	SET 1	
106	3'-0" x 7'-0" x 1 3/4"	HM	HM	B	A	SET 2	
107	3'-0" x 7'-0" x 1 3/4"	HM	HM	B	A	SET 2	
108	14'-0" x 16'-0" x 2"	STEEL		C			OVERHEAD SECTIONAL DOOR
109	9'-0" x 10'-0" x 2"	STEEL		C			OVERHEAD SECTIONAL DOOR
110	9'-0" x 10'-0" x 2"	STEEL		C			OVERHEAD SECTIONAL DOOR
111	9'-0" x 10'-0" x 2"	STEEL		C			OVERHEAD SECTIONAL DOOR
112	3'-0" x 7'-0" x 1 3/4"	HM	HM	B	A	SET 2	
113	9'-0" x 10'-0" x 2"	STEEL		C			OVERHEAD SECTIONAL DOOR
114	9'-0" x 10'-0" x 2"	STEEL		C			OVERHEAD SECTIONAL DOOR
115	9'-0" x 10'-0" x 2"	STEEL		C			OVERHEAD SECTIONAL DOOR
116	9'-0" x 10'-0" x 2"	STEEL		C			OVERHEAD SECTIONAL DOOR
117	3'-0" x 7'-0" x 1 3/4"	HM	HM	B	A	SET 2	
118	9'-0" x 10'-0" x 2"	STEEL		C			OVERHEAD SECTIONAL DOOR
119	9'-0" x 10'-0" x 2"	STEEL		C			OVERHEAD SECTIONAL DOOR
120	3'-0" x 7'-0" x 1 3/4"	HM	HM	B	A	SET 2	
121	9'-0" x 10'-0" x 2"	STEEL		C			OVERHEAD SECTIONAL DOOR
122	9'-0" x 10'-0" x 2"	STEEL		C			OVERHEAD SECTIONAL DOOR
123	9'-0" x 10'-0" x 2"	STEEL		C			OVERHEAD SECTIONAL DOOR
124	9'-0" x 10'-0" x 2"	STEEL		C			OVERHEAD SECTIONAL DOOR
125	3'-0" x 7'-0" x 1 3/4"	HM	HM	B	A	SET 2	
126	9'-0" x 10'-0" x 2"	STEEL		C			OVERHEAD SECTIONAL DOOR
127	9'-0" x 10'-0" x 2"	STEEL		C			OVERHEAD SECTIONAL DOOR
128	9'-0" x 10'-0" x 2"	STEEL		C			OVERHEAD SECTIONAL DOOR
129	14'-0" x 16'-0" x 2"	STEEL		C			OVERHEAD SECTIONAL DOOR
130	3'-0" x 7'-0" x 1 3/4"	HM	HM	B	A	SET 2	
131	3'-0" x 7'-0" x 1 3/4"	HM	HM	B	A	SET 2	
132	3'-0" x 7'-0" x 1 3/4"	HM	HM	B	A	SET 2	
133	3'-0" x 7'-0" x 1 3/4"	HM	HM	B	A	SET 2	
200	3'-0" x 7'-0" x 1 3/4"	HM	HM	B	A	SET 5	
200A	3'-0" x 7'-0" x 1 3/4"	HM	HM	B	A	SET 4	45 MINUTE RATED
201	3'-0" x 7'-0" x 1 3/4"	HM	HM	B	A	SET 5	
201A	3'-0" x 7'-0" x 1 3/4"	HM	HM	B	A	SET 3	45 MINUTE RATED
203	3'-0" x 7'-0" x 1 3/4"	HM	HM	B	A	SET 6	
204	3'-0" x 7'-0" x 1 3/4"	HM	HM	B	A	SET 6	

DOOR SCHEDULE NOTES:
1. HARDWARE TO BE COMMERICAL GRADE, SCHLAGE OR APPROVED EQUAL.
2. ALL LOCKSETS TO BE CAPABLE OF RECEIVING BEST CYLINDER CORES.
3. COORDINATE DOOR KEYING WITH OWNER.
4. ALL CLOSERS TO BE HEAVY DUTY.
5. REFER TO OUTLINE SPECIFICATIONS FOR DOOR & FRAME REQUIREMENTS.
6. ALL PAINTED DOORS AND FRAMES TO BE SPRAY PAINTED.

DOOR TYPES

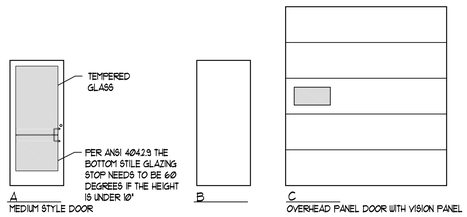

FRAME TYPES

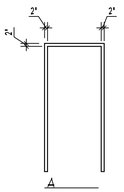

HARDWARE SETS

SET 1 (EXT STOREFRONT)
3 HINGES
1 OFFSET PULLS
1 CLOSER WITH OVERHEAD STOP
1 LATCH LOCK
1 CYLINDER
1 MANUAL CONCEALED VERTICAL ROD PANIC DEVICE
1 POWER TRANSFER
1 ELECTRIC STRIKE
1 THRESHOLD
1 SWEEP
WEATHERSTRIPPING

SET 2 (EXT ENTRY)
3 HINGES
1 STOREROOM LOCKSET
1 CLOSER WITH OVERHEAD STOP
1 THRESHOLD
1 SWEEP
1 RAIN DRIP CAP
WEATHERSTRIPPING

SET 3 (INT FP)
3 HINGES
1 STORAGE LOCKSET
1 CLOSER WITH OVERHEAD STOP
1 THRESHOLD SET IN SEALANT
SILENCERS
WEATHERSTRIPPING

SET 4 (INT-ELECTRICAL)
3 HINGES
1 PANIC BAR
1 DUMMY PULL KIT
1 CLOSER
1 WALL STOP
SILENCERS

SET 5 (EXT-UTILITY)
3 HINGES
1 PANIC BAR
1 STOREROOM LOCKSET
1 CLOSER WITH OVERHEAD STOP
1 THRESHOLD
1 SWEEP
1 RAIN DRIP CAP
WEATHERSTRIPPING

SET 5 (TOILET)
3 HINGES
1 PRIVACY LOCKSET
1 WALL STOP
1 CLOSER
1 KICKPLATE
SILENCERS
1 ADA SIGN

HARDWARE NOTES

1. VERIFY HARDWARE FUNCTIONS AND KEYING REQUIREMENTS WITH OWNER.
2. ALL DOOR HARDWARE TO COMPLY WITH ADA REQUIREMENTS AND AS DEFINED IN ANSI A-117.1.
3. DOOR HARDWARE SHALL BE CAPABLE OF OPERATION WITH THE USE OF ONE (1) HAND AND SHALL NOT REQUIRE TIGHT PINCHING, TIGHT GRASPING OR TWISTING OF THE WRIST TO OPERATE. THUMBTURN DEADBOLTS ARE PROHIBITED, LEVER OR PADDLE DEADBOLT RELEASES ARE ACCEPTABLE.
4. DOOR THRESHOLD SHALL NOT EXCEED ONE-HALF INCH (½") IN HEIGHT, THRESHOLDS EXCEEDING ONE QUARTER INCH (¼") IN HEIGHT SHALL HAVE A 1:2 BEVEL.
5. DOOR CLOSERS SHALL MEET OPENING FORCE AND SWEEP PERIOD REQUIREMENTS.
6. ALL ENTRY DOORS AND FIREWALL DOORS SHALL BE EQUIPPED WITH FINISH HARDWARE WHICH MEETS OR EXCEEDS THE REQUIREMENTS OF THE LOCAL CODES.
7. ALL REQUIRED ENTRY/ EXIT AND FIREWALL DOORS SHALL BE OPERABLE FROM THE INSIDE WITHOUT THE USE OF A KEY OR SPECIAL KNOWLEDGE.
8. SIGNS, IF REQUIRED, SHALL BE READILY VISIBLE AND DURABLE WITH LETTERS NOT LESS THAN ONE INCH HIGH ON A CONTRASTING BACKGROUND.
9. ACCESSIBLE TOILET ROOM SIGNAGE TO BE MOUNTED ON THE WALL ADJACENT TO THE LATCH SIDE OF THE DOOR WITH A MOUNTING HEIGHT OF 60" FROM THE FINISHED FLOOR TO THE CENTER OF THE SIGN.
10. PROVIDE KNURLED HANDLES ON EXTERIOR SIDE OF DOORS TO HAZARDOUS AREAS WHERE REQUIRED BY CODE.
11. DOORS AND FRAMES SHALL BE REINFORCED FOR SURFACE MOUNTED HARDWARE AS NECESSARY, DRILLING AND TAPPING FOR SURFACE MOUNTED HARDWARE SHALL BE PERFORMED BY INSTALLATION CONTRACTOR. PROVIDE PROPER DOOR REINFORCING TO ELIMINATE THE USE OF THRU-BOLTS.
12. ALL STANDARD TYPE HARDWARE WILL BE LOCATED AT THE MANUFACTURER'S STANDARD LOCATION AS SHOWN ON DOOR AND FRAME ELEVATION.
13. HARDWARE ITEMS SUCH AS PANIC EXIT DEVICES, DEADLOCKS, ETC. WILL ALSO BE LOCATED AT THE MANUFACTURER'S STANDARD LOCATION UNLESS SPECIFICALLY ADDRESSED IN SUBMITTAL AND/OR SUBMITTAL REVIEW.
14. ALL FRAMES SHALL BE PREPARED FOR DRILLED DOOR SILENCERS, THREE FOR SINGLE SWING OPENING AND TWO PER HEAD FOR DOUBLE SWING OPENINGS.
15. ALL FRAMES MUST BE SET PLUMB AND LEVEL TO ENSURE PROPER OPERATION OF DOORS AND HARDWARE.
16. FRAMES TO BE WELDED FULL DEPTH & WIDTH.
17. INSTALL DOOR CLOSERS ON NON-PUBLIC SIDE OF DOORS TO THE GREATEST EXTENT POSSIBLE.
18. DOOR SURFACES WITHIN 10" OF THE FLOOR OR GROUND SHALL BE SMOOTH AND EXTEND THE FULL WIDTH OF THE DOOR. PARTS CREATING HORIZONTAL OR VERTICAL JOINTS SHALL BE WITHIN 1/16" OF THE SAME PLANE. ANY CAVITIES CREATED BY ADDING A KICKPLATE SHALL BE CAPPED.
19. PROVIDE A THRESHOLD AND WEATHERSTRIP PACKAGE FOR ALL EXTERIOR DOORS INCLUDING COMPRESSIBLE GASKETS AROUND FRAME AND DOOR SWEEPS AT BOTTOM. PROVIDE MANUFACTURER'S STANDARD PACKAGE AT STOREFRONT DOORS AND PAIRS.
20. ALL EXTERIOR DOORS TO HAVE A RAIN CHANNEL CAP THE WIDTH OF THE DOOR + JAMBS COMBINED.
21. WHEN HOLLOW METAL IS USED IN CONJUNCTION WITH ALUMINUM OR STRUCTURAL STEEL PRODUCTS, CONSULT WITH THE CONSTRUCTION MANAGER FOR COORDINATION OF HARDWARE LOCATIONS.
22. WHERE DOORS OPEN BACK TO BACK, PROVIDE OVERHEAD STOP OR OTHER MEANS OF PREVENTING DOORS FROM DAMAGE.
23. PROVIDE HEAVYWEIGHT HINGES FOR DOORS OVER 3'-0" WIDE. USE A MINIMUM OF FOUR HINGES FOR DOORS OVER 7'-6" IN HEIGHT.
24. EXTERIOR HOLLOW METAL DOORS AND FRAMES TO BE GALVANIZED.
25. ALL CLOSERS TO BE HEAVY DUTY.
26. ALL PAINTED DOORS AND FRAMES TO BE SPRAY PAINTED.
27. REFER TO OUTLINE SPECIFICATIONS FOR ADDITIONAL HARDWARE AND DOCK EQUIPMENT REQUIREMENTS.

GLAZING NOTES

1. PROVIDE TEMPERED GLAZING AT THE FOLLOWING LOCATIONS (AND ANY OTHER LOCATIONS REQUIRED BY CODE):
   A. INGRESS AND MEANS OF EGRESS DOORS.
   B. FIXED PANELS IN SWINGING DOORS.
   C. INDIVIDUAL FIXED PANELS ADJACENT TO DOORS.
   D. FIXED PANELS WHOSE BOTTOM EDGE IS LESS THAN 18 INCHES FROM THE FLOOR.
   E. GLAZING IN GUARDS AND RAILINGS.
2. ALL GLAZING SHALL COMPLY WITH THE REQUIREMENTS OF THE LOCAL CODES.
3. ALL GLAZING IN OR ADJACENT TO DOORS OR IS WITHIN A 24" ARC OF EITHER VERTICAL EDGE OF THE DOOR IN A CLOSED POSITION SHALL BE TEMPERED.
4. PROVIDE TEMPERED GLAZING IN AN INDIVIDUAL FIXED OR OPERABLE PANEL WHEN ALL OF THE FOLLOWING CRITERIA APPLY. THE EXPOSED AREA OF AN INDIVIDUAL PANE IS GREATER THAN 9 SF., THE EXPOSED BOTTOM EDGE IS LESS THAN 18" ABOVE THE FLOOR, THE EXPOSED TOP EDGE IS GREATER THAN 36" ABOVE THE FLOOR AND ONE OR MORE WALKING SURFACE(S) ARE WITHIN 36" HORIZONTALLY FROM THE PLANE OF THE GLAZING.
5. FIELD VERIFY ALL ROUGH / FINISHED OPENING DIMENSIONS.
6. IF GLAZING IS IN AN INSULATED UNIT, BOTH LITES MUST BE TEMPERED, LAMINATED SAFETY GLASS, OR A COMBINATION OF THE TWO.
7. EXTERIOR STOREFRONT GLAZING AND DOORS TO HAVE 1" INSULATED GLASS, INTERIOR STOREFRONT GLAZING AND DOORS TO HAVE 1/4" SINGLE GLASS UNLESS NOTED OTHERWISE.

© 2026 Partners in Design Architects, Inc.

REVISIONS
1 05.20.26 SITE 1 OPERATIONAL RESUBMITTAL
2 05.26.26 SITE 1 OPERATIONAL COMMENTS
3 07.24.26 SUBMITTAL #4
4 09.22.26 SITE 1 OPERATIONAL CONDITIONAL APPROVAL SET


ZILBER INDUSTRIAL 3
108th St, Lakeview Corporate Park, Pleasant Prairie, WI

SCHEDULES & NOTES

2610 Lake Cook Road
Suite 280
Riverwoods, IL 60015
Ph.: (847) 940-0300
www.pidarchitects.com


Partners in Design ARCHITECTS

PROJECT NO.: 522.22.031
DRAWN BY: JJH
CHECKED BY: WHB
DATE: 08.12.22
SHEET NO.: A3.5

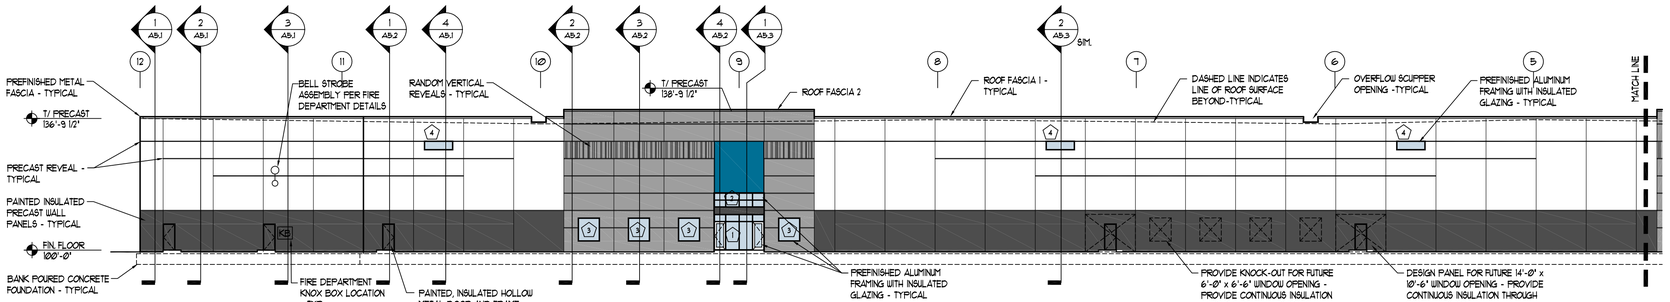


1 A4.1 NORTH ELEVATION 1" = 20'-0"


MAN DOOR NUMBERING STARTS AT '1' AT THIS MAN DOOR, INCREASE IN NUMBERS CLOCKWISE AROUND THE BUILDING FROM HERE

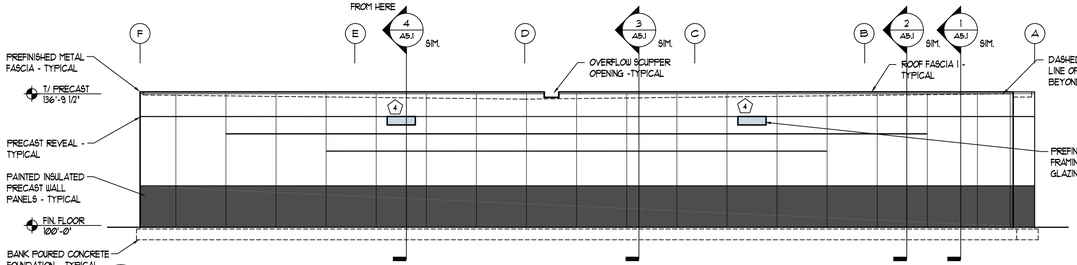


2 A4.1 EAST ELEVATION 1" = 20'-0"

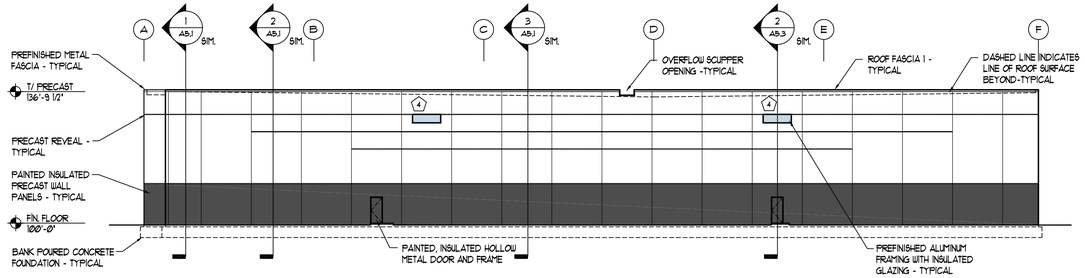


3 A4.1 WEST ELEVATION 1" = 20'-0"

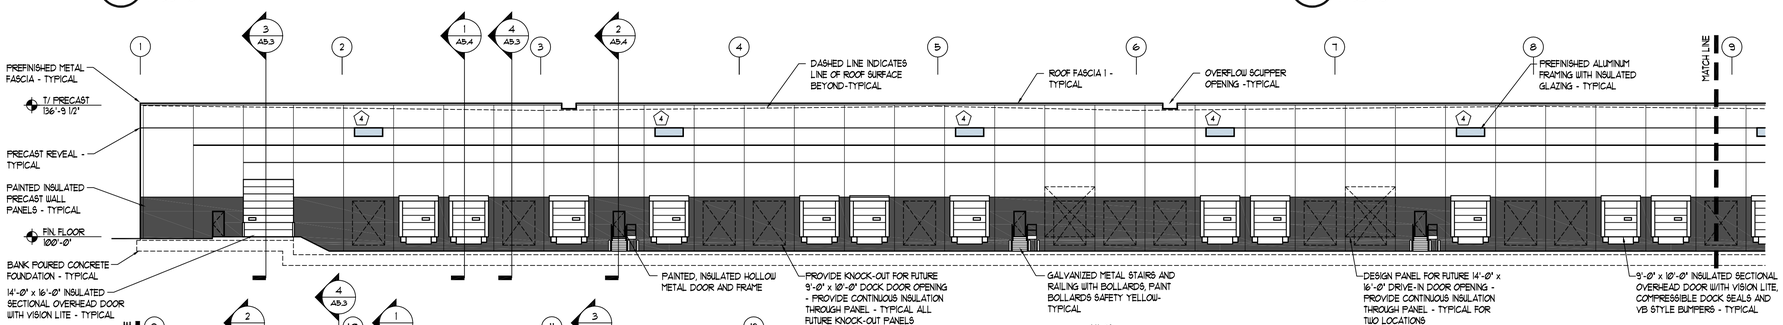

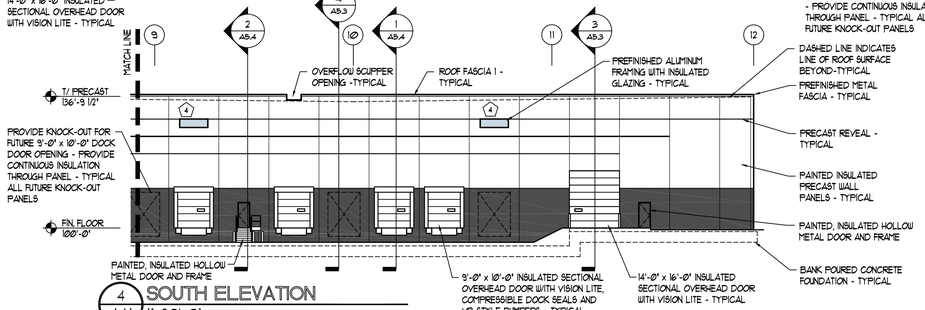


4 A4.1 SOUTH ELEVATION 1" = 20'-0"

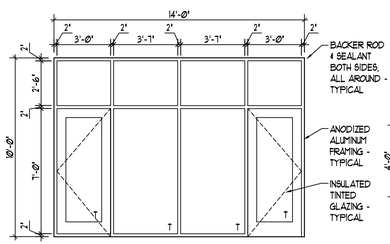


5 A4.1 TYPE 1 FRAME ELEV. 1/4" = 1'-0"


T = TEMPERED GLAZING

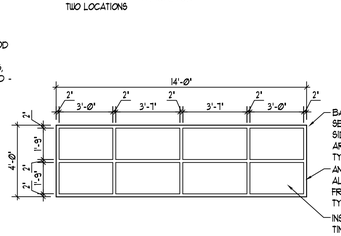

6 A4.1 TYPE 2 FRAME ELEV. 1/4" = 1'-0"

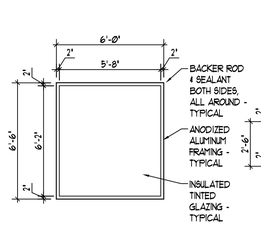

7 A4.1 TYPE 3 FRAME ELEV. 1/4" = 1'-0"

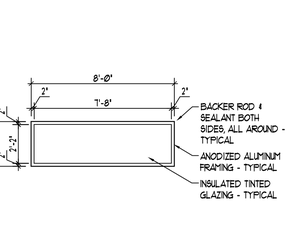

8 A4.1 TYPE 4 FRAME ELEV. 1/4" = 1'-0"

EXTERIOR FINISHES:

PAINT COLORS:

- COLOR 1 (LIGHT FIELD COLOR) SHERWIN-WILLIAMS COLOR: SW7064 PASSIVE
- COLOR 2 (DARK ACCENT COLOR) SHERWIN-WILLIAMS COLOR: SW7066 GRAY MATTERS
- COLOR 3 (DARK BASE COLOR) SHERWIN-WILLIAMS COLOR: SW7067 CITYSCAPE
- COLOR 4 (ACCENT COLOR) SHERWIN-WILLIAMS COLOR: SW6511 REGATTA
- ROOF FASCIA 1: FIRESTONE COLOR: STONE WHITE
- ROOF FASCIA 2: FIRESTONE COLOR: CITYSCAPE
- INSULATED TINTED GLASS: COLOR GREY

WINDOW FRAMES: CLEAR ANODIZED ALUMINUM

OVERHEAD DOORS: PREFINISHED ALUMINUM, WHITE

EXTERIOR STAIRS: GALVANIZED STAIRS & RAILINGS

© 2026 Partners in Design Architects, Inc.


REVISIONS
- 03.20.26 SITE 1 OPERATIONAL RESUBMITTAL
- 05.1.26 SITE 1 OPERATIONAL COMMENTS
- 07.24.26 SUBMITTAL #4
- 09.22.26 SITE 1 OPERATIONAL CONDITIONAL APPROVAL SET

ZILBER INDUSTRIAL 3
108th St, Lakeview Corporate Park, Pleasant Prairie, WI


EXTERIOR ELEVATIONS & FRAME TYPES

Partners in Design ARCHITECTS
2610 Lake Cook Road Suite 280 Riverwoods, IL 60015
Ph.: (847) 940-0300 www.pidarchitects.com


PROJECT NO.: 522.22.031
DRAWN BY: CTS CHECKED BY: WHB
DATE: 08.12.22
SHEET NO.: A4.1

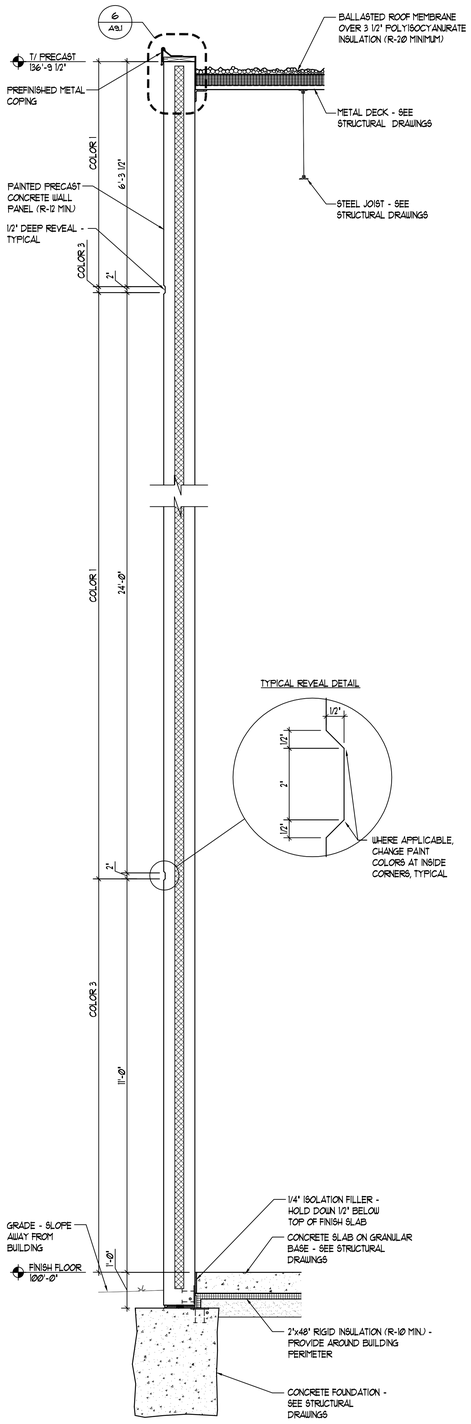


1 A5.1 **WALL SECTION**
1/2" = 1'-0"

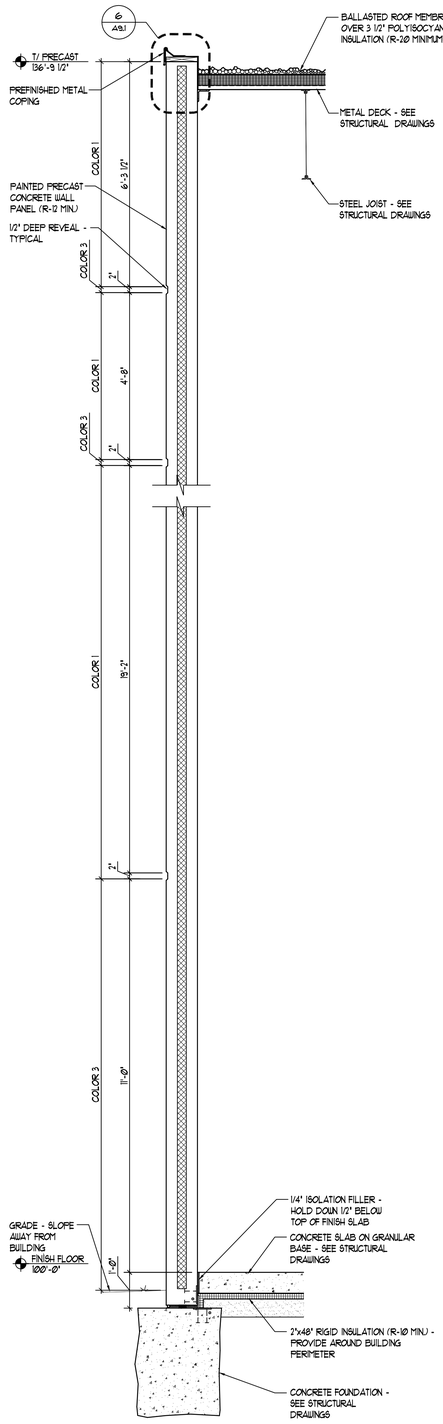

2 A5.1 **WALL SECTION**
1/2" = 1'-0"

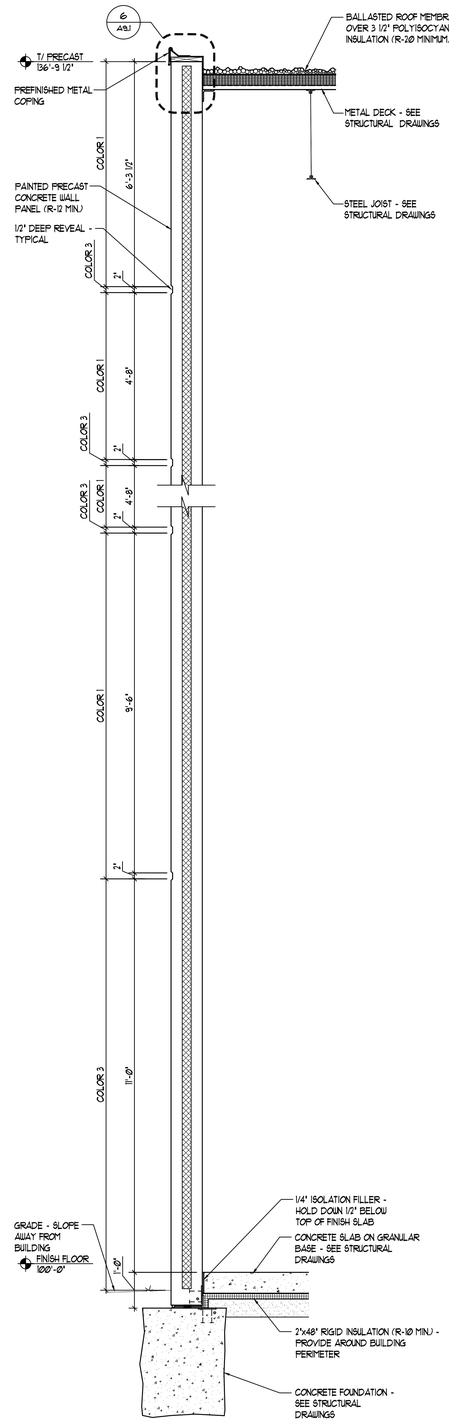

3 A5.1 **WALL SECTION**
1/2" = 1'-0"

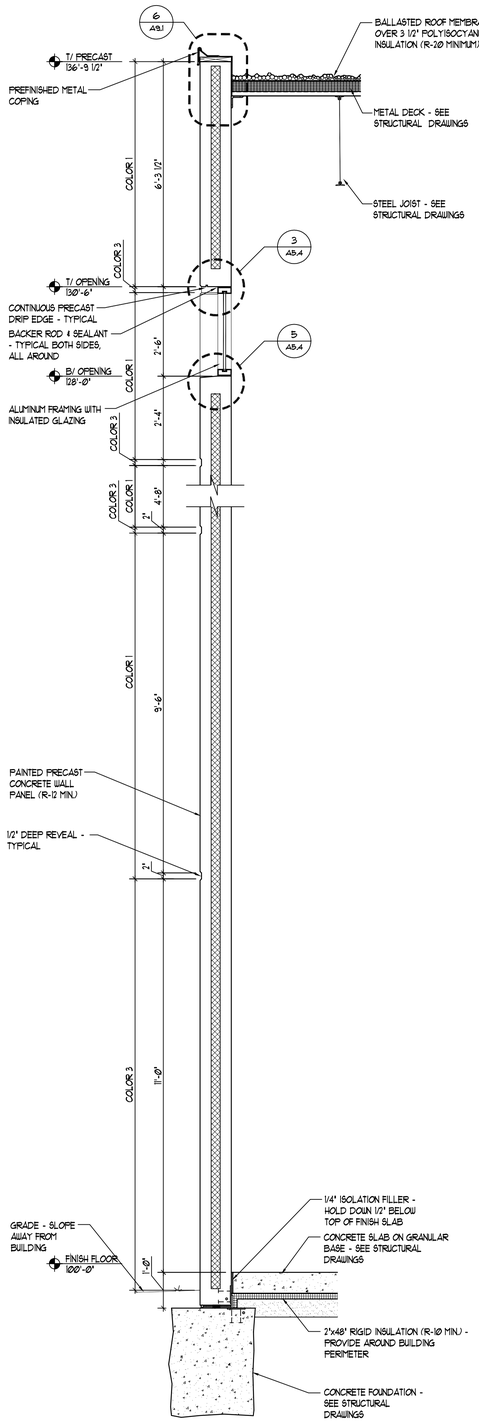

4 A5.1 **WALL SECTION**
1/2" = 1'-0"

© 2026 Partners in Design Architects, Inc.

REVISIONS
1 05.20.26 SITE 1 OPERATIONAL RESUBMITTAL
2 05.26.26 SITE 1 OPERATIONAL COMMENTS
3 07.24.26 SUBMITTAL #4
4 09.22.26 SITE 1 OPERATIONAL CONDITIONAL APPROVAL SET


ZILBER INDUSTRIAL 3
108th St, Lakeview Corporate Park, Pleasant Prairie, WI

WALL SECTIONS


2610 Lake Cook Road
Suite 280
Riverwoods, IL 60015
Ph.: (847) 940-0300
www.pdarchitects.com

Partners in Design ARCHITECTS


PROJECT NO.: 522.22.031
DRAWN BY: CTS
CHECKED BY: WHB
DATE: 08.12.22
SHEET NO.: A5.1

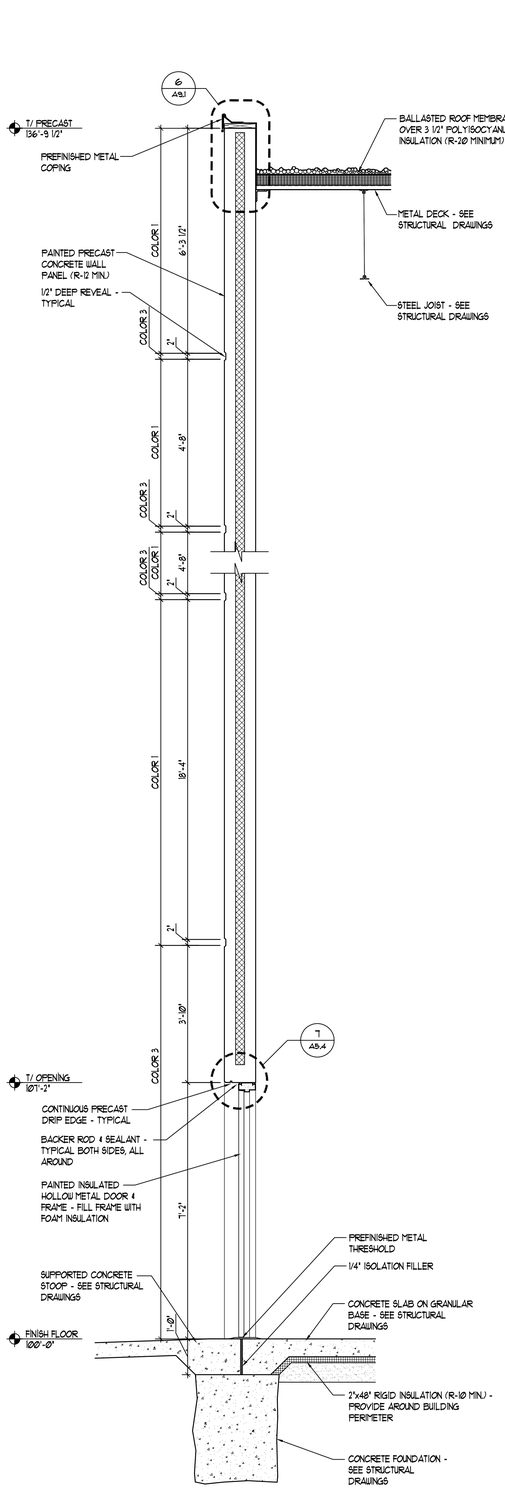


1 A5.2 WALL SECTION
1/2" = 1'-0"

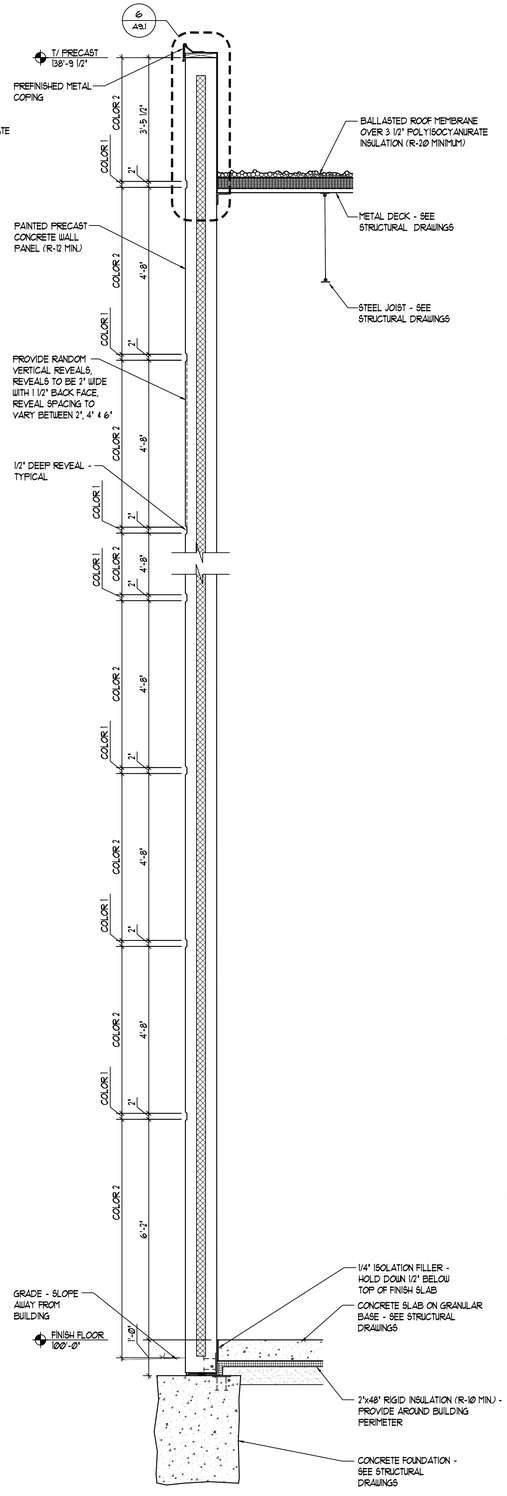

2 A5.2 WALL SECTION
1/2" = 1'-0"

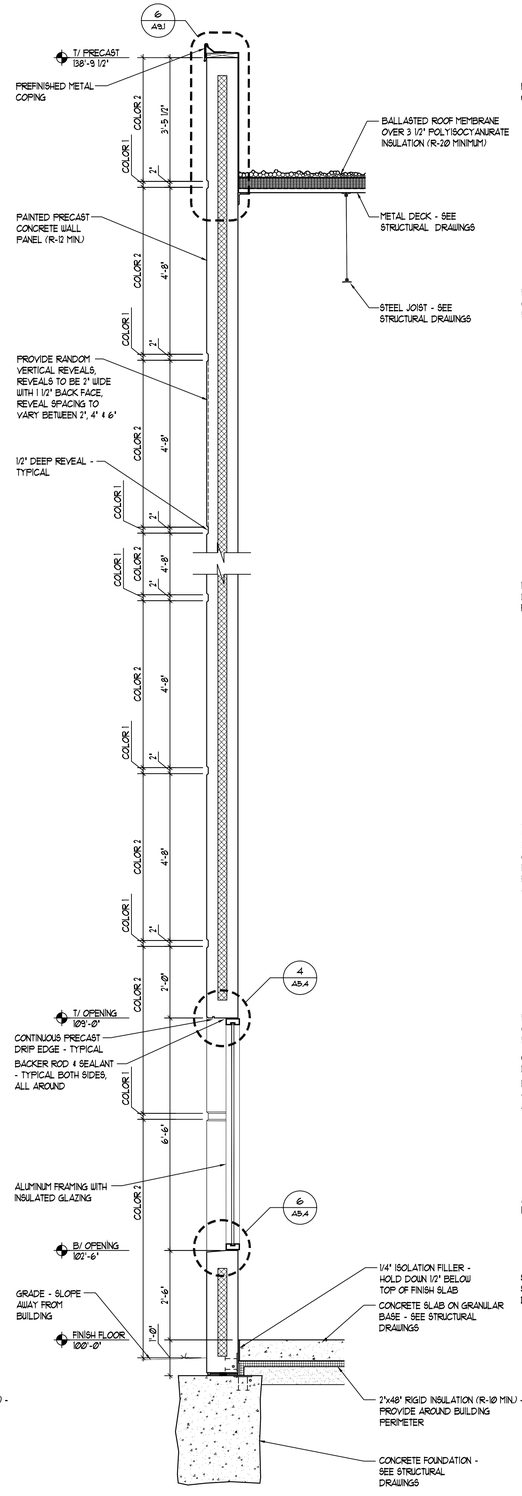

3 A5.2 WALL SECTION
1/2" = 1'-0"

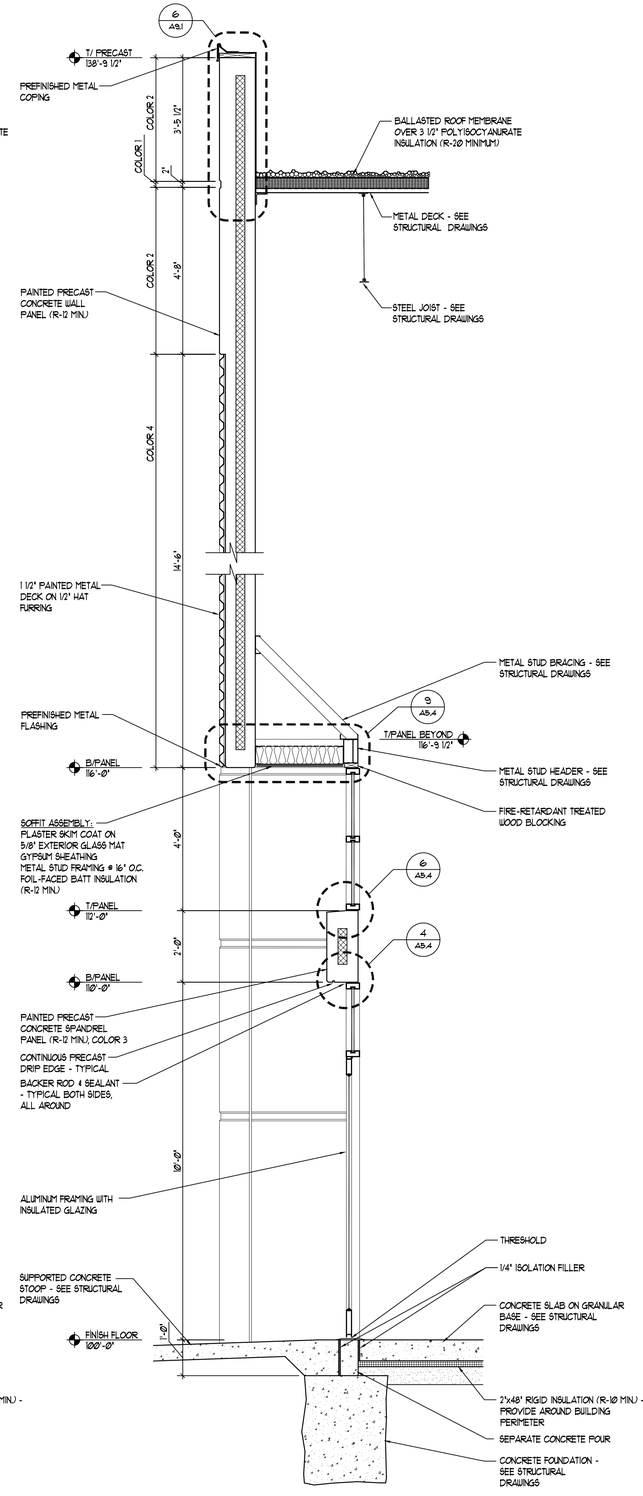

4 A5.2 WALL SECTION
1/2" = 1'-0"

© 2026 Partners in Design Architects, Inc.

REVISIONS
1 05.12.26 SITE 1 OPERATIONAL RESUBMITTAL
2 05.1.26 SITE 1 OPERATIONAL COMMENTS
3 07.24.26 SUBMITTAL #4
4 09.22.26 SITE 1 OPERATIONAL CONDITIONAL APPROVAL SET


ZILBER INDUSTRIAL 3
108th St, Lakeview Corporate Park, Pleasant Prairie, WI

WALL SECTIONS


2510 Lake Cook Road
Suite 280
Riverwoods, IL 60015
Ph.: (847) 940-0300
www.pidarchitects.com

Partners in Design ARCHITECTS


PROJECT NO.: 522.22.031
DRAWN BY: CTS
CHECKED BY: WHB
DATE: 08.12.22
SHEET NO.: A5.2

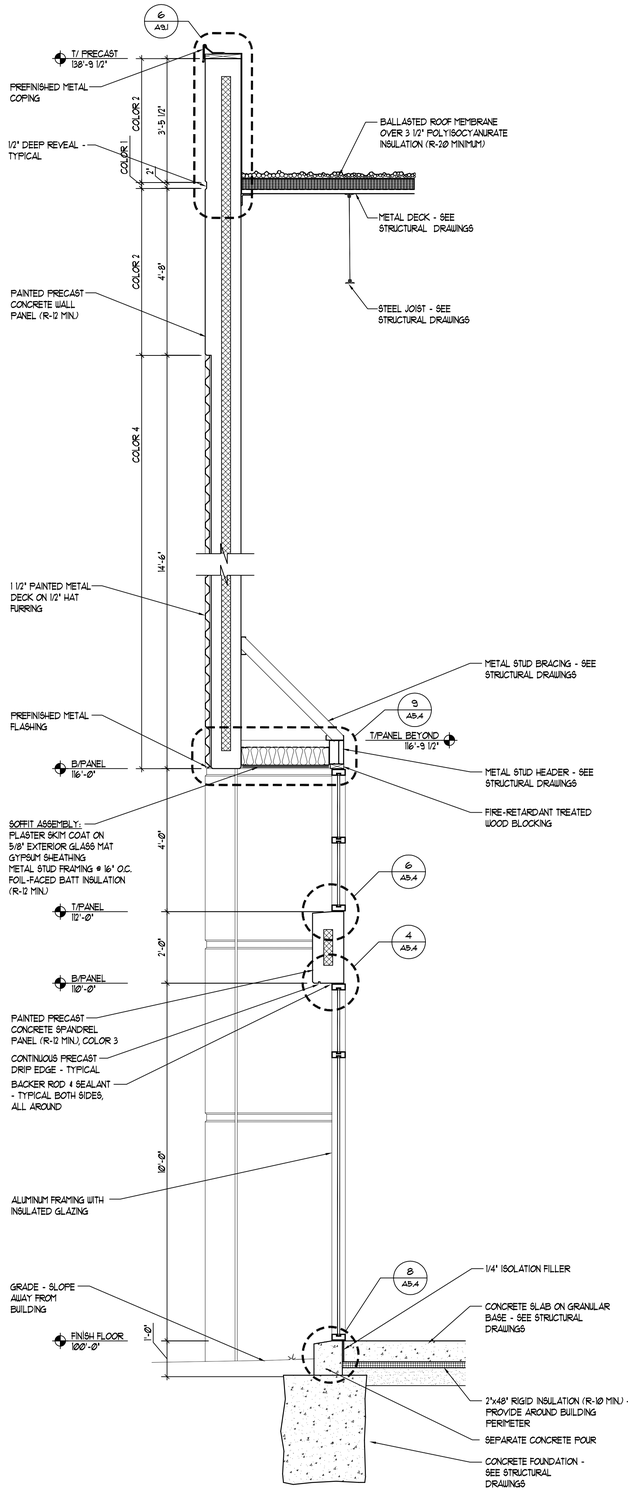


1 A5.3 **WALL SECTION** 1/2" = 1'-0"

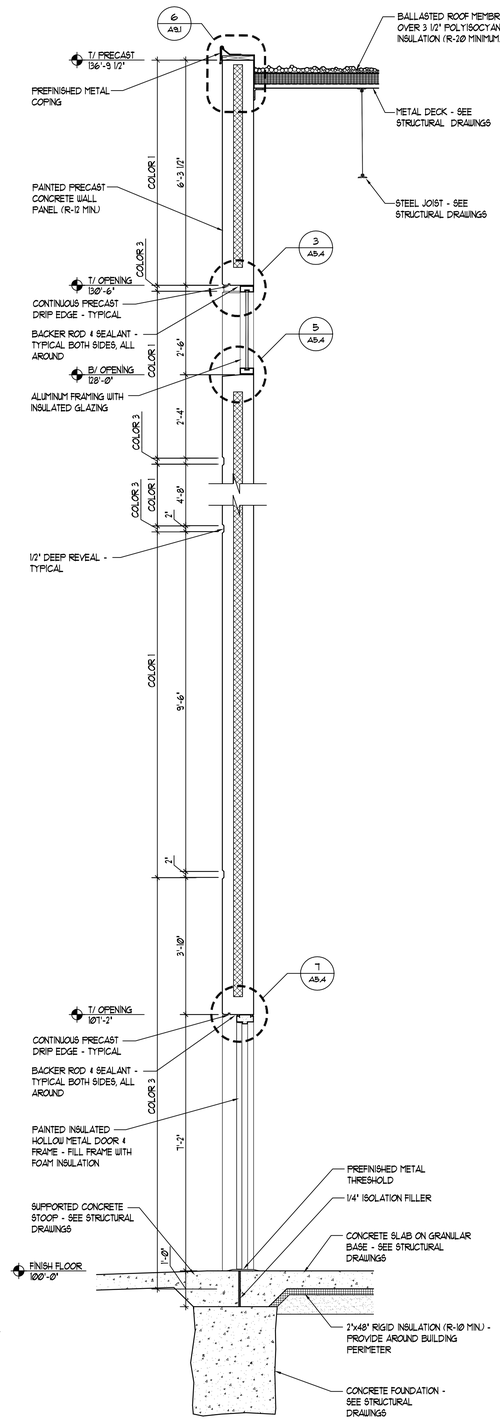

2 A5.3 **WALL SECTION** 1/2" = 1'-0"

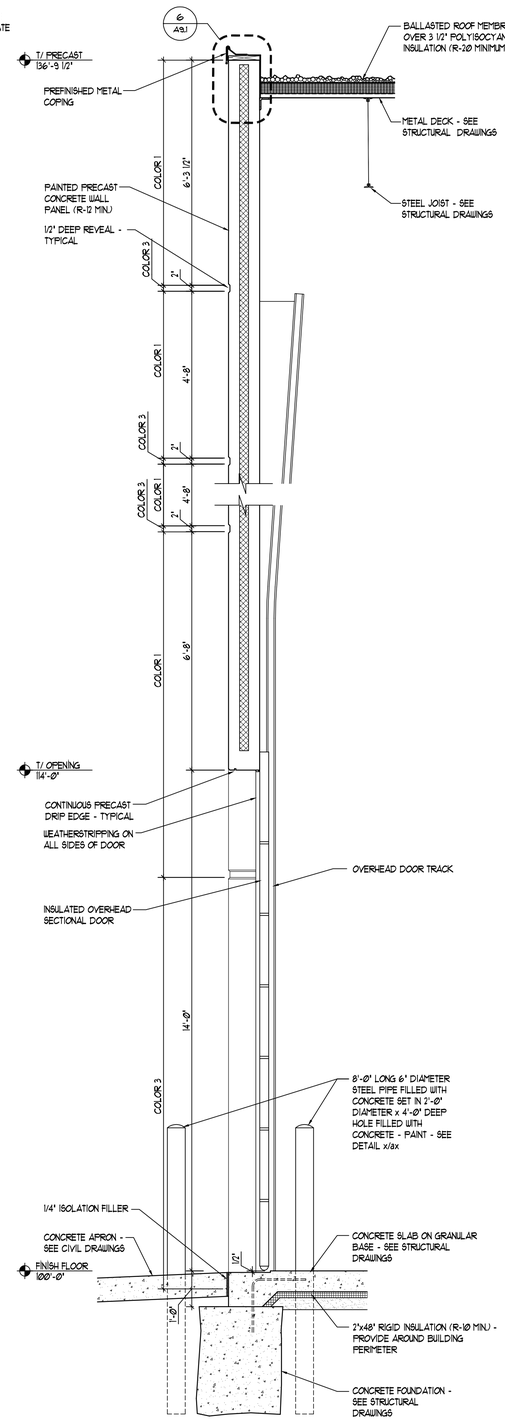

3 A5.3 **WALL SECTION** 1/2" = 1'-0"

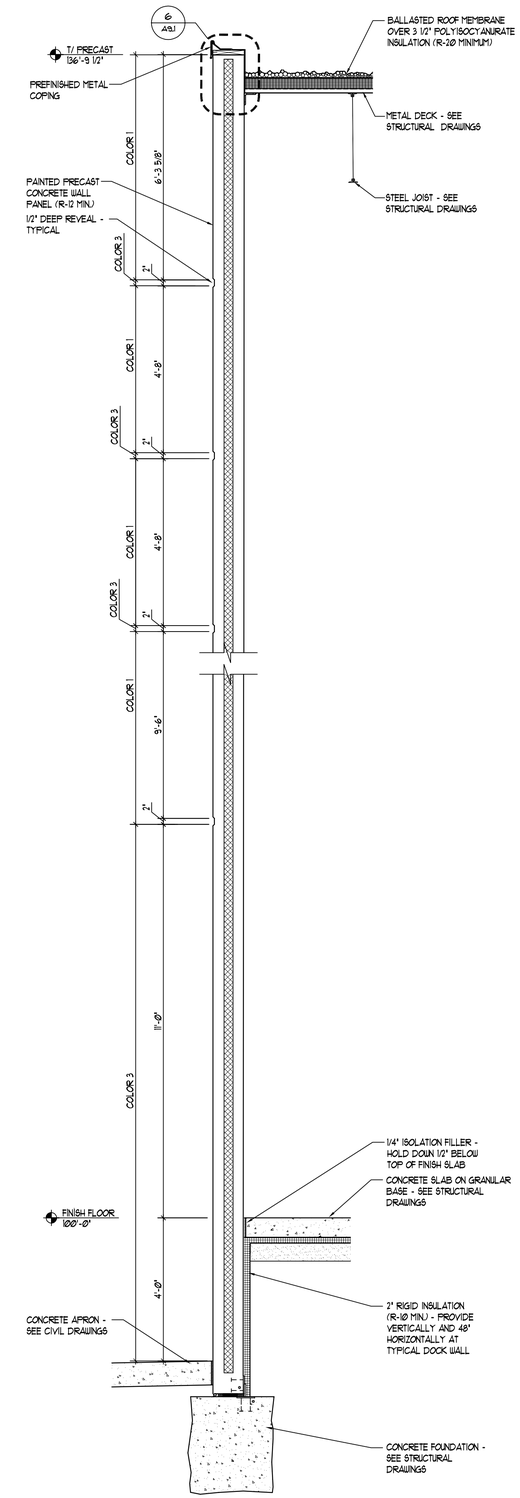

4 A5.3 **WALL SECTION** 1/2" = 1'-0"

© 2026 Partners in Design Architects, Inc.

REVISIONS
1 05.20.26 SITE & OPERATIONAL RESIDENTIAL
2 05.26.26 SITE & OPERATIONAL COMMENTS
3 07.24.26 SUBMITTAL #4
4 09.22.26 SITE & OPERATIONAL CONDITIONAL APPROVAL SET


ZILBER INDUSTRIAL 3
108th St, Lakeview Corporate Park, Pleasant Prairie, WI

WALL SECTIONS


2610 Lake Cook Road
Suite 280
Riverwoods, IL 60015
Ph.: (847) 940-0300
www.pidarchitects.com

Partners in Design ARCHITECTS


PROJECT NO.: 522.22.031
DRAWN BY: CTS
CHECKED BY: WHB
DATE: 08.12.22
SHEET NO.: A5.3

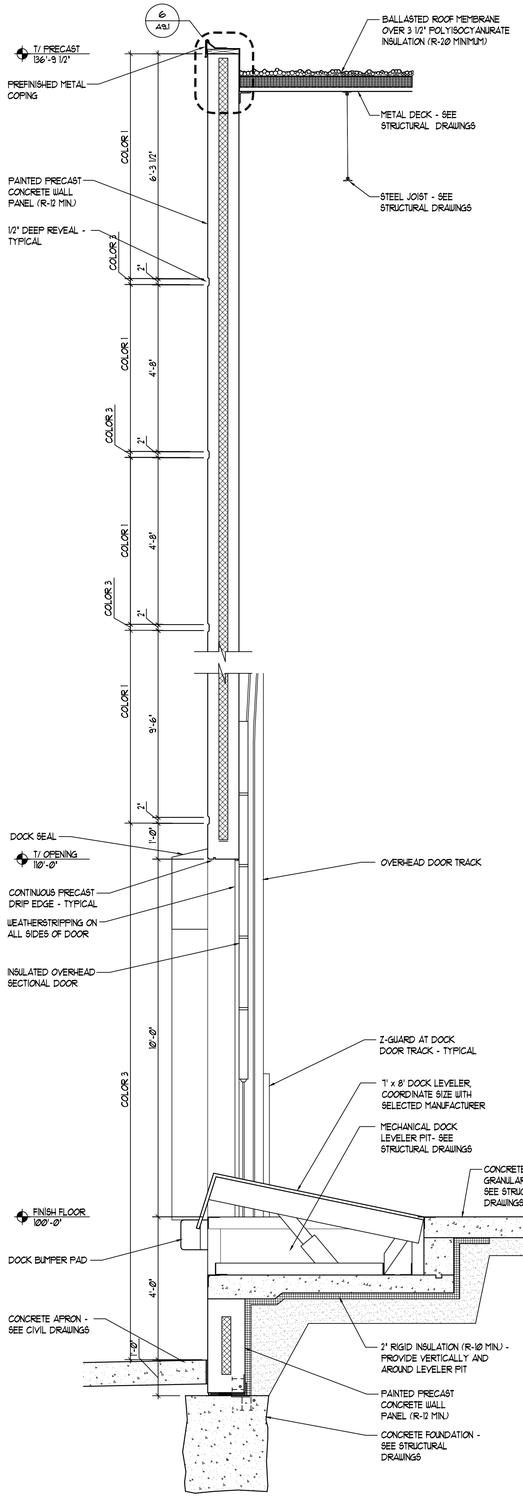


1 A5.4 **WALL SECTION**
1/2" = 1'-0"

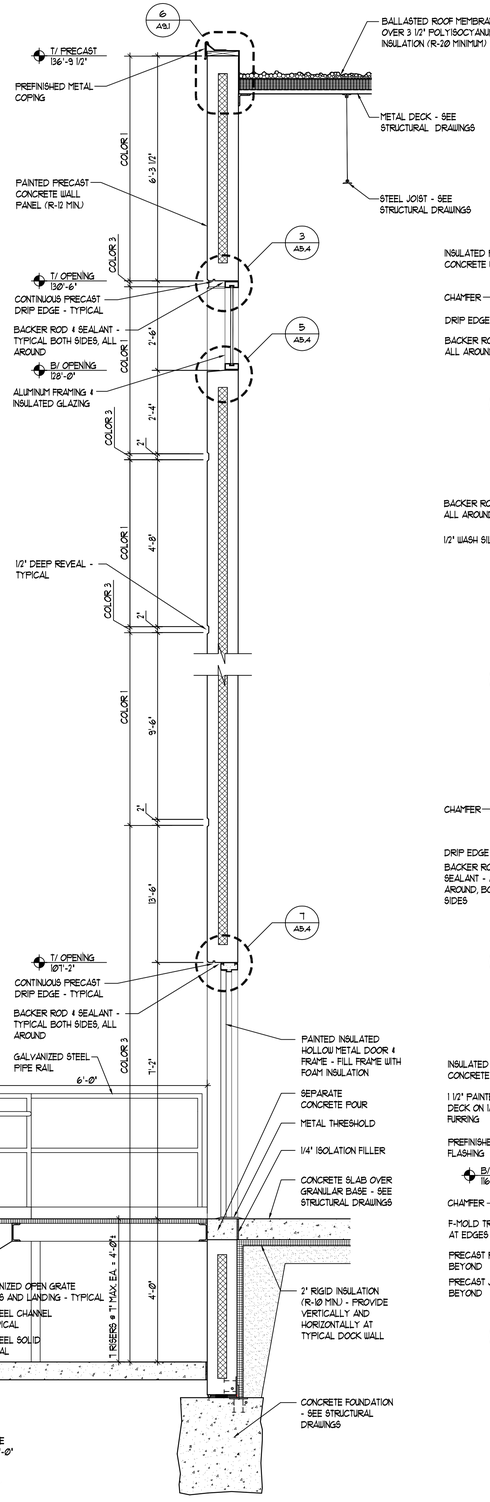


2 A5.4 **WALL SECTION**
1/2" = 1'-0"

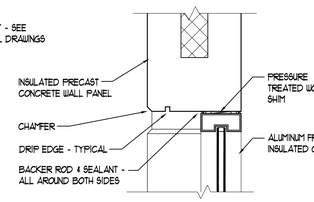


3 A5.4 **SECTION DETAIL**
1 1/2" = 1'-0"

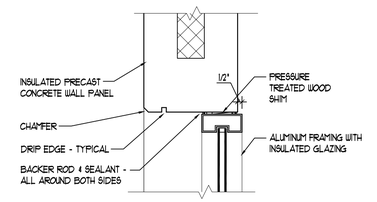


4 A5.4 **SECTION DETAIL**
1 1/2" = 1'-0"

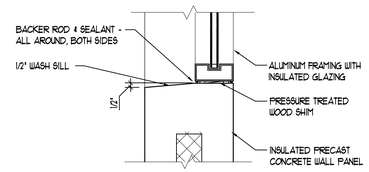


5 A5.4 **SECTION DETAIL**
1 1/2" = 1'-0"

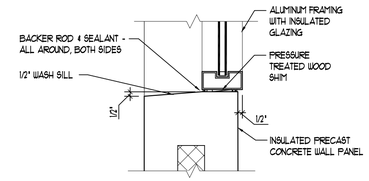


6 A5.4 **SECTION DETAIL**
1 1/2" = 1'-0"

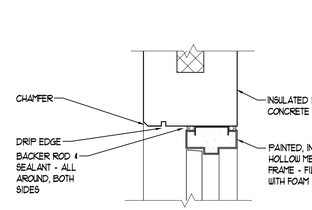

7 A5.4 **SECTION DETAIL**
1 1/2" = 1'-0"

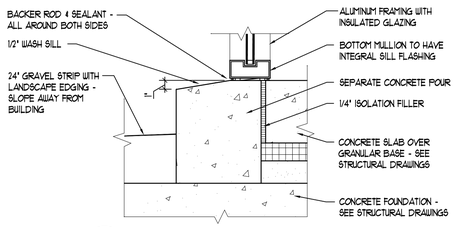

8 A5.4 **SECTION DETAIL**
1 1/2" = 1'-0"

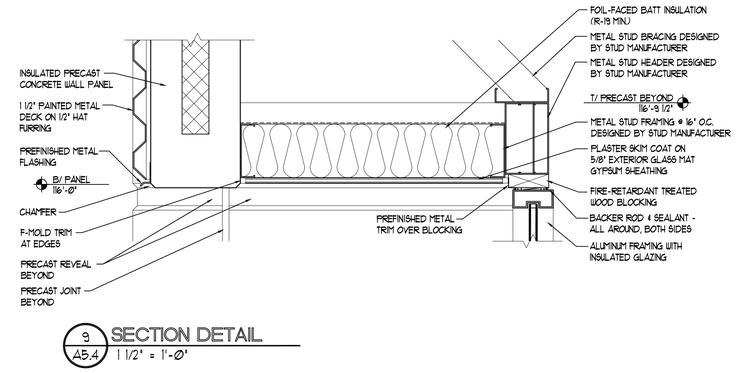

9 A5.4 **SECTION DETAIL**
1 1/2" = 1'-0"

© 2026 Partners in Design Architects, Inc.

REVISIONS
1 05.20.26 SITE 1 OPERATIONAL RESUBMITTAL
2 05.1.26 SITE 1 OPERATIONAL COMMENTS
3 07.24.26 SUBMITTAL #4
02.27.26 SITE 1 OPERATIONAL CONDITIONAL APPROVAL SET


ZILBER INDUSTRIAL 3
108th St, Lakeview Corporate Park, Pleasant Prairie, WI

WALL SECTIONS & SECTION DETAILS

2610 Lake Cook Road
Suite 280
Riverwoods, IL 60015
Ph.: (847) 940-0300
www.pdarchitects.com


Partners in Design ARCHITECTS

PROJECT NO.: 522.22.031
DRAWN BY: CTS
CHECKED BY: WHB
DATE: 08.12.22
SHEET NO.: A5.4

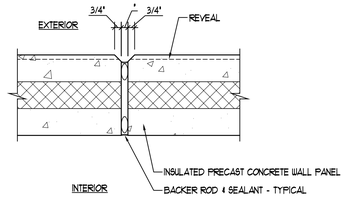


* - JOINT DIMENSION BY PRECASTER

1 A6.1 TYP. WALL PANEL JOINT DETAIL
1 1/2" = 1'-0"

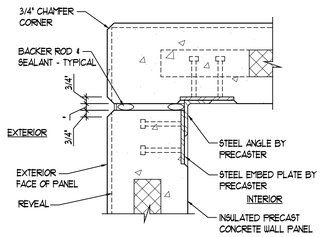


* - JOINT DIMENSION BY PRECASTER

2 A6.1 PRECAST BUTT CORNER DETAIL
1 1/2" = 1'-0"

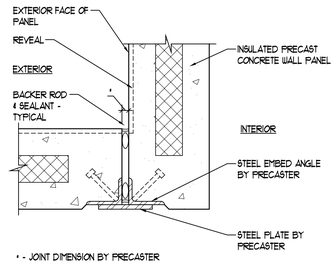


* - JOINT DIMENSION BY PRECASTER

3 A6.1 PRECAST BUTT CORNER DETAIL
1 1/2" = 1'-0"

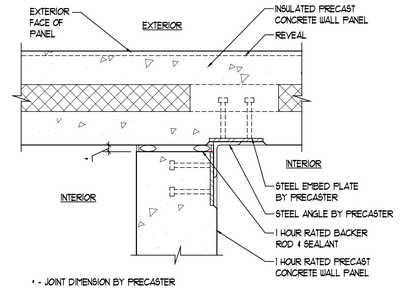


* - JOINT DIMENSION BY PRECASTER

4 A6.1 INTERIOR PRECAST DETAIL
1 1/2" = 1'-0"

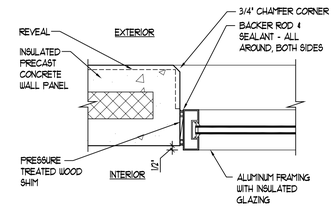


5 A6.1 WINDOW JAMB DETAIL
1 1/2" = 1'-0"

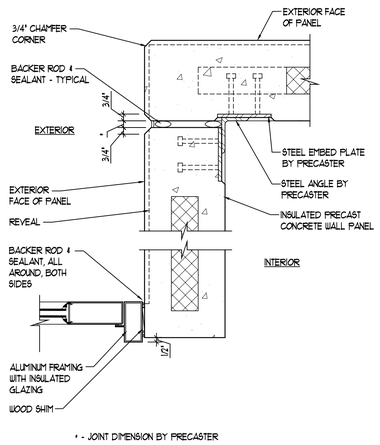


* - JOINT DIMENSION BY PRECASTER


6 A6.1 CORNER DETAIL
1 1/2" = 1'-0"

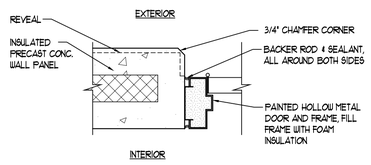


7 A6.1 DOOR JAMB DETAIL
1 1/2" = 1'-0"

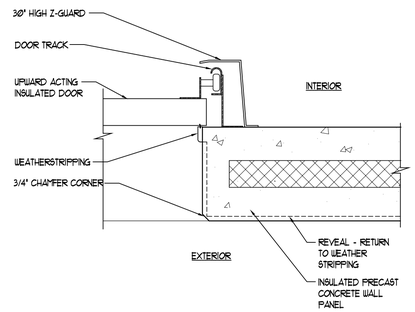

8 A6.1 DOCK DOOR JAMB DETAIL
1 1/2" = 1'-0"

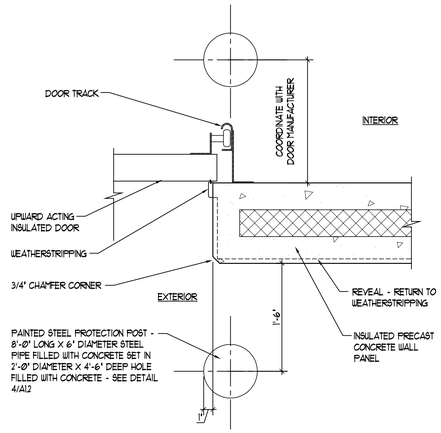

9 A6.1 DRIVE-IN DOOR JAMB DETAIL
1 1/2" = 1'-0"

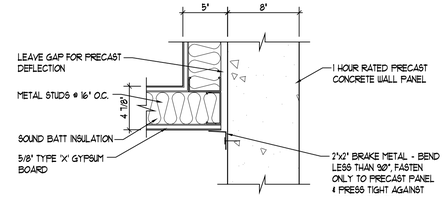

10 A6.1 GYP. BD. TO PRECAST DETAIL
1 1/2" = 1'-0"

© 2026 Partners in Design Architects, Inc.

REVISIONS
- 05.20.26 SITE & OPERATIONAL RESUBMITTAL
- 05.26.26 SITE & OPERATIONAL COMMENTS
- 07.24.26 SUBMITTAL #4
- 09.22.26 SITE & OPERATIONAL CONDITIONAL APPROVAL SET


ZILBER INDUSTRIAL 3
108th St, Lakeview Corporate Park, Pleasant Prairie, WI

PLAN DETAILS

2610 Lake Cook Road
Suite 280
Riverwoods, IL 60015
Ph.: (847) 940-0300
www.pidarchitects.com

PartnersinDesign ARCHITECTS

PROJECT NO.: 522.22.031
DRAWN BY: CTS
CHECKED BY: WHB
DATE: 08.12.22
SHEET NO.: A6.1

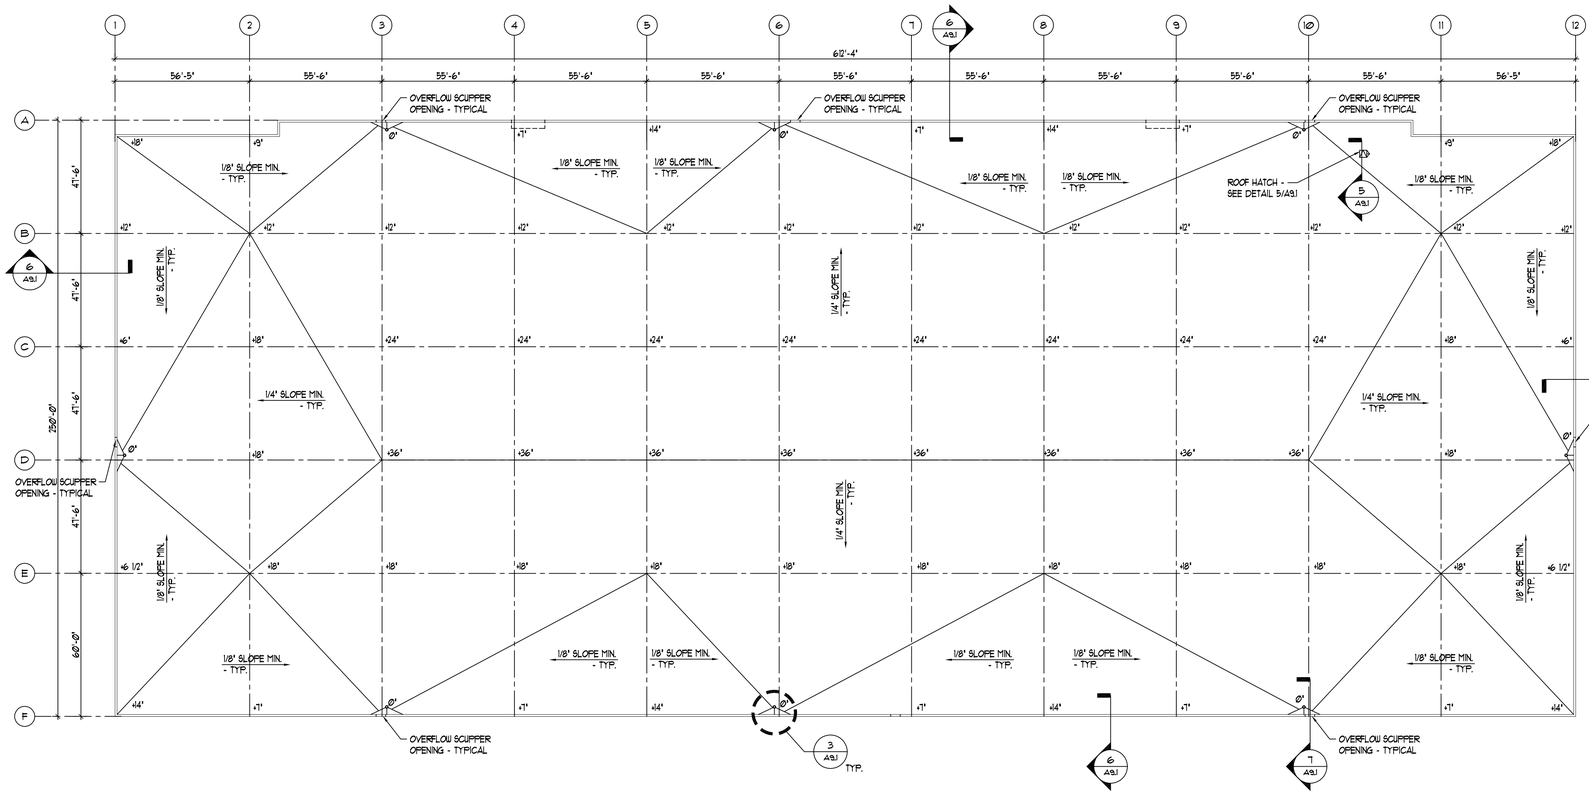


1 A9.1 ROOF PLAN
1" = 30'-0"

TRUE NORTH


PLAN NORTH

GENERAL ROOF NOTES

1. ALL ROOFING PRODUCTS AND MATERIALS TO BE INSTALLED PER MANUFACTURER'S PUBLISHED & WARRANTEED DETAILS.

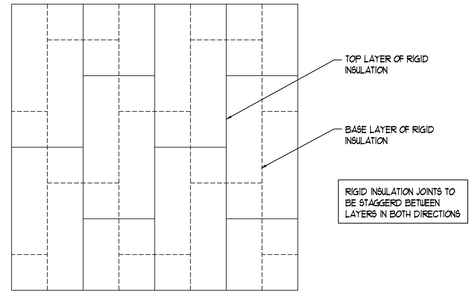


2 A9.1 ROOF INSULATION JOINT DIAGRAM

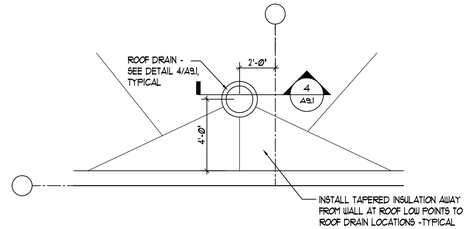


3 A9.1 ROOF DRAIN DETAIL
1/4" = 1'-0"

TRUE NORTH


PLAN NORTH

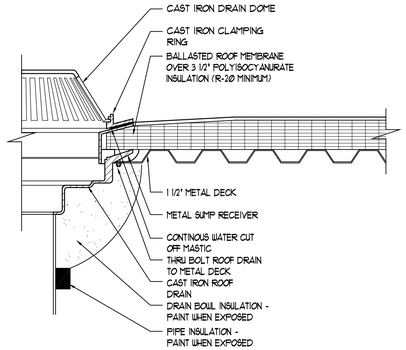


4 A9.1 ROOF DRAIN DETAIL
1 1/2" = 1'-0"

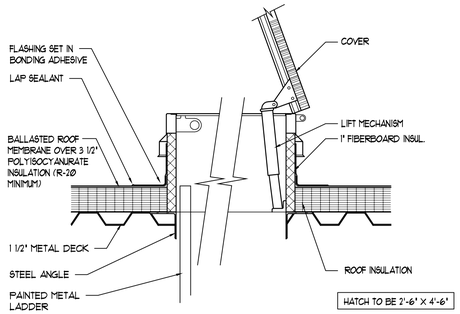

5 A9.1 ROOF HATCH DETAIL
1 1/2" = 1'-0"

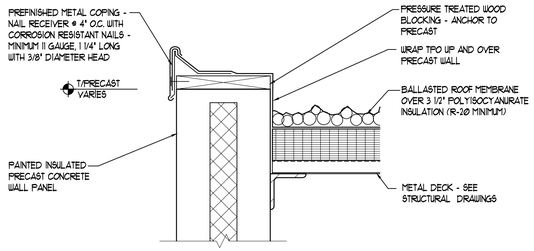

6 A9.1 ROOF EDGE DETAIL
1 1/2" = 1'-0"

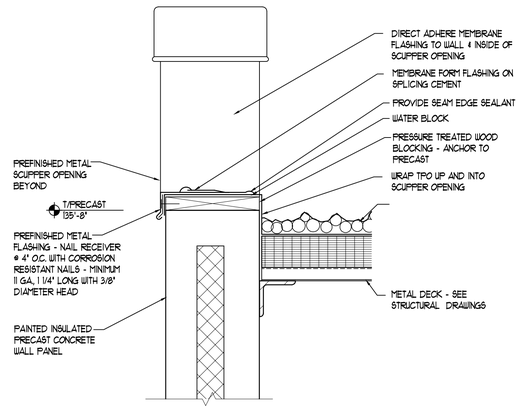

7 A9.1 ROOF EDGE DETAIL
1 1/2" = 1'-0"

© 2026 Partners in Design Architects, Inc.

REVISIONS
1 05.20.26 SITE 1 OPERATIONAL RESUBMITTAL
2 05.13.26 SITE 1 OPERATIONAL COMMENTS
3 07.24.26 SUBMITTAL #4
09.22.26 SITE 1 OPERATIONAL CONDITIONAL APPROVAL SET

ZILBER INDUSTRIAL 3
108th St, Lakeview Corporate Park, Pleasant Prairie, WI

ROOF PLAN & DETAILS

2610 Lake Cook Road
Suite 280
Riverwoods, IL 60015
Ph.: (847) 940-0300
www.pdarchitects.com

Partners in Design ARCHITECTS

PROJECT NO.: 522.22.031
DRAWN BY: JJH
CHECKED BY: WHB
DATE: 08.12.22
SHEET NO.: A9.1

Office of the Chief of Fire & Rescue
Craig Roepke

VILLAGE STAFF MEMORANDUM

TO: Rob Hanson, Community Development Director
CC: Peggy Herrick, Assistant Planner, Community Development

FROM: Craig Roepke, Chief Fire & Rescue

SUBJECT: Fire Department Review of LakeView 3 Site and Op Plans

SMARTGov: DEV2208-006

DATE: April 10, 2026

These are Comments/Reviews for LakeView 3 Site and Op Plans

The Fire and Rescue Department is responsible for providing Fire & Rescue services and fire prevention inspections of this facility. Based on the information and plans submitted, the Fire & Rescue Department have the following comments regarding the project:

1. The project will require an automatic fire sprinkler system. The system to be built in a similar fashion as shown on the markup sheet and as discussed in the April 2 meeting with the AHJ.
2. The project will require a fire alarm notification and detection system.
3. The FDC/ pumper pad to be located as depicted in the attached markup drawing including a setback as noted.
4. Village Engineering staff have discussed the placement of a hydrant fed from the Highway 31 main to extend to the Southeast as shown. This will be considered a private hydrant.
5. Fire Hose valves are required at all man doors including office entrances.
6. As discussed, the exterior yard hydrants will be fed from an interior looped system with control valves operable from the ground level.
7. Some form of "No blocking fire room or pump room access" to be discussed for the dead-end East roadway leading to the fire pump room.
8. See Fire alarm pull station details regarding "No glass rod" pulls.
9. Any tenant occupancy after spec building approval, requires additional review.

10165 Terwall Terrace • Pleasant Prairie, Wisconsin 53158-5643 • Phone 262.948.8975 • Fax 262.697.1901 • pleasantprairiewi.gov

Responsibility to Distribute this document: the person(s) who obtains the relevant permit is responsible to distribute to all contractors and subcontractors affected by this document. This document outlines critical times and deadlines. All recipients of this document must become familiar with the contents.

AHJ: The Authority Having Jurisdiction is the Village of Pleasant Prairie Fire & Rescue Department.

Planned Unit Development: Should this project fall under a zoning PUD agreement or other negotiated provisions by the Village of Pleasant Prairie, these comments and requirements may supersede and be more stringent than other State or building related rules or code sets.

Verbal Discussion: Any verbal discussions regarding variations to the comments within this document shall be confirmed in writing by both the AHJ and the responsible agent. Failure to secure written confirmation shall invalidate any verbal variance or discussion.

Conflicts: In the event a conflict in code(s) is identified, or a conflict with the insurance carrier criteria occurs, the more stringent shall apply. In the event this conflicts with any codes adopted by the State of Wisconsin, the owner must petition the State directly for a variance. The Owner must demonstrate that they will provide materials or design equivalent to the code or that they will exceed the code when petitioning the State of Wisconsin and/or the Village of Pleasant Prairie where applicable.

Fire Safety System Plans: such as fire sprinkler and fire alarm plans, will need to be submitted to the State of Wisconsin Department of Safety and Professional Services and also to this AHJ for review. No installation of any fire protection or system is allowed until a satisfactory review is obtained from both departments.

FIRE ALARM AND SPRINKLER PLANS ARE A SEPARATE SUBMITTAL TO THE FIRE DEPARTMENT. FIRE PROTECTION SUBMITTALS SHALL BE BROKEN INTO AN UNDERGROUND SUBMITTAL AND AN ABOVE GROUND SUBMITTAL. THESE SUBMITTALS MAY BE SUBMITTED SIMULTANEOUSLY AS ONE PACKET.

Pre-Construction Meeting: A pre-construction meeting may take place with the general contractor, the fire protection contractor, the Fire and Rescue Department, Village staff, and any other sub-contractor prior to the start of any project construction.

1. **Contact Information:** For questions on the information and comments included within this document please use the following information:

   Pleasant Prairie Fire & Rescue Department
   10165 Terwall Terrace
   Pleasant Prairie, WI 53158
   262.948.8975
   manshus@pleasantprairiewi.gov
   Attn: Mike Anshus – Fire Inspector

   Website: https://pleasantprairiewi.gov/departments/fire_rescue

2. **Site Access:**
   a. All entrances from public streets, as well as road and driveways around the proposed building shall be a minimum of 30 feet wide or as otherwise agreed upon.
   b. All roadways and fire lanes shall be unobstructed and not used any part as a parking area for automobiles, semi-trucks or trailers. Fire lanes shall comprise of a hard and maintainable surface throughout all seasons.
   c. All exterior exit pathways as well as access to the Fire Pump or riser room shall have a hard surface, leading to a hard surface. This includes all exit doors from the facility. These pathways shall be maintained and accessible at all times.
   d. An exterior personnel door shall be located in close proximity to each fire sprinkler riser.
3. **Gates / Barriers:**
   a. Any gates or barriers that are employed or installed on a private roadway or access shall have a minimum width clearance of sixteen (16) feet. Builder/developer to identify any other gate widths and obtain written AHJ variance approval.
   b. Gates or barriers that are locked must have the ability for the AHJ to remove, unlock or disable either

manually or automatically the securing mechanism to open or raise the gate or barrier. Builder/developer to identify methodology of such mechanisms.

   c. Any barrier or gate that raises vertically at a pivot point to allow for passage must provide for at least 90 degrees of clearance from the ground to the bottom of the gate or barrier.
   d. Gates or barriers that raise vertically shall have a minimum vertical clearance of 13'6".
   e. There shall be a manufacture endorsed mechanism or process to secure the gate or barrier in the open position without utilizing personnel or ad-hoc methods to maintain an open condition.
   f. There shall be Knox padlocks, Knox key switches, or other AHJ approved devices on all gates on site. The Fire & Rescue Department will review the proper placement and operation of the Knox system locks & Boxes.
   g. The gate or barrier access on premise shall be readily identifiable and in contrast to fencing and reviewed by the AHJ.
   h. Based on the project details main access or emergency gates will likely require a "Click-to-Enter" system or similar; see website click2enter.net
4. **Combination Water Sizing Confirmation:** The owner shall provide a letter from the sprinkler designer affirming that the combination water main is sized appropriately for both domestic use and fire sprinkler protection demand. This will typically include the designer's license stamp on the document.
5. **Compliance:** A letter shall be submitted to the Fire & Rescue Department prior to receiving a building permit, stating that the project will comply with all requirements addressed within this document. This document shall be received prior to holding any pre-construction meeting.
6. **Required Licenses:** A Wisconsin licensed fire protection contractor and/or sprinkler fitter must install any and all dedicated fire protection underground fire mains and aboveground fire protection as defined in WI SPS 305 subchapter V
7. **Review and Comments:** the Fire Department will review and comment on the following areas outlined below.

   A. Site and Operational Permits
      1. Site accessibility (Plans provided do not specific clearances or distances)
      2. Fire Pump Location
      3. Pumper Pad
      4. Fire hydrant spacing

   B. Conditional Use and Operational
      1. Standpipe outlet locations
      2. Fire alarm pull station
      3. Emergency and Exit Lighting
      4. Fire extinguishers
8. **Plan Review, Permits and Fees**
   a. The plans for the fire protection underground, aboveground, fire alarm system, and/or special suppression systems shall be submitted to the AHJ for review.
   b. Underground fire piping and aboveground (Sprinklers) are split into separate reviews in the interest of time and construction.
   c. Electronic submittals are now in place. This will aide in reducing the time for approval notifications.
   d. The Village will use an independent fire safety consultant for review of all fire protection plans submitted.
      i. Standard review periods are 21 business days
      ii. Expedited reviews at 10 business days are available for an extra cost.
      iii. Plan review times begin the day after the plans are received by the contract reviewer.
   e. Contacting the third-party reviewer directly for submission is not allowed. Subsequent design

questions and clarification dialogue is permissible.

   f. An approved & stamped AHJ review must be completed before any permits will be issued and before construction may begin.
   g. A submittal is not considered permitted or an approved plan.
   h. Acquiring WI State approved plans is not an alternative to bypass the AHJ permitting process.
   i. A Building Department Low voltage permit shall also be secured by the fire alarm installer.
   j. Applications & assistance can be found at https://www.pleasantprairiewi.gov
9. **Permit fees & Submittals:** Submittals and reviews are required for other less common fire suppression systems as outlined below. Permit/submittal fees must be paid at time of submission for review. Work cannot begin until all permits have been issued AND have received AHJ stamped approval. A typical review turnaround is four weeks

   The following fees and permits are received directly to the Fire & Rescue Department.

   a. Fire Protection Plans for Underground and Aboveground
   b. Fire Alarm System Plans
   c. Kitchen (Ansul™ or similar) Hood Systems Plans
   d. Clean Agent systems such as HFC-125, Sapphire™ agents or similar

   NOTE: Permits are required from the Fire & Rescue Department for the installation of water main in addition to any permits required by other Village of Pleasant Prairie Departments.

10. **Occupancy:**
    a. All fire and life safety requirements shall be in place and operational prior to any building being occupied.
    b. No occupancy inspections shall be scheduled until all life-safety systems are complete.
    c. Key life safety systems include: Fire sprinkler system, Fire alarm system, Fire extinguishers, Emergency Lighting, and any additional requirements determined by both the Fire Department and/or the Village Building inspection department.
    d. AEDs as required are in place.
    e. Building access keys and related interior access methods must be in place.
11. **Hazardous Occupancies**: Should there be identified hazard occupancies with this project, the Fire & Rescue Department may need more than the typical four week time period to review potential Hazardous Occupancies. The owner must contact the Fire & Rescue Department as soon as possible to begin the review process.
12. **Exterior Doors:** All outside doors shall have access to the interior. Doors shall have a handle, knob or similar, to allow outside access. Doors shall incorporate a keyed lock even if there are electronic methods for access.
13. **AED:** The owner may be required to acquire and install one or more public access Automatic External Defibrillator (AED) onsite for employee and public use in the event of a sudden cardiac arrest. It is suggested that during the construction phase that a location(s) be identified so that options for recessed cabinets may be determined. Recessed cabinets for AEDs and any Bleed kit installations are highly preferred.
14. **Storage:** Maximum height, width and aisle ways and egress pathways must be maintained and will be enforced. The same concerns apply to the storage of quantities of combustibles (plastics and cardboard) and other storage of flammable liquids or chemicals must also be properly identified, placarded and stored.
15. **Severe Weather Shelter:** The architect shall identify the area within each building or structure that can be used as a "severe weather shelter" or "safe haven" during severe weather such as a tornado. That area will be identified with signage.
16. **Door Numbering:** Each exterior door shall be sequentially numbered.
    a. Shall consist of a 4" reflective number in a color that is contrasting to the door color.
    b. Numbering shall be in an increasing sequence and located in the upper right-hand portion of the

door.

   c. The starting numbering point shall be the front entrance or determined in the field and approved by the AHJ prior to completion.
   d. Door numbering shall also be identified on the interior on the upper corner of the Handle side.
   e. Other identification schemes may be permissible with prior review and AHJ approval.
17. **Door numbering – Internal:** in multi-unit residential dwelling buildings a numbering scheme shall be devised so that locations of a room are intuitively expected. Each room shall have a unique number assignment.
18. **On Premise Secure Key System:**
    a. Knox Company Rapid Entry System, "Knox Boxes" shall be provided for the building. The Knox Boxes shall be Model 4400, other models may be permissible with written AHJ approval.
    b. Knox Boxes are ordered through the AHJ.
    c. **Recessed mounted key boxes;** Wherever possible recessed key boxes should be utilized
    d. Two sets of all keys (Master, fire alarm pull station, annunciator, elevator, etc.) shall be placed within each installed box on premise. This includes key cards, FOBs or other electronic media used to access both interior and exterior doors. Key sets should be labelled and organized into two distinct ringed sets.
    e. Height of Knox Box is five (5) feet from finished ground to top of box. Review drawing cut sheet for specific details.
    f. Details on installation location can be found on the Village website or requested through the contact within this document.
    g. If this is an existing facility, the Knox Boxes should be adjusted to meet the current height installation requirement.
    h. Refer to the Project Supplement Guide for height and location installation.
19. **Fire Extinguishers:** Shall meet NFPA 10 (Portable Fire Extinguishers) for the specific use of the building and be in sufficient number. Final approval, of fire extinguisher locations and quantity, will not be given until occupancy is taken, to see how a tenant furnishes the space. The company providing the fire extinguishers shall submit a letter to the Fire and Rescue Department stating the locations and size of the extinguishers are in compliance with NFPA 10. Fire Extinguisher locations should be recessed into the wall whenever possible.
20. **Emergency and Exit Lighting:** Exit and Emergency Lighting shall be provided and shall have a backup methodology allowed by applicable codes. Combination EM/Exit units are acceptable. An emergency generator and transfer switch designed for such uses eliminates the need for EM lighting battery backup. These circuits shall be clearly labeled as applicable. Emergency lighting testing and photometrics shall be required and will also be reviewed by the Village building inspection department.
21. **Underground Fire Protection piping**: The general contractor and project owner have the overall responsibility to ensure that the fire underground piping is managed appropriately with proper elements completed below:
    a. Underground submittals to the AHJ. This also includes pumper pad FDC and hydrant details.
    b. As-built drawings are provided with nomenclature that depicts valve locations and their operations.
    c. Tracer wire as required by Code.
    d. The installation of dedicated underground fire protection piping is overseen by a WI licensed sprinkler installer that is on-site.
22. **Sprinkler System:**
    a. The building shall be equipped with an "automatic fire sprinkler system" . The systems shall be designed and constructed to the current relevant edition of *NFPA 13x, Automatic Fire Sprinklers and the Village of Pleasant Prairie Ordinance 180-16, Automatic Fire Sprinklers*. Confirm NFPA edition with the Fire Department prior to system design.

   b. Fire Risers shall be durably labeled with the system and/or riser identification. NFPA 13 [2016]25.5 & 25.6. Fire risers shall have their system number affixed to the vertical riser pipe in a contrasting color that is easily identified from a distance. Number sizes at minimum shall be 4 inches.
   c. Outside/exterior building Riser Control Valves: Where installed, outside control valves shall be durably labeled with the associated system or riser that it controls. Control valves shall be electrically monitored and/or locked as required by code.
   d. Outside yard valves such as PIVs or OS&Y valves shall be locked with chain and/or commercially breakable locks. Those keys shall also be made available and placed in the respective Knox key boxes. Valves shall be durably labelled as to what system the valve affects.
   e. The use of underground fire valves in the roadway, placed in "buffalo boxes" or similarly depicted enclosures shall be specifically identified and approved by the AHJ. Pavement markings identifying valves shall be required and maintained. Valve handles or "Tee" Handles or valve key, to control such valves shall be made available and kept on-site for fire personnel.
   f. Hydrant flow test values for sprinkler design purposes shall be no older than one year from the above ground (sprinkler) fire submittal date.
   g. If exterior building riser valves are in place in raised loading dock areas, they shall be accessible by dock platform stairs so that valves can be accessed and operated in a safe manner.
   h. Interior fire riser systems that have the potential to be struck by forklifts or similar warehouse type vehicle or devices shall be protected either by bollards, guard rails or similar AHJ approved devices.
   i. An "as-is" drawing of the fire sprinkler system shall be provided and posted in the riser or pump room of the building. The size of the drawing shall be at least 22"x34" (ANSI D) in size and no larger than 34"x44" (ANSI E). In multi-floor projects, each floor shall be a separate page. The maps shall either be mounted on a wall within the pump/riser room or reliably hung and removable from the wall. Maps shall be laminated. An electronic copy shall also be provided to the AHJ in PDF format.

23. **The following information as applicable, must be submitted with the sprinkler plans for review:**

Building height	Number of stories/floors	Mezzanines	Elevators
Hazard class	Commodity Class	Exterior storage	Fire protection

24. **Fire Hydrants:** Fire hydrants shall meet the Village of Pleasant Prairie hydrant specification. Fire hydrants shall be spaced no more than 350 feet apart around the perimeter of the building, per Village Ordinance §180-16. The distance from the finished grade line to the lowest discharge shall be no less than 18 inches and no more than 23 inches.
25. **Existing On-Premise Hydrants**: For properties with existing hydrants; Hydrants shall be evaluated and re-painted per AHJ specifications. At minimum, the designated FDC hydrant shall be retro-fitted with a Storz connection per Village specifications. Any Yard hydrant may be required to Storz retro-fitted based on-site review.
26. **Fire Protection Loop:** As applicable for building type or unless otherwise approved in writing by the AHJ, a fire protection (hydrant) loop shall be required as part of the overall fire protection systems as outlined in §180-16(K)(5).
27. **Locating Requirements:** Tracer locating wire to be installed as per WI SPS 382.30 for underground fire piping, including any remote FDC connections.
28. **Fire Hydrant Acceptance**: Prior to the fire sprinkler system connection to any new water mains (including water mains, fire hydrants, laterals leading to the building and risers) must be hydrostatically tested and flushed according to National Fire Protection Association (NFPA) code standard 24 and witnessed by the Fire Chief or designee.
29. **Fire Hydrant Colors**: The following hydrant color scheme shall be adopted;

REVISIONS:
- 03.06.26 SITE & OPERATIONAL RESUBMITTAL
- 03.26.26 SITE & OPERATIONAL COMMENTS
- 04.02.26 SUBMITTAL #4
- 04.07.26 SITE & OPERATIONAL CONDITIONAL APPROVAL SET

ZILBER INDUSTRIAL 3
108th St, Lakeview Corporate Park, Pleasant Prairie, WI

FIRE DEPARTMENT CONDITIONS AND REQUIREMENTS

2610 Lake Cook Road
Suite 280
Riverwoods, IL 60015
Ph.: (847) 940-0300
www.pidarchitects.com

PartnersinDesign
ARCHITECTS

PROJECT NO.: 522.22.031
DRAWN BY: CTS
CHECKED BY: WHB
DATE: 08.12.22
SHEET NO.: FD1.1

© 2026 Partners in Design Architects, Inc.

a. Any non-pressurized private hydrant shall be painted solid Blue. (Sherman Williams Blue Chip (SW6959) (Mueller Caution Blue F63RXL9667) in color, both barrel and caps. These fire hydrants are owned by the property owner and shall be maintained by the owner or tenant if identified in the lease agreement. This would include at minimum the FDC pumper pad hydrant.

b. Yard fire hydrants are located on a fire loop fed by a fire pump and shall be painted a solid yellow color, both barrel and caps. These fire hydrants are owned by the property owner and shall be maintained by the owner or tenant if identified in the lease agreement. Existing hydrants to re-paint using Mueller Yellow (Sherwin-Williams Safety Yellow SW4084). New factory Hydrants using Mueller Yellow (Sherwin-Williams Polane F63YL14).

c. Municipal fire hydrants located in the easement property, road right-of-way, shall be solid red in color, both barrel and caps. These fire hydrants are the owned by the municipality have jurisdiction and will be maintained by their respective organization. Paint color Mueller Red Sherwin Williams Polane F63RL15

d. Hydrants with Storz connections; do not paint the Storz portion of the hydrant.

e. Existing building with remodel or expansion projects shall re-paint all on premise hydrants to the current color scheme standard. Refer to the Project Supplement Guide for hydrant details.

30. **Fire hydrant / water main flushing:** The AHJ shall coordinate the flushing of all new water mains, fire hydrants, laterals leading to the building and risers with both the sub-contractors responsible, the Village of Pleasant Prairie Engineering Department, Fire & Rescue Department and the Water Utility Department, prior to seeking a "clean water sample" on this site. Water valves within the right-of-way shall only be operated by Village DPW employees.

31. **Pumper Pad:**

a. A municipally fed fire hydrant and fire department connection (FDC) combination is defined to be a "pumper pad".

b. See Fire hydrant Color scheme for FDC hydrant.

c. The FDC shall comprise of a 30 degree angled 5" Storz connection unless otherwise approved by the fire department in writing.

d. Both the hydrant and FDC shall between 18" and 23" above finished grade as a pair. Both the FDC connection and hydrant pumper nozzle shall face perpendicular to the curb or roadway.

e. There shall be dedicated space for a fire engine to have unobstructed access to the pumper pad.

f. The pumper pad shall be in close proximity to the fire pump room or riser room.

g. Wall mounted FDCs may be an option dependent on project details. AHJ written approval required.

h. Both the Fire Department Sprinkler connection and the fire hydrant shall be installed remote from the building and located a minimum distance from the building equal to the highest wall. Any variances shall be approved by the AHJ in writing.

i. The pumper pad shall be free of vegetation, plant, shrubs, or other obstructions at least 5 feet on each side.

j. The fire hydrant shall be located no more than five (5) feet from the roadway and the Fire Department sprinkler connection shall be placed no more than five (5) feet from the fire hydrant.

k. The Fire Department connection shall be constructed along with an underground drain with access for inspection. In cases where there is an accessible basement, the FDC drip/valve assembly may be located inside the basement. Should this situation present itself, written AHJ approval shall be required to utilize this arrangement.

l. The area around the pumper pad shall be comprised of a hard surface such as asphalt or concrete.

m. The pumper pad area shall have posted; signage and pavement markings as identified in detail FD-1 & FD-3 cut sheets.

n. Bollards shall not obstruct access to either the FDC or hydrant pumper nozzle.

o. Refer to the Village specification drawing FD-1 for the pumper pad design.

p. Existing FDCs shall be retro-fitted to the 5" Storz connection. The Siamese connection of any FDC shall be removed.

32. **Bollards:**

a. Shall be placed near fire hydrants, remote post indicator valves (PIV) and Fire Department connection(s) that are subject to damage.

b. Bollards shall not obstruct charged fire hoses.

c. It is recommended that the Fire Department approve the location of the bollard(s) before final placement is made.

d. Refer to detail FD-2 cut sheet.

33. **Hydrant Identification and Truck/vehicle parking:** In locations that maintain semi-trailer or related parking where the trailer/vehicle may hide or inhibit access to a hydrant, shall be visibly marked and maintained prohibiting using that space. See Fire Dept. Project Supplement Guide for detailed diagram.

34. **Fire Lane & Pavement Markings:** As required by the AHJ & project details, fire lane signage and pavement markings shall be required. Refer to Project Supplement Guide for pavement requirements.

35. **Standpipes:**

a. Where required, standpipes/hose valves shall be wet and placed adjacent to all exterior exit doors, same side as the door handle/knob. Village Ordinance 180.16 (I).

b. The building protection system shall be equipped with standpipes that shall consist of 2-½ inch NST valve, capable of delivering 250 GPM, at 75 PSI measured at the standpipe valve.

c. No 1-1/2" cap reductions are required.

d. Other standpipe configurations may be permissible with written AHJ approval.

e. Standpipe installation/location should be aware of other obstructions such as electrical outlets, light switches, fire alarm pull stations, and electrical boxes that typically reside in this general location. This concern is to avoid unsafe operation of the standpipe and surrounding devices.

36. **Fire Sprinkler Riser Protection:** Where interior fire risers are exposed to floor areas that have the potential to be struck by moving equipment such forklifts or similar devices, risers shall be protected by guardrails, bollards or similar crash barriers. These barriers are to be described and/or shown in the architectural drawings.

37. **Pump Room / Riser Room Door:**

a. The exterior door that accesses either the fire pump or riser room shall be labeled in the following manner outlined below

i. At the center upper 1/3 of the door, utilizing 4" reflective RED or WHITE block lettering contrasting to the door color, with the following title.

ii. "FIRE PUMP ROOM" or "FIRE RISER ROOM", respective for the type of existing room.

b. Other notification or placarding may be required based on facility or structure complexity.

c. This door shall have a Knox-Box installed adjacent to the door. The specific location heights and details are documented in the Project Supplement Guide attachment.

d. Hearing Protection; for facilities with fire pumps, hearing protection, either ear muffs, or ear plugs shall be provided by the tenant or owner.

e. This room shall contain as applicable, the building system map, underground drawings, and fire alarm device map as outlined in their specific system disciplines.

38. **MSDS / SDS Station:**

a. Within the pump or riser room locate a (SDS) Safety Data Sheet Station in a conspicuous and

accessible location. The station shall be labelled so to be readily identified.

b. Products used for maintenance, production or stored within the facility shall have their SDS information located at this SDS station.

c. The SDS information shall be organized in such manner that access to product information is intuitive.

d. The contents of the SDS station shall be updated and/or reviewed at least annually by the building owner or active tenant. A dated record log shall be kept with the SDS station indicating such review.

e. Other SDS station or electronic options per AHJ approval.

39. **Strobe Light(s):**

a. All strobe lights required below shall meet Village specifications as found in section 180-16(m) of the Sprinkler Ordinance. The lens color shall be **RED**.

b. A strobe light and 8" dome bell shall be provided, visible from the pumper pad to indicate a waterflow alarm condition.

c. If the building has a fire pump, an additional strobe light shall be required and installed adjacent to the waterflow alarm and activated when the fire pump is running.

d. Both notification devices above (b & c) shall be labeled appropriately as "WATERFLOW" and "PUMP RUN" below the respective devices. In instances where only one strobe is required, no signage is required. There may be situations where signage may be waived.

e. A strobe light shall be provided and installed vertically at each riser location on the exterior of the building. No bell or signage is required. In instances where two or more risers are located at one location, only one exterior strobe is required. The strobe shall activate on any one riser waterflow.

f. The heights of all strobe lights shall be sufficient to seen above standard semi-trailer heights or other obstructions applicable to the structure type or purpose.

g. Standard Strobe notifications devices (white strobe) used for the interior are not valid for exterior use. Verbal To Occupy or VTO shall not be granted should interior or non-standard devices be utilized.

h. Specific locations and layout typically are discussed with the AHJ and it is understood that various building finishes may impact exact locations.

i. A separate Project Supplement Guide document is available to provide visual detail supporting the above requirements.

40. **Fire Alarm System:** The system shall be designed and constructed to the NFPA 72 code-set. Confirm NFPA edition with the Fire Department prior to system design.

a. **Definitions:** For the purposes of this document; an **Alarm** condition requires primary notification to the AHJ dispatch center. A **Supervisory** condition does not notify the AHJ dispatch center.

b. **Addressable & Device point Transmission**: The system shall be addressable, having the ability to identify and display device points at the FACP and FAAP. The system shall be so configured to transmit the device point(s) to the supervising station and shall provide the device point description or equivalent of that information detail to the Communications Center (AHJ's dispatch or PSAP) during the conveyance/reporting of the alarm signal. Systems that only provide basic Alarm, Supervisory, or Trouble transmissions are not acceptable or permitted.

c. **Installation:** Installation of the Fire Alarm System shall be in accordance with NFPA 70 – The National Electrical Code and applicable local building codes and practices. A Village Low-voltage permit is also required.

d. **Combination Systems:** Systems combining burglar or security and fire alarm systems shall not be allowed. The Fire Alarm system shall be separate from both a security or burglar system.

e. **Manual Fire Alarm Pull Stations:** Shall be located at a minimum, immediately adjacent to each exterior door. Any additional exterior doors will be required to meet this requirement. The pull station shall not be placed around the door, but immediately adjacent to the door jamb. Pull stations shall require a key or set screw to reset the device. **No glass rods devices will be allowed**. Reset tools

shall be made available (2) for each Knox Box location, plus 4 additional.

f. **Manual Pull Stations – Protective Covers**: In retail and similar business occupancies where the potential exists for an increase of nuisance alarms, protective covers shall be installed with the pull stations to aide in the reduction of accidental and malicious activations. The AHJ may also require installation of protective covers for any project based on plan review findings. See additional details in the Project Supplement Guide.

g. **Pull Stations and Audiovisual Alarms:** Shall be installed per ADA requirements.

h. **Smoke and Heat Detection:** Shall be installed as required.

i. **Tamper Switches:** Shall be installed as required.

j. **PIV & Exterior Valves:** Shall be monitored by the Fire Alarm system or locked as applicable in Code. Exterior wall mounted riser valves shall be durably labeled with the system that it controls. Labels/placards shall be affixed to the wall directly above the valve control.

k. **Strobe & Bell:** Strobe light and Bell devices shall be identified and documented on the submitted Fire Alarm plan submittal. It is understood that typically this work is completed by the electrical contractor and not part of the alarm plan per say.

l. **Duct Detectors:** Duct detectors shall be programmed as a Supervisory condition, not as an Alarm condition unless pre-approved by the AHJ or required by Code.

m. **Fire Pump Run:** A fire pump run condition shall be treated as an Alarm condition.

n. **Fire Alarm Plans Location:** There shall be a designated location for a set of as-built fire alarm plans near the FACP per NFPA 72.

o. **FACP Nomenclature:** Confirmation of nomenclature shall be discussed between the Fire Department and the fire alarm program technician prior to any inspections. Nomenclature programming download or document (xlsx/csv) to be provided to the AHJ no less than 72 hours prior to any scheduled inspections. Nomenclature device descriptions shall incorporate building door numbering whenever feasible.

p. **Initiating Devices Labeling:** All initiating devices e.g.: pull stations, smoke detectors, tampers, etc shall be labeled with the FA device point or number that matches the system nomenclature programmed. The font/letters shall be at least 14pt and/or of such size that they are visible based on accessibility to the device. (e.g.: ceiling initiating devices may require a larger font size). Labeling shall be in a contrasting color as to the surface that the label is affixed to.

q. **Annunciator Panel:** The annunciator panel (FAAP) type shall be approved by the AHJ. The FAAP shall display alarm, trouble, and supervisory conditions along with the device point and description and be capable of full function (Silence, reset). Locations for FAAP(s) shall be identified in the AHJ plan review and documented on the approved system drawing. The FAAP shall either require no key or keyed activation. **FAAP models that require a password will not be accepted.**

r. **Transmission of Fire Alarms.** The method of transmission to supervising station shall be documented within the submittal and approved by the AHJ. (e.g. RF Radio/Mesh network, cellular, VOIP, MFVN, or other approved technologies allowed by Code.)

s. **FACP Main Panel:** There will be one main fire alarm panel within a building. The system will not be split into two or multiple fire alarm panels interconnected together. (Example: West wing is one panel; East wing is a different panel). Written AHJ approval shall be required for large facilities to tie-in large systems by technology methods.

t. **FACP Breaker Disconnect Lock:** Where required, provide commercial circuit lockout device NFPA 72 [2025] 10.6.5.4

u. **FACP Location:** The main fire alarm panel shall be located in the fire pump or riser room. Any other location shall be identified in advance and in writing. The AHJ shall review and approve. Any deviation shall be conveyed in writing to the AHJ prior to any submitted plans or construction.

v. **Fire Alarm Map:** An "as-is" drawing of the fire alarm system shall be provided and posted in the riser

or pump room of the building. The drawing shall have at minimum, the initiating device numbers, locations, and door numbering scheme on the posted drawing. The size of the drawing shall be at least 22"x34" (ANSI D) in size and no larger than 34"x44" (ANSI E). In multi-floor projects, each floor shall be a separate page. The maps shall either be mounted on a wall within the pump/riser room or reliably hung and removable off the wall. Maps shall be laminated. An electronic copy shall also be provided to the AHJ in PDF format. Refer to the Project Supplement Guide for further details.

w. **Supervising Station:** The Fire Alarm Control Panel (FACP) shall transmit all alarm, trouble and supervisory signals to a supervising station as defined by NFPA 72, that is certified by Underwriters Laboratories (UL) and/or Factory Mutual (FM) and approved by the Fire & Rescue Department. The owner shall provide such documentation for approval. The supervising station shall utilize the **Alarm reporting** number listed for the conveyance of all alarm condition signals.

41. **Public Safety Contact Numbers:**

PUBLC SAFETY PROVIDERS	
Fire Suppression & Rescue Services	Pleasant Prairie Fire & Rescue
EMS & Medical	Pleasant Prairie Fire & Rescue
Law Enforcement	Pleasant Prairie Police
PHONE NUMBERS	
Emergency	911 (Reporting to Kenosha Joint Services)
Alarm Reporting	**(262) 694-1402**
Dispatch Non-emergency	(262) 694-7105
Fire Dept. Business	(262) 948-8975

42. **All Hazards Notification System:** Should the owner or tenant plan on the installation of an in-building all hazards notification system (fire, weather, active threat, etc), the fire department shall be made aware and the system shall meet all NFPA 72 requirements.

43. **Electric Vehicle (EV) Charging Station:** Any installation of an electrical system to charge electric vehicles shall at minimum have the following elements considered. Additionally, the project person shall discuss with the AHJ, the proposed details for the charging station at the conceptual phase of any given project.

a. Charging station spacing
b. Adequate lighting
c. Emergency notification – ie: phone
d. Charging station electrical remote shutoff
e. Placarding

44. **Final Inspection:** The General Contractor shall be responsible to provide or confirm from the MEPs that the following system related documents have been delivered to the AHJ throughout the project and before a final occupancy scheduled:

a. **100% Completion Letters** – Shall be delivered on company letterhead and stamped or signed by an authorized agent of the organization. Letters shall include at minimum, the project name, address, and scope of work description, along with an authorized signatory of the organization. Email message statements are not acceptable.

1. The fire protection contractor shall provide the AHJ with a letter (upon completion of the sprinkler work) stating the sprinkler and protection systems, or portion thereof, are "100% operational and built according to the AHJ stamped plan design", Village Ordinance, 180-16 N if modifications are made to the system, as-built plans shall be provided.

2. The fire alarm contractor shall also provide the AHJ with a letter (upon completion of the fire alarm work) stating the fire alarm system, or portion thereof, is "100% operational and built according to the approved AHJ stamped design" if modifications are made to the system, as-built plans shall be provided.

3. The contractor responsible for any fire protection (fire loop or FDC) underground and/or FDC connection/pumper pad construction shall also provide the AHJ with a letter (upon completion of the underground work) stating the underground fire protection (piping) system, or portion thereof, is "100% operational and built according to the approved AHJ stamped design" if modifications are made to the system, as-built plans shall be provided.

b. Contract copy with fire alarm central monitoring station.

c. UL and/or FM certificate(s) for the contracted fire alarm central monitoring station.

d. As applicable, fire pump test documentation.

e. Fire protection underground flushing documents.

f. Underground and fire sprinkler (Wet & Dry) hydrostatic test certificates.

g. Clean Agent System documentation as applicable.

h. Copies of the fire sprinkler operational test certificates.

i. Copies of the fire alarm test documents. – Record of Completion

j. Copies of other related system documents such as, hood/duct, smoke, etc…

k. The Pleasant Prairie Fire and Rescue Department shall have all information needed for our pre-fire plan prior to occupancy.

l. Provide in an electronic PDF format, floor plans and fire protection (Sprinkler/Fire Alarm) plans for the building in an as-built condition.

m. System drawings of the fire alarm and fire sprinkler system shall be placed in the fire pump or riser room, near the fire alarm control panel as outlined in their respective system comments (above). An electronic copy of each system shall be provided in PDF format

n. AED is in place and in an operational state, as required at such time that the occupancy inspection is conducted.

o. A copy of the Emergency Plan must be submitted to the Fire & Rescue Department before occupancy.

###

2026/v1

REVISIONS
- 03.06.26 SITE & OPERATIONAL RESUBMITTAL
- 05.06.26 SITE & OPERATIONAL COMMENTS
- 07.24.26 SUBMITTAL #4
- 09.02.26 SITE & OPERATIONAL CONDITIONAL APPROVAL SET

ZILBER INDUSTRIAL 3
108th St, Lakeview Corporate Park, Pleasant Prairie, WI


FIRE DEPARTMENT CONDITIONS AND REQUIREMENTS

2610 Lake Cook Road
Suite 280
Riverwoods, IL 60015
Ph.: (847) 940-0300
www.pidarchitects.com

PartnersinDesign
ARCHITECTS

PROJECT NO.: 522.22.031
DRAWN BY: CTS
CHECKED BY: WHB
DATE: 08.12.22
SHEET NO.: FD1.2


© 2026 Partners in Design Architects, Inc.

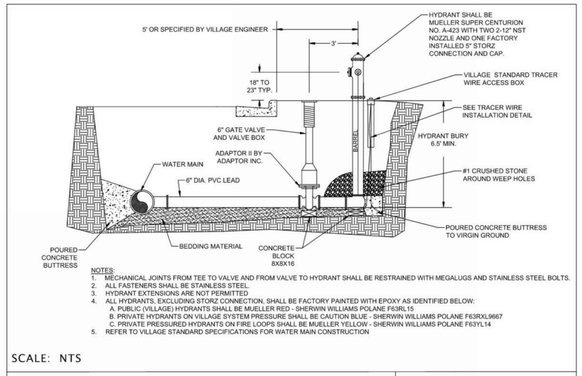

NOTES:
1. MECHANICAL JOINTS FROM TEE TO VALVE AND FROM VALVE TO HYDRANT SHALL BE RESTRAINED WITH MEGALUGS AND STAINLESS STEEL BOLTS.
2. ALL FASTENERS SHALL BE STAINLESS STEEL.
3. HYDRANT EXTENSIONS ARE NOT PERMITTED
4. ALL HYDRANTS, EXCLUDING STORZ CONNECTION, SHALL BE FACTORY PAINTED WITH EPOXY AS IDENTIFIED BELOW:
   A. PUBLIC (VILLAGE) HYDRANTS SHALL BE MUELLER RED - SHERWIN WILLIAMS POLANE F63RL15
   B. PRIVATE HYDRANTS ON VILLAGE SYSTEM PRESSURE SHALL BE CAUTION BLUE - SHERWIN WILLIAMS POLANE F63RXL9667
   C. PRIVATE PRESSURED HYDRANTS ON FIRE LOOPS SHALL BE MUELLER YELLOW - SHERWIN WILLIAMS POLANE F63YL14
5. REFER TO VILLAGE STANDARD SPECIFICATIONS FOR WATER MAIN CONSTRUCTION

SCALE: NTS

STANDARD HYDRANT ASSEMBLY	DETAIL: W - 1
DATE: 8-19-19	VILLAGE OF PLEASANT PRAIRIE
APPROVED BY: MATT FINEOUR	KENOSHA COUNTY, WISCONSIN

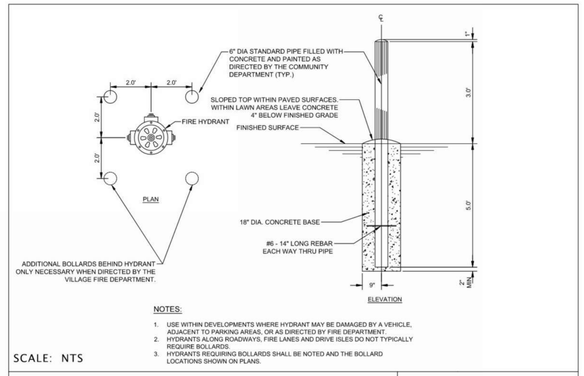


NOTES:
1. USE WITHIN DEVELOPMENTS WHERE HYDRANT MAY BE DAMAGED BY A VEHICLE, ADJACENT TO PARKING AREAS, OR AS DIRECTED BY FIRE DEPARTMENT.
2. HYDRANTS ALONG ROADWAYS, FIRE LANES AND DRIVE ISLES DO NOT TYPICALLY REQUIRE BOLLARDS.
3. HYDRANTS REQUIRING BOLLARDS SHALL BE NOTED AND THE BOLLARD LOCATIONS SHOWN ON PLANS.

SCALE: NTS


DEVELOPMENT HYDRANT BOLLARD	DETAIL: FD - 2
DATE: 4-8-22	VILLAGE OF PLEASANT PRAIRIE
APPROVED BY: C. ROEPKE	KENOSHA COUNTY, WISCONSIN

VALVE PAVEMENT MARKING EXAMPLE

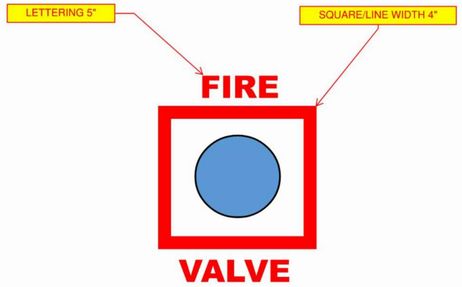

To be utilized when underground pavement fire valves are used.


NOTE:
1. SYSTEM SIZING SHALL BE COMPLETED BY A FIRE SUPPRESSION ENGINEER AND APPROVED OF BY THE VILLAGE OF PLEASANT PRAIRIE FIRE DEPARTMENT.
2. SYSTEM INSTALLATION MUST BE CONSTRUCTED UNDER THE ONSITE SUPERVISION OF A LICENSED SPRINKLER FITTER.
3. WHEN POSSIBLE THE CHECK VALVE WITH BALL DRIP SHALL BE PLACED WITHIN THE BUILDING BASEMENT REMOVING THE NEED FOR THE MANHOLE STRUCTURE. THE BALL DRIP SHALL BE A MIN. 6' BELOW THE SURFACE ELEVATION OF THE PUMPER PAD IN EITHER LOCATION.

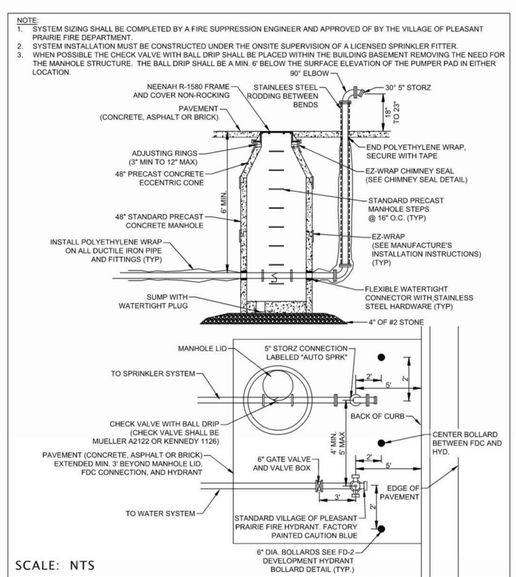

SCALE: NTS

PUMPER PAD FDC DETAIL	DETAIL: FD - 1
DATE: 8-19-19	VILLAGE OF PLEASANT PRAIRIE
APPROVED BY: C. ROEPKE	KENOSHA COUNTY, WISCONSIN


NOTES:
1. SIGNS SHALL BE SPACED NOT GREATER THAN SIXTY (60) FEET APART. NO PART OF THE FIRE LANE SHALL BE FURTHER THAN 30 FEET FROM A SIGN.
2. SIGNS SHALL BE MOUNTED ON ROUND 2-3/8" DIAMETER GALVANIZED STEEL POSTS POWDER COATED BLACK, DARK BRONZE OR OTHER COLOR APPROVED BY THE VILLAGE COMMUNITY DEVELOPMENT DEPARTMENT.
3. THE MINIMUM HEIGHT, MEASURED VERTICALLY FROM THE TOP OF THE SIGN TO THE TOP OF THE CURB, OR IN THE ABSENCE OF CURB, MEASURED VERTICALLY FROM THE TOP OF THE SIGN TO THE ELEVATION OF THE NEAR EDGE OF THE TRAVELED WAY SHALL BE 6'-6".
4. WHERE A CURB IS PROVIDED, TOP AND FACE SHALL BE PAINTED YELLOW. PAVEMENT MARKING STRIPES SHALL BE YELLOW, FOUR INCHES (4") WIDE AND EXTENDING OUTWARD TO A WIDTH OF FOUR (4) FEET FROM CURB FACE WITH THREE (3) FEET BETWEEN EACH STRIPE.
5. YELLOW PAVEMENT MARKING LETTERS NOT LESS THAN FOUR (4) INCHES IN HEIGHT AND NOT LESS THAN TWO (2) INCHES IN WIDTH WITHIN THE STRIPING (BETWEEN THE POSTED SIGNS) TO READ "NO PARKING FIRE LANE".
6. SIGNS AND PAINTING ARE TO BE MAINTAINED BY THE PROPERTY OWNER.

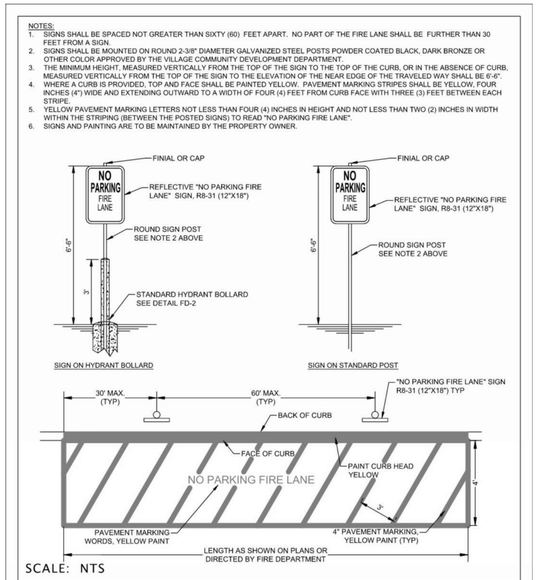

SCALE: NTS

FIRE LANE MARKING AND SIGNING	DETAIL: FD - 3
DATE: 4-8-22	VILLAGE OF PLEASANT PRAIRIE
APPROVED BY: C. ROEPKE	KENOSHA COUNTY, WISCONSIN

Hydrant Truck Vehicle parking Pavement Markings Project Guide

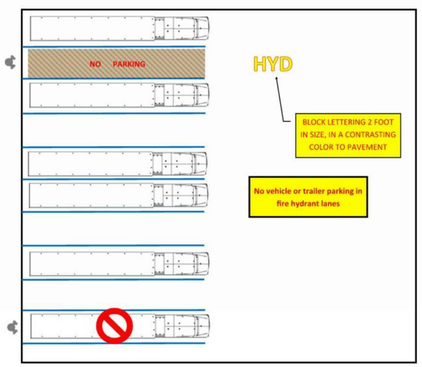

This guide depicts a truck parking yard that has fire hydrants along the curb. No Truck parking is allowed that would obstruct access and use to a hydrant. Pavement markings shall be provided as shown. The lane shall be diagonally stripped and lettered in a manner similar as shown. The "HYD" designation shall be placed as shown to allow a visual notification of a "Hydrant lane" that may be obscured by adjacent trucks. Lettering size shall be proportional as depicted in the drawing.

1/2020; HydrantTruckParkingMarkings

© 2026 Partners in Design Architects, Inc.

REVISIONS
1. 03.02.26 SITE 1 OPERATIONAL RESUBMITTAL
2. 05.11.26 SITE 1 OPERATIONAL COMMENTS
3. 07.24.26 SUBMITTAL #4
4. 09.02.26 SITE 1 OPERATIONAL CONDITIONAL APPROVAL SET

ZILBER INDUSTRIAL 3
108th St, Lakeview Corporate Park, Pleasant Prairie, WI

FIRE DEPARTMENT DETAILS AND SPECIFICATIONS

2610 Lake Cook Road
Suite 280
Riverwoods, IL 60015
Ph.: (847) 940-0300
www.pidarchitects.com

PartnersinDesign ARCHITECTS

PROJECT NO.: 522.22.031
DRAWN BY: CTS
CHECKED BY: WHB
DATE: 08.12.22
SHEET NO.: FD1.3

KNOX
When seconds matter.

KNOXVAULT® 4400
SINGLE LOCK MODEL

The KnoxVault 4400 is a secure, high capacity key lock box trusted by first responders, property owners, and universities. Store up to 50 keys, access cards and/or emergency plans to quickly gain rapid emergency access to large business and industrial facilities and campuses.



WEIGHT:
Surface Mount - 28 lbs
Recessed Mount - 29 lbs


DIMENSIONS:
Surface Mount Body - 7"H x 7"W x 5"D
Recessed Mount Flange - 9 1/2"H x 9 1/2"W

FEATURES
- Large capacity, storing up to a 50 keys. Access cards, entry items, emergency planning documents, and FDC Keywrench may also fit in interior compartment but will reduce max key quantity.
- Built Knox-Rugged and secure: UL 1037, UL 1610, UL 1332, UL 437
- Finished with Knox-Coat® to protect four times better than standard powder coat
- Extreme weather-resistant door gasket

BENEFITS
- Allows rapid property access
- Reduces property damage
- Prevents forced entry into buildings
- Minimizes first responder injury
- Compliant to National Fire Code (NFPA, IFC, IBC)

OPTIONS
- Knox Tamper Alert connects to building's alarm system for extra security
- Mount types: Recessed and Surface
- 3 color options: Black, Aluminum, Dark Bronze
- Dual lock configuration

ACCESSORIES
- Multi-Purpose Switch for use on electrical doors, gates and other electrical equipment
- Recess Mounting Kit for new concrete or masonry construction
- Public Safety Labels
- Tag-Out Tamper Seals
- Key Tags
- Key Rings

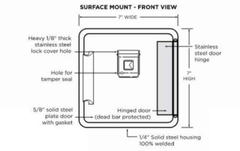

ORDERING SPECIFICATIONS

To insure procurement and delivery of the KnoxVault 4400, it is suggested that following specification paragraph is used:

KnoxVault surface/recessed mount with/without UL Listed Knox Tamper Alert. 1/4" plate steel housing, 5/8" thick steel door with interior gasket seal and stainless steel door hinge. Vault & lock UL Listed. Lock has 1/8" thick stainless steel dust cover with tamper seal mounting capability. Vault has anti-theft re-locking mechanism with drill resistant hard-plate lock protector.

Exterior Dimensions: Surface Mount - 7"H x 7"W x 5"D
Recessed Mount Flange - 9 1/2"H x 9-1 /2"W

Lock: UL Listed. Double-action rotating tumblers and hardened steel pins accessed by a biased cut key.

Finish: Knox-Coat® proprietary finishing process

Color: Black, Dark Bronze or Aluminum

P/N: KnoxVault 4400 (mfr's cat. ID)

Mfr's Name: KNOX COMPANY

1601 W. DEER VALLEY RD, PHOENIX, AZ 85027 | T. 800-552-5669 | F. 623-687-2290 | INFO@KNOXBOX.COM | KNOXBOX.COM

©Knox Company. All rights reserved.

MKT-KBSPEC-0023-C


KNOX
When seconds matter.

KNOXVAULT® 4400
SINGLE LOCK MODEL

GENERAL MOUNTING INSTRUCTIONS

Suggested minimum mounting height, 6 feet above ground.

ATTENTION: KnoxVault is a very strong device that MUST be mounted properly to ensure maximum security and resist physical attack.

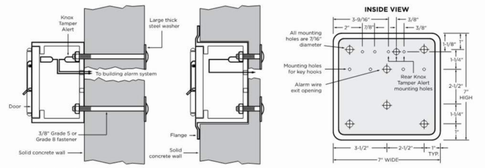


KnoxVault 4400 Surface Mount **KnoxVault 4400 Recessed Mount**

RECESS MOUNTING KIT AND INSTALLATION INSTRUCTIONS

The Recess Mounting Kit (RMK) includes shell housing and mounting hardware, which may only be used for recessed models to cast-in-place within new concrete or masonry construction. The KnoxVault is mounted into the shell housing after construction is completed.

Recessed Mounting Using Recess Mounting Kit (RMK)

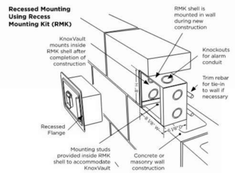

RECESS MOUNTING KIT DIMENSIONS
Rough-in Dimensions:
8-1/2"H x 8-1/2"W x 7"D

IMPORTANT:
Care should be taken to ensure the front of the Recess Mounting Kit (RMK) shell housing, including the cover plate and screw heads, is flush with the wall. The RMK must be plumbed to ensure vertical alignment of the vault.

ABOUT KNOX COMPANY

Over forty years ago, a unique concept in rapid access for emergency response was born. The KnoxBox®, a high-security key lock box, was designed to provide rapid access for emergency responders to reduce response times, minimize injuries and protect property from forced entry.

Today, one revolutionary lock box has grown into a complete system providing rapid access for public safety agencies, industries, military, and property owners across the world. The Knox Company is trusted by over 14,000 fire departments, law enforcement agencies, and governmental entities.

KNOX COMPANY
1601 W. DEER VALLEY RD
PHOENIX, AZ 85027

T. 800.552.5669
F. 623.687.2290

KNOXBOX.COM
INFO@KNOXBOX.COM

MUELLER® FIRE HYDRANT
STORZ
Pumper Connections

Quick-Connect / Full Pressure Rating

Mueller Centurion hydrants (traditional or Modern styles), can be ordered with an integral, Mueller designed and manufactured Storz connection on the pumper nozzle. The connection is also available separately to retrofit hydrants in the field. Making our own Storz connection means your Centurion hydrants remain '100% Mueller' for assurance of reliability.

The Mueller Storz connection allows the fire department to connect its pumper hose to the hydrant with a quick, quarter-turn action. The action is fast and smooth so fire fighters can get to their tasks quickly without the thread alignment, cross threading, or leakage problems sometimes associated with threaded connections.

The Mueller Storz option is available for 4" and 5" pumper nozzles on any Centurion 200™, 250™, or Modern hydrant. Mueller hydrants retain their UL Approval, FM Listing, AWWA Compliance and published pressure rating when ordered with the Storz option. Hydrants are also compliant with NFPA 1963. To order, specify Storz size, and locking or non-locking caps.

Mueller Storz retrofit Part# 287305 for 5 Inch Storz - Locking caps



Storz retrofit Contractor Information:	Mueller Regional Rep
Joe Kuhaupt Wisconsin Hydrant Repair 414.550.9475 wisconsinhydrantrepair@gmail.com	Bob Boyer bboyer@muellerwp.com 262.689.6530

For more information, contact your local authorized Mueller Distributor, Mueller Sales Representative, or call our Customer Service Center at 1-800-423-1323.

>>ALWAYS VERIFY YOUR HYDRANT STYLE/MFG BEFORE PROCEEDING<<

Mueller Co.
Smart Move

Mueller Co.
633 Chestnut St., Suite 1200
Chattanooga, TN 37450
www.muellercompany.com
moreinfo@muellercompany.com

Phone: 1.423.209.4800
Toll Free: 1.800.423.1323
Canada: 1.705.719.9965
International: 1.423.490.9555

Copyright © 2015 Mueller Co., LLC. All Rights Reserved.
The trademarks, logos and service marks displayed in this document herein are the property of Mueller Co., LLC, its affiliates or other third parties. Products above marked with a section symbol (§) are subject to patents or patent applications. For details, visit www.mwppat.com. These products are intended for use in potable water applications. Please contact your Mueller Sales or Customer Service Representative concerning any other application(s).

Form 12272 - Rev 11/15

FIRE PRODUCTS

STI STOPPER II®



PRODUCT OVERVIEW

This protective cover has been helping to stop false fire alarms around the world for more than 40 years, without restricting legitimate alarms. All models offer excellent protection against physical damage (both accidental and intentional) and several against severe environments both inside and out. It is ideal for schools, colleges, hospitals, nursing homes, stores, hotels and public buildings of almost every kind where there is a threat of false alarms.

HOW IT WORKS

Stopper II consists of a clear, tamperproof, tough polycarbonate shield and frame, but the line includes models with the option of a piezo horn, spacer and gaskets. The cover accommodates most manual pull stations. When the Stopper II with horn is lifted to gain access to the protected alarm, a piercing self-contained 95 or 105 dB warning horn (at one foot) sounds. Immediate attention is drawn to the area and a prankster will either run or be caught. The cover is connected to the frame by a cable. When the cover is lifted, it drops off of the frame and a horn will sound (models with horn) until the cover is snapped back onto the frame or for the life of the battery.

KEY FEATURES

General Information
- Proven effective for more than 40 years in helping stop false fire alarms without restricting legitimate alarms.
- Can be used as a guard against physical damage to a manual pull station, with or without the optional warning horn.
- Three year guarantee against breakage of polycarbonate in normal use (one year on electro mechanical and electronic components).

Design
- Larger sizes and surface mounted pull stations accommodated with STI-3100 conduit spacer.
- Weather models have closed cell gaskets.
- The Stopper II design is a registered trademark of Safety Technology International, Inc.

Construction
- UL Listed to U.S. and Canadian safety standards (also for custom labeling).

Installation
- When covering a pull station outside, UL requires stations to be listed for outdoor use.
- Typical working properties of polycarbonate are -40° to 250°F (-40° to 121°C).

Electronics
- Power source is a 9V DC alkaline battery included on standard Stopper II (remote powered unit available).

Options
- Optional horn has a choice of 95 or 105 dB at one foot.
- Standard red units have "In Case of Fire..." label unless specified with "NR" (no label) or "CR" (custom label).

For more information, call 248-673-9898 or visit www.sti-usa.com.

Safety Technology International

STI Stopper II®
Dimensions and Technical Information

MODELS AVAILABLE

Stopper II® Models Indoor Use

STI-1100*★	With horn for flush mount
STI-1130*★	With horn and spacer
STI-1200*★	Without horn flush mount
STI-1230*★	Without horn with spacer

Weather Stopper® with gaskets (Indoor/Outdoor rated)

STI-1150*	With horn flush mount and gaskets
STI-1155*	With horn surface mount and gaskets
STI-1250*	Without horn flush mount and gaskets
STI-3150*★	Without horn surface mount and gaskets

Accessories

KIT-316	Louvers for STI-3100
KIT-H19015	Two 3/32" Allen wrenches
KIT-M02002	Clear Frame for Stopper II Series
STI-1102	Replacement horn for cover with alarm
STI-1280	Backplate
STI-3002	Weather gasket
STI-3003	Conduit gasket
STI-3004	Rigid conduit gasket
STI-3100	2" conduit spacer with a frame, ½" or ¾" conduit entry
STI-3104	2" conduit spacer with ½" or ¾" conduit entry (includes one ¾" conduit entry gasket)

Add -NR for no label on horn housing
Add -CR for custom label on horn housing (2 lines/40 characters max. each line)
Add -FR for French lab

★ **Available in a 6-pack (STI-1100 & STI-1130 also in a 12-pack)**

APPROVALS & WARRANTY


TESTING
It has been tested and approved or listed by:
- UL/cUL Listed No. S2466
- For fire alarm applications, UL38 requires outdoor listed stations for outdoor use
- State of California (obtain local fire marshal approval)
- MEA 49-00-E (STI-1200)
- Flush models ADA Compliant. Surface models ADA Compliant for operation
- Weather Stopper® versions designed to meet the requirements of IP54.
- The indoor/outdoor rated station covers, when mounted on a smooth surface, provide a rain tight seal similar to a 3R enclosure rating.


WARRANTY
Three year guarantee against breakage of polycarbonate in normal use (one year on electro mechanical and electronic components).

IMPORTANT NOTICE

Stopper II "FIRE" models are intended to be used in areas where the incidence of false fire alarms from manual pull stations is high or has proven to be a serious problem. Any disadvantage of this device is more than balanced when one considers the consequences of false fire alarms, especially if fire service personnel and equipment are responding to a false fire alarm when they are needed for a real fire somewhere else. Add to this the disruption to the facility when false alarms occur. If you have, or may have, a problem with false fire alarms or physical/weather damage to your fire alarm activation devices, the Stopper II could prove invaluable.

*WARNING: ⚠For RC models: UL Listing does not permit relay contacts to connect to the fire alarm or a life safety function. The power supply for horns, according to UL Listing, cannot be connected to a UL Listed fire alarm system. For electrical specifications see install book. RC models contain one set of Form "C" dry contacts. Contacts rated 30 VAC/VDC 1 amp.

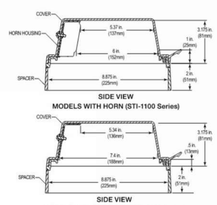

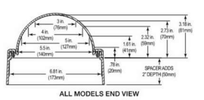

EXTERNAL DIMENSIONS:
- Flush 7.2 W x 10.2 H x 3.3 D in. (183x259x84mm)
- Surface 7.2 W x 10.2 H x 5.5 D in. (183x259x140mm)

Safety Technology International
2106 Airport Road, Waterford, MI 48327, USA
info@sti-usa.com
www.sti-usa.com
Tel:248-673-9898

Taylor House, 34 Sherwood Rd., Bromsgrove, Worcs., B60 3DR, England
info@sti-emea.com
www.sti-emea.com
Tel: +44 (0) 1527 520 999

Unit 7A Lockheed Avenue, Airport Business Park, Waterford X91 HWF2, Ireland

© 1987-2022 Safety Technology International, Inc.

Subject to change without notice. 09/22

ZILBER INDUSTRIAL 3
108th St, Lakeview Corporate Park, Pleasant Prairie, WI
FIRE DEPARTMENT DETAILS AND SPECIFICATIONS

2610 Lake Cook Road
Suite 280
Riverwoods, IL 60015
Ph.: (847) 940-0300
www.pidarchitects.com

Partners in Design
ARCHITECTS

REVISIONS
1 05.12.26 SITE 1 OPERATIONAL RESUBMITTAL
2 05.15.26 SITE 1 OPERATIONAL COMMENTS
3 07.24.26 SUBMITTAL #4
4 09.22.26 SITE 1 OPERATIONAL CONDITIONAL APPROVAL SET

PROJECT NO.: 522.22.031
DRAWN BY: CTS
CHECKED BY: WHB
DATE: 08.12.22
SHEET NO.: FD1.4

© 2026 Partners in Design Architects, Inc.